

INTERIOR DRAWING

TGMM YANGON OFFICE

Status For Tender
Issue T1
Date 10 APRIL 2020

LUX 89 COMPANY LIMITED 7/89 Vista Park Rama II Soi 54/4, Samae Dam,
Bang Khun Thian, Bangkok , Thailand10150
E CHAYANAN.LUX89@GMAIL.COM, LUX89.BKK@GMAIL.COM
T 66(2) 416 9189

LUX 89

SAKURA TOWER , UNIT 1603- 1605 &1607-1608, LEVEL 16 FLOORS

© LUX89 CO., LTD. April 2020

REFERENCE MAP			NORTH		
NOTES 1. DO NOT SCALE DRAWINGS. WRITTEN DIMENSIONS GOVERN. 2. ALL DIMENSIONS ARE IN MILLIMETERS UNLESS NOTED OTHERWISE. 3. THE WORK: LUX89 SHALL BE NOTIFIED IN WRITING OF ANY DISCREPANCIES. 4. THIS DRAWING MUST BE READ IN CONJUNCTION WITH ALL RELEVANT CONTRACTS, SPECIFICATIONS, REPORTS AND DRAWINGS.					
© 2020 COPYRIGHT OF THIS DRAWING IS VESTED IN LUX89 CO., LTD.					
THIS DRAWING IS AN UNCONTROLLED COPY. UNLESS NOTED OTHERWISE					
T1	CP	FOR TENDER			10/04/2020
REV	BY	DESCRIPTION			DATE
CLIENT / PROJECT					
Tilleke & Gibbins Myanmar Limited.					
PROJECT MANAGER & INTERIOR DESIGNER					
LUX 89 CO., LTD. 7/89 Soi Rama 2 Soi 54/4,Samae Dam, Bang Khun Thian, Bangkok , Thailand10150 E LUX89.BKK@GMAIL.COM W LUX89.COM T 66(2) 416 9189					
ARCHITECTURE					
STRUCTURE ENGINEER					
M&E ENGINEER					
ACCO ENGINEERING CO., LTD. 1213/430 Soi Ladprao94 (Panjarnit) Plubpla, Wang Thonglang, Bangkok, Thailand. 10310 E APISAK@ACCO.CO.TH W ACCO@ACCO.CO.TH T 66(2) 559 0177-9, F 66 (2) 559 0176					
DRAWING					
LIST OF DRAWING					
STATUS					
FOR TENDER					
SCALE AT 1:100	DRAWN	CHECKED	FLUTTER		
AK	CP	CP		10/04/2020	
JOB NO.	DRAWING NUMBER			REASON	
PTD 20.001	D-001			T1	

A modern office reception area. On the left, a white reception desk with a dark wood base holds a laptop and a small potted plant. The wall behind the desk is made of light-colored stone tiles. The ceiling features a wooden slatted design with recessed lighting. In the background, a glass-walled office space is visible, with the name "Tillett & Gibbins" on the wall. The floor is made of large, light-colored marble tiles. On the right, a black leather sofa is partially visible.

A modern office interior featuring a long wooden table, black ergonomic chairs, and two large, cylindrical pendant lights. The ceiling is made of horizontal wooden slats, and the walls are a combination of wood paneling and frosted glass partitions. The floor is covered in a dark, patterned carpet.

REFERENCE MAP	NOTES

NOTES

1. DO NOT SCALE DRAWINGS. WRITTEN DIMENSIONS GOVERN.
2. ALL DIMENSIONS ARE IN MILLIMETERS UNLESS NOTED OTHERWISE.
3. ALL DIMENSIONS SHALL BE VERIFIED ON SITE BEFORE PROCEEDING WITH THE WORK. LUX89 SHALL BE NOTIFIED IN WRITING OF ANY DISCREPANCIES.
4. THIS DRAWING MUST BE READ IN CONJUNCTION WITH ALL RELEVANT CONTRACTS, SPECIFICATIONS, REPORTS AND DRAWINGS.

© 2020 COPYRIGHT OF THIS DRAWING IS VESTED IN LUX89 CO., LTD.

THIS DRAWING IS AN UNCONTROLLED COPY. UNLESS NOTED OTHERWISE

[illegible]

T1	CP	FOR TENDER	10/04/2020
REV	BY	DESCRIPTION	DATE

CLIENT / PROJECT

**Tilleke & Gibbins
Myanmar Limited.**

PROJECT MANAGER & INTERIOR DESIGNER

LUX 89 CO., LTD.
7/89 Soi Rama 2 Soi 54/4, Samae Dam,
Bang Khun Thian, Bangkok, Thailand 10150
E LUX89.BKK@GMAIL.COM W LUX89.COM
T 66(2) 416 9189

ARCHITECTURE

STRUCTURE ENGINEER

M&E ENGINEER

ACCO ENGINEERING CO., LTD.
1213/430 Soi Ladprao94 (Panjamit) Plubpla, Wang Thonglang,
Bangkok, Thailand. 10310
E APISAK@ACCO.CO.TH W ACCO@ACCO.CO.TH
T 66(2) 559 0177-9, F 66 (2) 559 0176

DRAWINGS

PERSPECTIVE
RECEPTION & MEETING 6 PAX.

STATUS

FOR TENDER

SCALE AT A1:A3	DRAWN	CO-ORDINATED	CHECKED	PLOTTED DATE
	AK	CP	CP	10/04/2020

JOB NO. PTD 20.001	DRAWING NUMBER D-009	REVISION T1
------------------------------	--------------------------------	-----------------------

ETH

1. DO NOT SCALE DRAWINGS. WRITTEN DIMENSIONS GOVERN.
2. ALL DIMENSIONS ARE IN MILLIMETERS UNLESS NOTED OTHERWISE.
3. ALL DIMENSIONS SHALL BE VERIFIED ON SITE BEFORE PROCEEDING WITH THE WORK. LUX89 SHALL BE NOTIFIED IN WRITING OF ANY DISCREPANCIES.
4. THIS DRAWING MUST BE READ IN CONJUNCTION WITH ALL RELEVANT CONTRACTS, SPECIFICATIONS, REPORTS AND DRAWINGS.

THIS DRAWING IS AN UNCONTROLLED COPY. UNLESS NOTED OTHERWISE

T1	CP	FOR TENDER	10/04/2020
REV	BY	DESCRIPTION	DATE

**Tilleke & Gibbins
Myanmar Limited.**

LUX 89 CO., LTD.
7/89 Soi Rama 2 Soi 54/4, Samae Dam,
Bang Khun Thian, Bangkok , Thailand 10150
E LUX89.BKK@GMAIL.COM W LUX89.COM
T 66(2) 416 9189

STRUCTURE ENGINEER

ACCO ENGINEERING CO., LTD.
1213/430 Soi Ladprao94 (Panjamit) Plubpla, Wang Thonglang,
Bangkok, Thailand. 10310
E APISAK@ACCO.CO.TH W ACCO@ACCO.CO.TH
T 66(2) 559 0177-9, F 66 (2) 559 0176

PERSPECTIVE
MEETING ROOM 16 PAX.


STATUS FOR TENDER

JOB NO. PTD 20.001	DRAWING NUMBER D-010	REVISION T1
------------------------------	--------------------------------	-----------------------



© LUX89 CO., LTD. April 2020

REFERENCE MAP		NORTH	
NOTES 1. DO NOT SCALE DRAWINGS. WRITTEN DIMENSIONS GOVERN. 2. ALL DIMENSIONS ARE IN MILLIMETERS UNLESS NOTED OTHERWISE. 3. ALL DIMENSIONS SHALL BE VERIFIED ON SITE BEFORE PROCEEDING WITH THE WORK. LUX89 SHALL BE NOTIFIED IN WRITING OF ANY DISCREPANCIES. 4. THIS DRAWING MUST BE READ IN CONJUNCTION WITH ALL RELEVANT CONTRACTS, SPECIFICATIONS, REPORTS AND DRAWINGS.	
(C) 2020 COPYRIGHT OF THIS DRAWING IS VESTED IN LUX89 CO., LTD.	
THIS DRAWING IS AN UNCONTROLLED COPY. UNLESS NOTED OTHERWISE	
<table border="1"><tr><td></td><td></td><td></td><td></td></tr><tr><td></td><td></td><td></td><td></td></tr><tr><td></td><td></td><td></td><td></td></tr><tr><td></td><td></td><td></td><td></td></tr><tr><td></td><td></td><td></td><td></td></tr><tr><td></td><td></td><td></td><td></td></tr><tr><td></td><td></td><td></td><td></td></tr><tr><td></td><td></td><td></td><td></td></tr><tr><td></td><td></td><td></td><td></td></tr><tr><td></td><td></td><td></td><td></td></tr><tr><td></td><td></td><td></td><td></td></tr><tr><td></td><td></td><td></td><td></td></tr><tr><td></td><td></td><td></td><td></td></tr><tr><td></td><td></td><td></td><td></td></tr><tr><td></td><td></td><td></td><td></td></tr><tr><td></td><td></td><td></td><td></td></tr><tr><td></td><td></td><td></td><td></td></tr><tr><td></td><td></td><td></td><td></td></tr><tr><td>T1</td><td>CP</td><td>FOR TENDER</td><td>10/04/2020</td></tr><tr><td>REV</td><td>BY</td><td>DESCRIPTION</td><td>DATE</td></tr></table>	T1	CP	FOR TENDER	10/04/2020	REV	BY	DESCRIPTION	DATE
T1	CP	FOR TENDER	10/04/2020	
REV	BY	DESCRIPTION	DATE	
CLIENT / PROJECT	
LUX 89 Tilleke & Gibbins Myanmar Limited.	
PROJECT MANAGER & INTERIOR DESIGNER	
LUX 89 CO., LTD. 7/89 Soi Rama 2 Soi 54/4,Samae Dam, Bang Khun Thian, Bangkok , Thailand10150 E LUX89.BKK@GMAIL.COM W LUX89.COM T 66(2) 416 9189	
ARCHITECTURE	
STRUCTURE ENGINEER	
M&E ENGINEER	
ACCO ENGINEERING CO., LTD. 1213/430 Soi Ladprao94 (Panjarnit) Plubpla, Wang Thonglang, Bangkok, Thailand. 10310 E APISAK@ACCO.CO.TH W ACCO@ACCO.CO.TH T 66(2) 559 0177-9, F 66 (2) 559 0176	
DRAWING	
PERSPECTIVE GENERAL WORK STATION & PANTRY	
STATUS	
FOR TENDER	
SCALE AT A1/A3	DRAWN	CHECKED	FLUOTATE	
	AK	CP	10/04/2020	
JOB NO.	DRAWING NUMBER	REVISION	
PTD 20.001	D-011	T1	

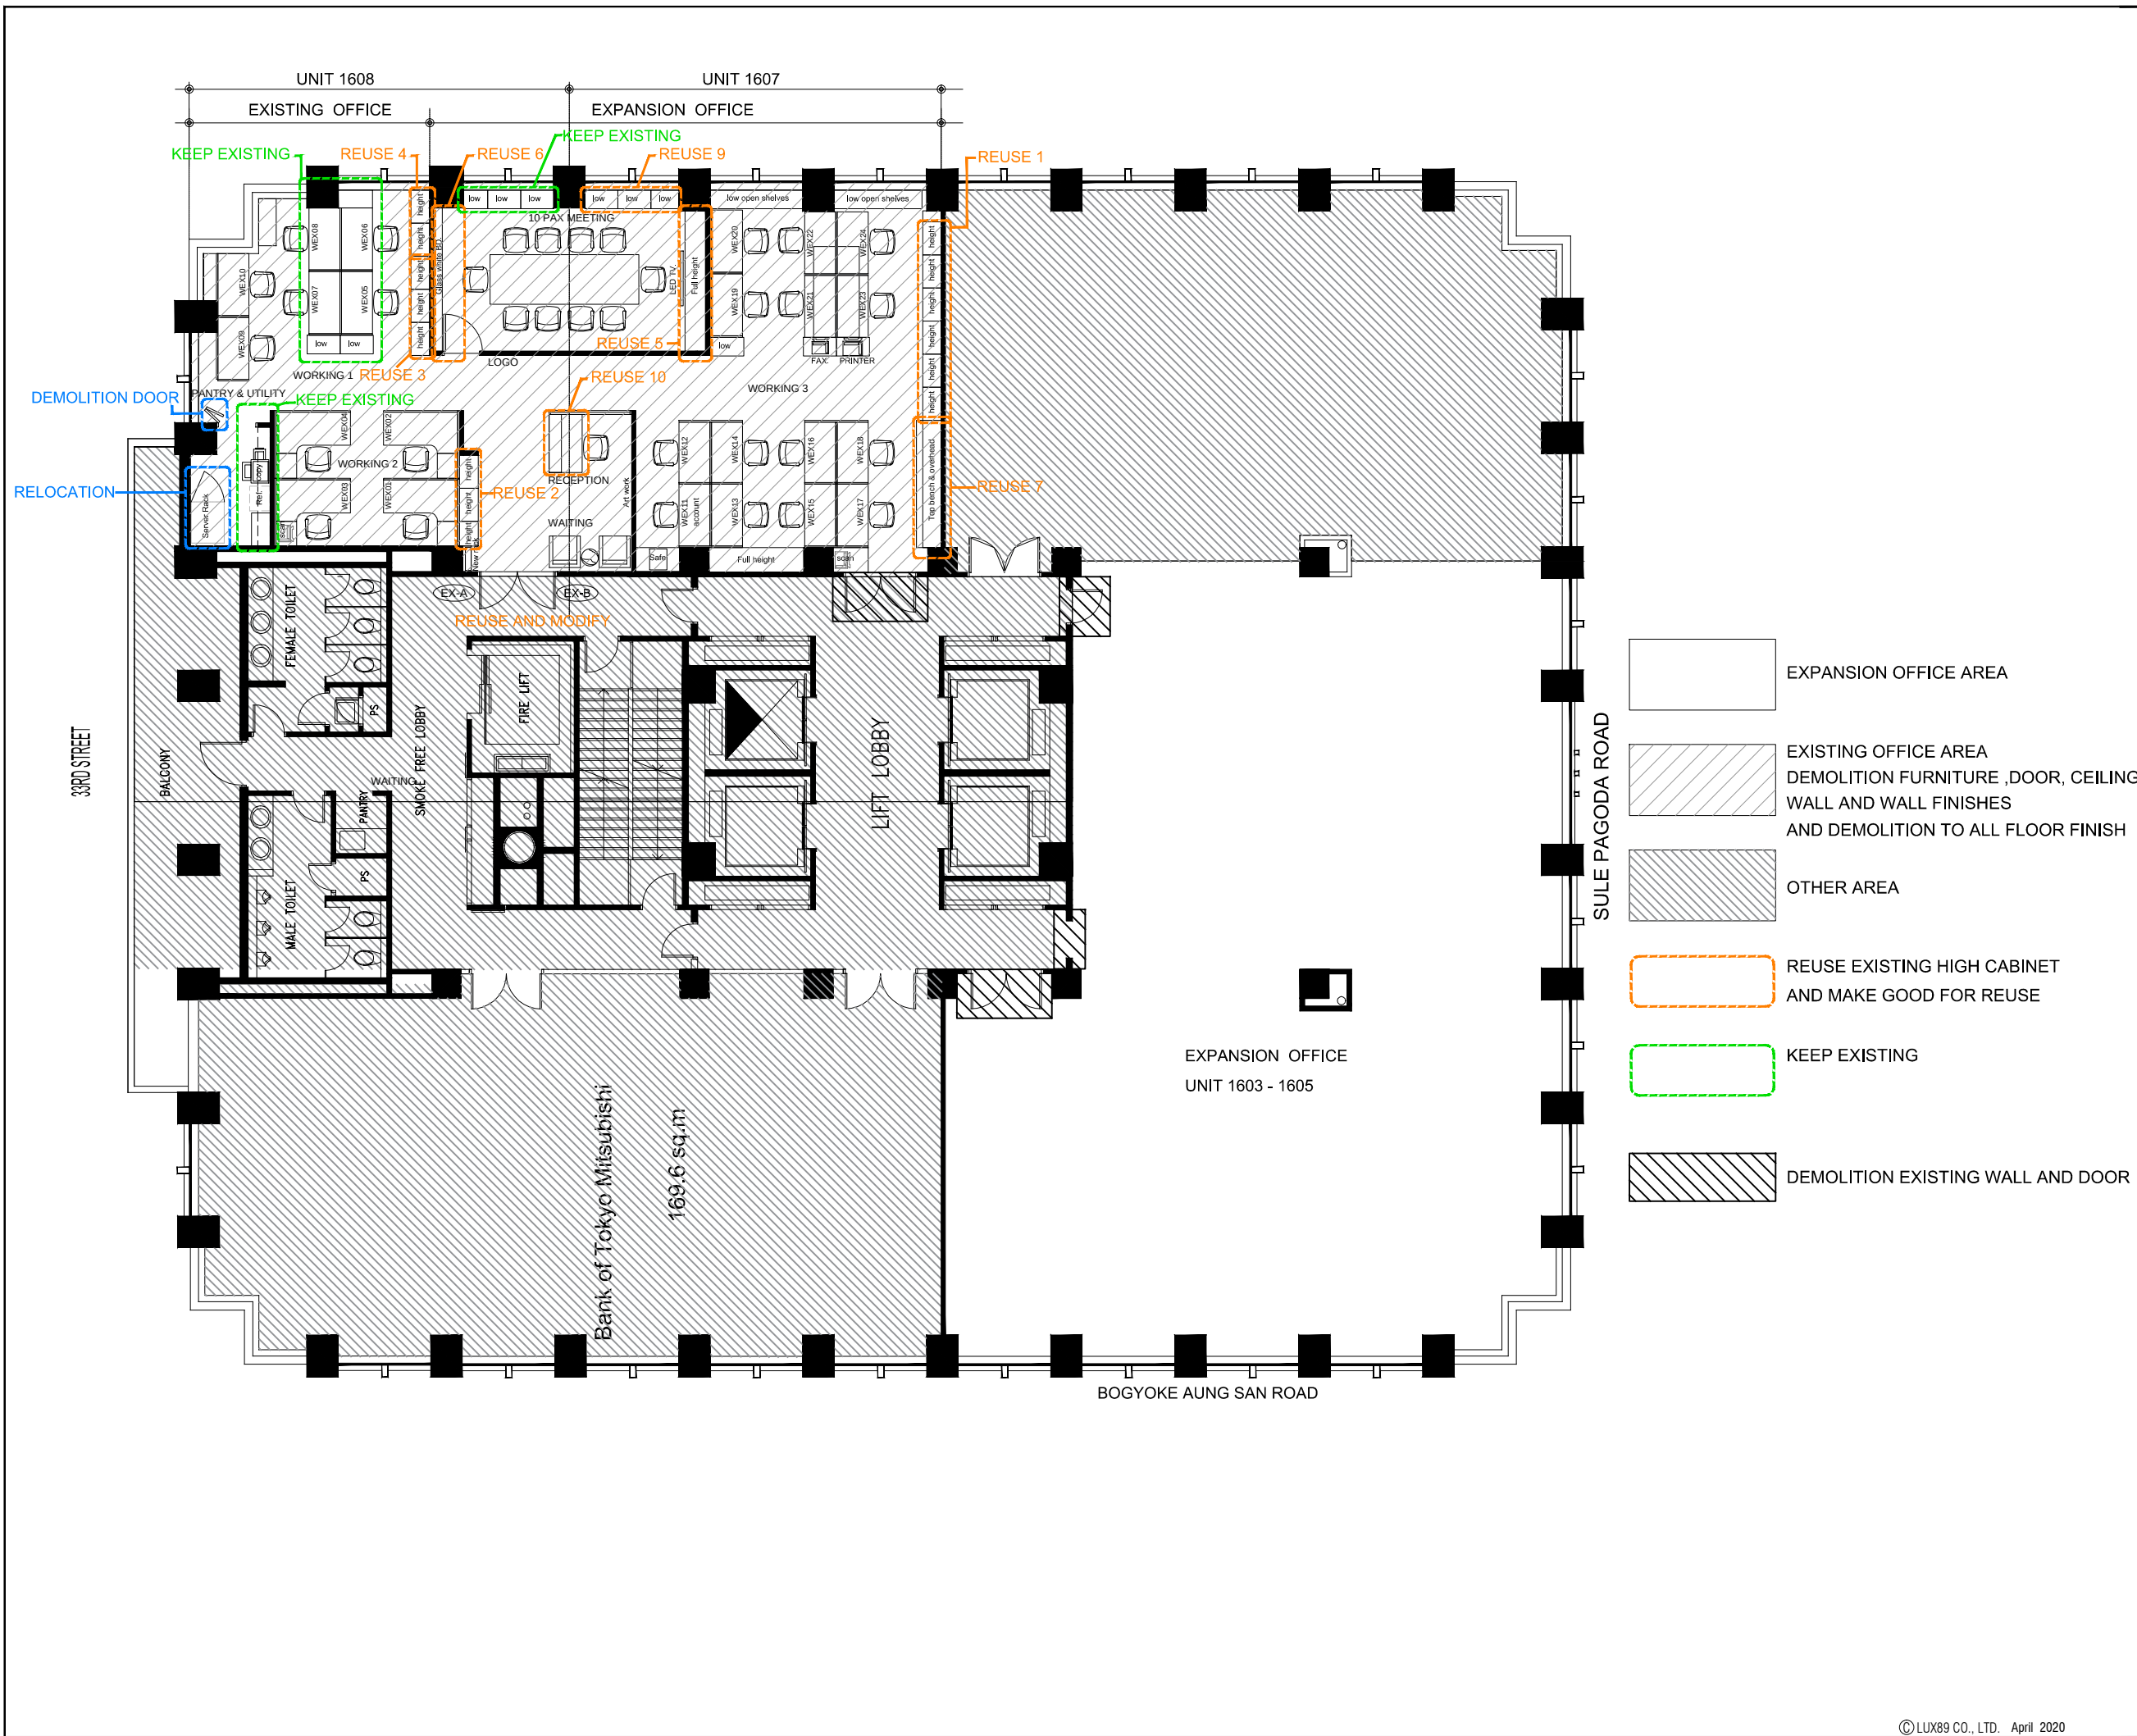

REFERENCE MAP

NORTH

NOTES

1. DO NOT SCALE DRAWINGS. WRITTEN DIMENSIONS GOVERN.
2. ALL DIMENSIONS ARE IN MILLIMETERS UNLESS NOTED OTHERWISE.
3. ALL DIMENSIONS SHALL BE VERIFIED ON SITE BEFORE PROCEEDING WITH THE WORK. LUX89 SHALL BE NOTIFIED IN WRITING OF ANY DISCREPANCIES.
4. THIS DRAWING MUST BE READ IN CONJUNCTION WITH ALL RELEVANT CONTRACTS, SPECIFICATIONS, REPORTS AND DRAWINGS.

© 2020 COPYRIGHT OF THIS DRAWING IS VESTED IN LUX89 CO., LTD.

THIS DRAWING IS AN UNCONTROLLED COPY, UNLESS NOTED OTHERWISE

T1	CP	FOR TENDER	10/04/2020
REV	BY	DESCRIPTION	DATE

CLIENT / PROJECT

**Tilleke & Gibbins
Myanmar Limited.**

PROJECT MANAGER & INTERIOR DESIGNER

LUX 89 CO., LTD.
7/89 Soi Rama 2 Soi 54/4 Samae Dam,
Bang Khun Thian, Bangkok, Thailand 10150
E LUX89.BKK@GMAIL.COM W LUX89.COM
T 66(2) 416 9189

ARCHITECTURE

STRUCTURE ENGINEER

M&E ENGINEER

ACCO ENGINEERING CO., LTD.
1213/430 Soi Ladprao94 (Panjamit) Plubpla, Wang Thonglang,
Bangkok, Thailand. 10310
E APISAK@ACCO.CO.TH W ACCO@ACCO.CO.TH
T 66(2) 559 0177-9, F 66 (2) 559 0176


DRAWING

EXISTING & DEMOLITION PLAN

STATUS

FOR TENDER

SCALE AT A3	DRAWN	CO-ORDINATED	CHECKED	PLUTDATE
1:150	AK	CP	CP	10/04/2020
JOB NO.	DRAWING NUMBER	REVISION		
PTD 20.001	D-101	T1		

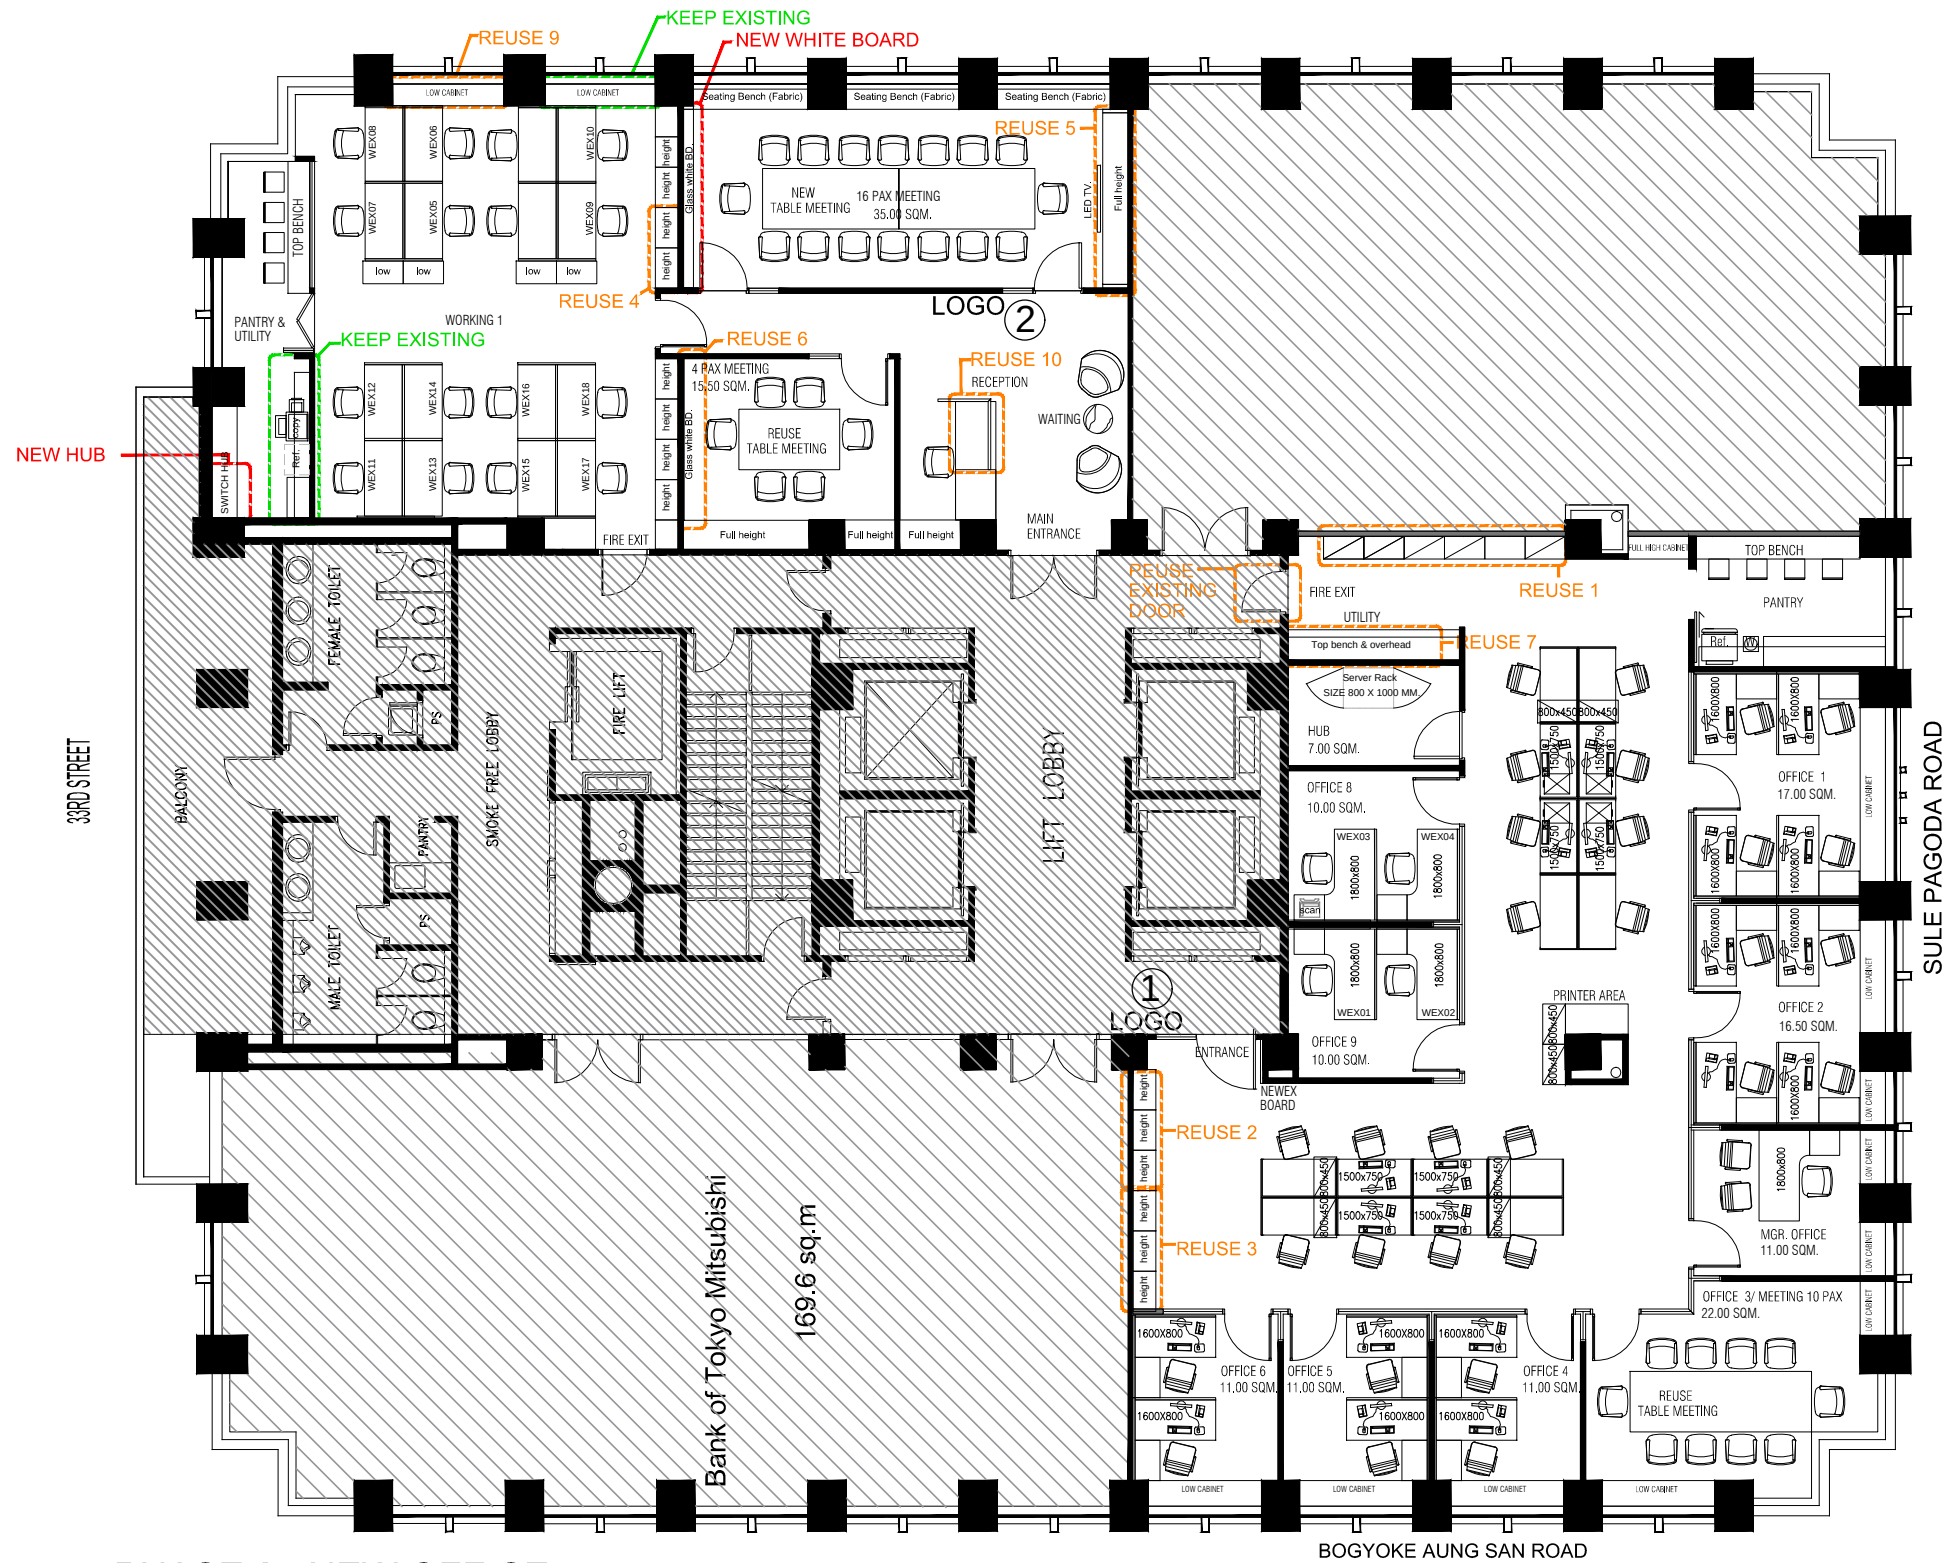

PHASE 2 : NEW OFFICE

RECEPTION	23.00 sqm.	STAFF WORKSTATION 1500x750 = 16 PAX
MEETING ROOM1 # 16 PAX	35.00 sqm.	UTILITY & PANTRY 10.00 sqm.
MEETING ROOM 2 # 4 PAX	15.50 sqm.	HUB 2.00 sqm.

PHASE 1 : NEW OFFICE

CLOSE OFFICE		
MANAGER 1 ROOM	11.00 sqm.	STAFF
OFFICE 2 PAX #5 ROOMS	10.00 -11.00 sqm.	WORKSTATION 1500x750 = 8 PAX
OFFICE 4 PAX #2 ROOMS	16.50 - 17.00 sqm.	PANTRY AREA 10.00 sqm.
MEETINGROOM 10 PAX # 1 ROOM	22.00 sqm.	HUB ROOM 7 sqm.

REFERENCE MAP

NORTH

NOTES

1. DO NOT SCALE DRAWINGS. WRITTEN DIMENSIONS GOVERN.

2. ALL DIMENSIONS ARE IN MILLIMETERS UNLESS NOTED OTHERWISE.

3. ALL DIMENSIONS SHALL BE VERIFIED ON SITE BEFORE PROCEEDING WITH THE WORK. LUX89 SHALL BE NOTIFIED IN WRITING OF ANY DISCREPANCIES.

4. THIS DRAWING MUST BE READ IN CONJUNCTION WITH ALL RELEVANT CONTRACTS, SPECIFICATIONS, REPORTS AND DRAWINGS.

© 2020 COPYRIGHT OF THIS DRAWING IS VESTED IN LUX89 CO., LTD.

THIS DRAWING IS AN UNCONTROLLED COPY, UNLESS NOTED OTHERWISE

T1	CP	FOR TENDER	10/04/2020
REV	BY	DESCRIPTION	DATE

CLIENT / PROJECT

Tilleke & Gibbins
Myanmar Limited.

PROJECT MANAGER & INTERIOR DESIGNER

LUX 89 CO., LTD.
7/89 Soi Rama 2 Soi 54/4 Samae Dam,
Bang Khun Thian, Bangkok, Thailand 10150
E LUX89.BKK@GMAIL.COM W LUX89.COM
T 66(2) 416 9189

ARCHITECTURE

STRUCTURE ENGINEER

M&E ENGINEER

ACCO ENGINEERING CO., LTD.
1213/430 Soi Ladprao94 (Panjarnit) Plubpla, Wang Thonglang,
Bangkok, Thailand. 10310
E APISAK@ACCO.CO.TH W ACCO@ACCO.CO.TH
T 66(2) 559 0177-9, F 66 (2) 559 0176


DRAWING

LAY-OUT PLAN

STATUS

FOR TENDER

SCALE AT A3	DRAWN	CORRECTED	CHECKED	PLUTDATE
1:150	AK	CP	CP	10/04/2020
JOB NO.	DRAWING NUMBER	REVISION		
PTD 20.001	D-102	T1		

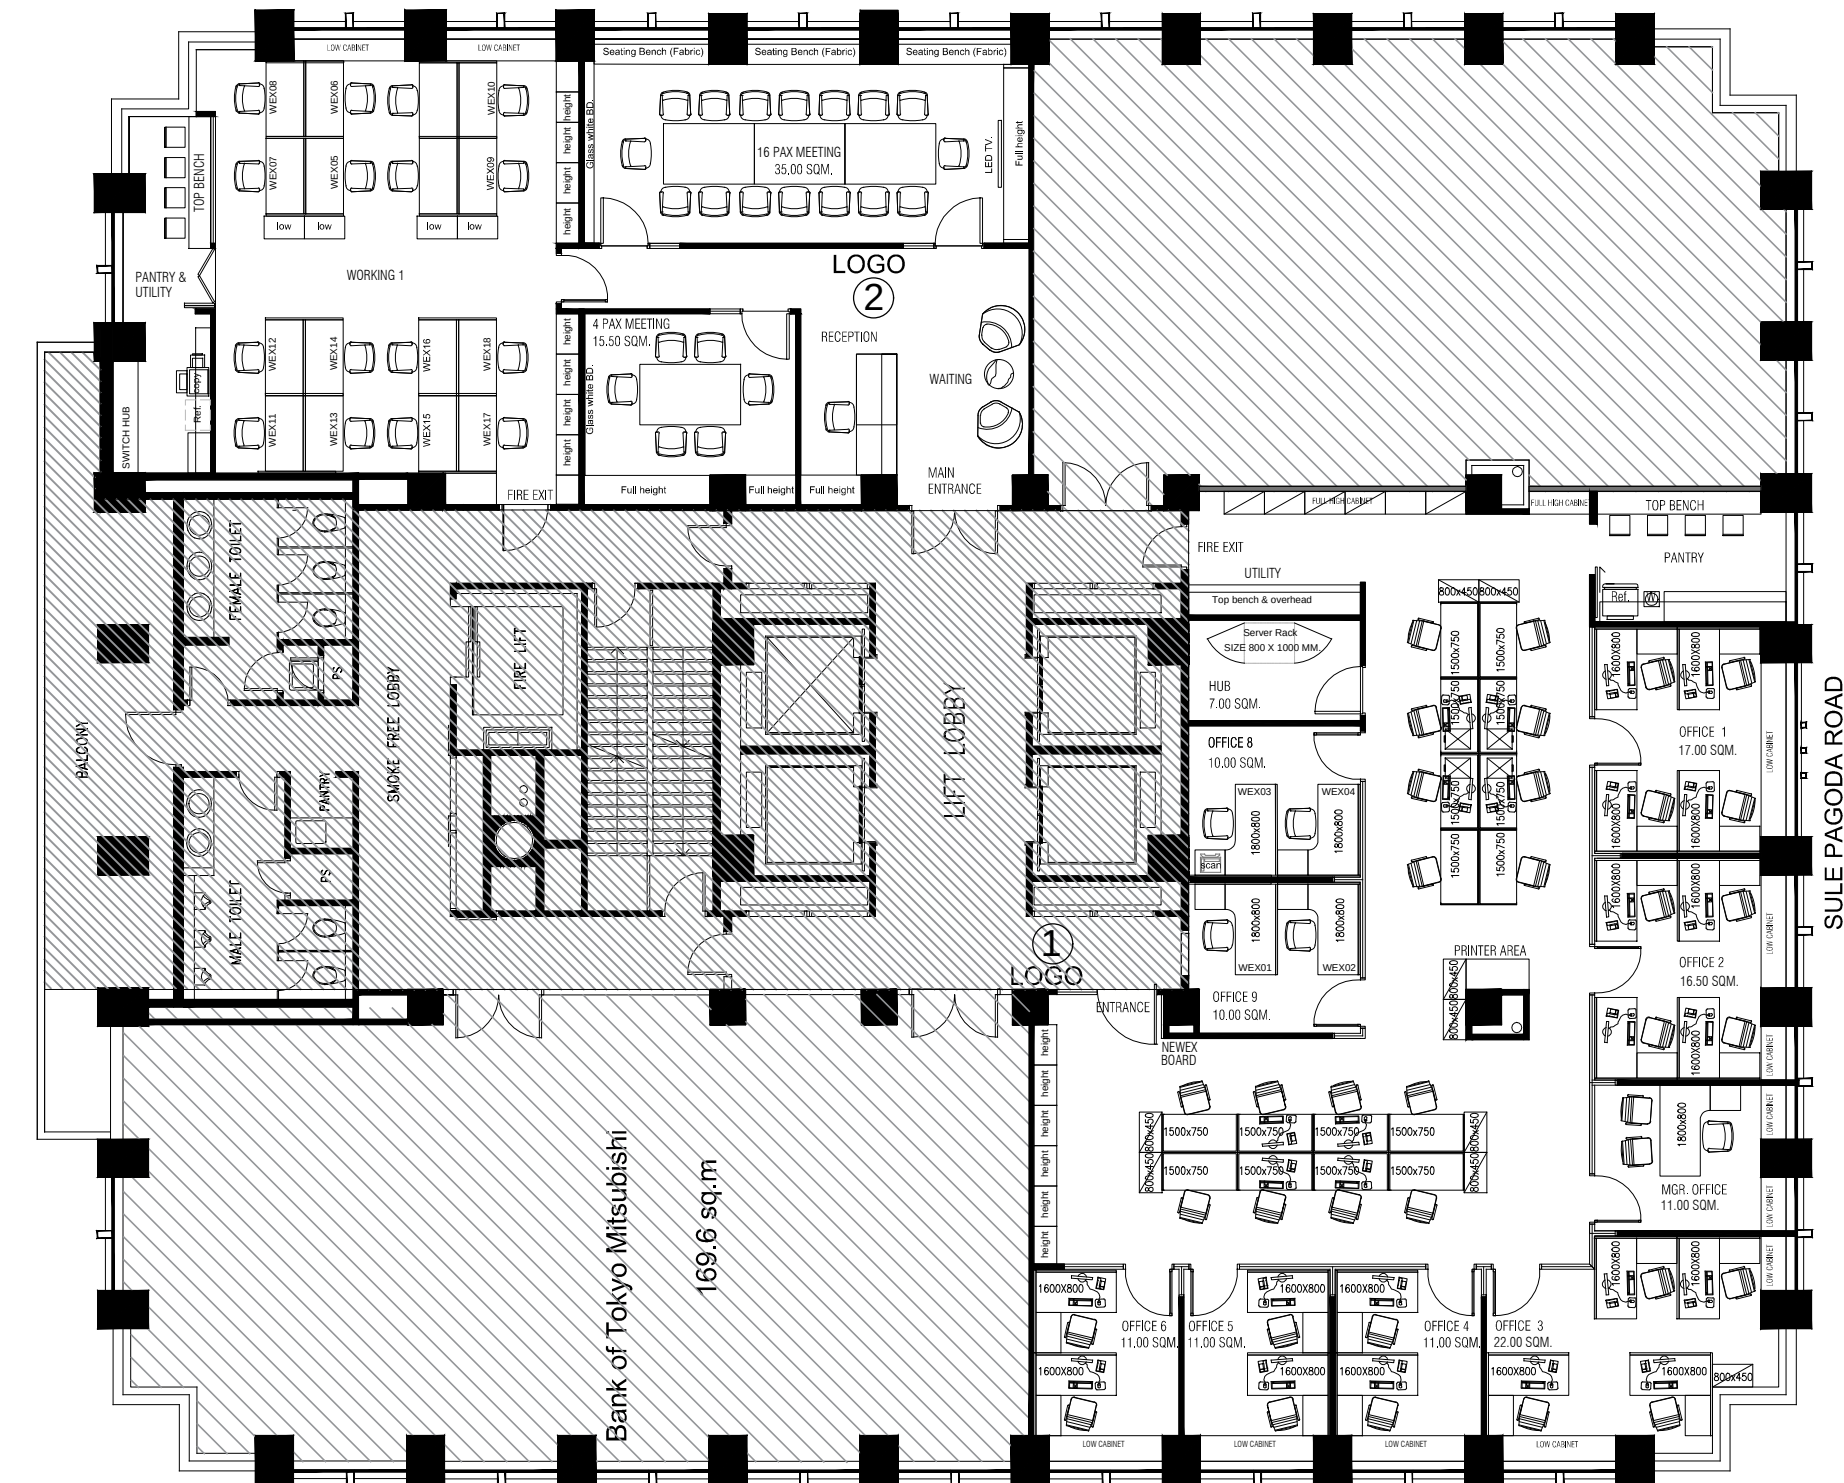

PHASE 2 : NEW OFFICE

RECEPTION	23.00 sqm.	STAFF WORKSTATION 1500x750	= 16 PAX
MEETING ROOM1 #16 PAX	35.00 sqm.	UTILITY & PANTRY	10.00 sqm.
MEETING ROOM 2 # 4 PAX	15.50 sqm.	HUB	2.00 sqm.

PHASE 3 : FUTURE

CLOSE OFFICE		STAFF	
MANAGER 1 ROOM	11.00 sqm.	WORKSTATION 1500x750	= 16 PAX
OFFICE 2 PAX #5 ROOMS	10.00-11.00 sqm.	PANTRY AREA	10.00 sqm.
OFFICE 4 PAX #3 ROOMS	16.50 & 22.00 sqm.	HUB ROOM	7 sqm.

REFERENCE MAP

NORTH

NOTES

1. DO NOT SCALE DRAWINGS. WRITTEN DIMENSIONS GOVERN.
2. ALL DIMENSIONS ARE IN MILLIMETERS UNLESS NOTED OTHERWISE.
3. ALL DIMENSIONS SHALL BE VERIFIED ON SITE BEFORE PROCEEDING WITH THE WORK. LUX89 SHALL BE NOTIFIED IN WRITING OF ANY DISCREPANCIES.
4. THIS DRAWING MUST BE READ IN CONJUNCTION WITH ALL RELEVANT CONTRACTS, SPECIFICATIONS, REPORTS AND DRAWINGS.

© 2020 COPYRIGHT OF THIS DRAWING IS VESTED IN LUX89 CO., LTD.

THIS DRAWING IS AN UNCONTROLLED COPY, UNLESS NOTED OTHERWISE

T1	CP	FOR TENDER	10/04/2020
REV	BY	DESCRIPTION	DATE

CLIENT / PROJECT

Tilleke & Gibbins
Myanmar Limited.

PROJECT MANAGER & INTERIOR DESIGNER

LUX 89 CO., LTD.
7/89 Soi Rama 2 Soi 54/4 Samae Dam,
Bang Khun Thian, Bangkok, Thailand 10150
E LUX89.BKK@GMAIL.COM W LUX89.COM
T 66(2) 416 9189

ARCHITECTURE

STRUCTURE ENGINEER

M&E ENGINEER

ACC0 ENGINEERING CO., LTD.
1213/430 Soi Ladprao94 (Panjarnit) Plubpla, Wang Thonglang,
Bangkok, Thailand. 10310
E APISAK@ACC0.CO.TH W ACC0@ACC0.CO.TH
T 66(2) 559 0177-9, F 66 (2) 559 0176


DRAWING

LAY-OUT PLAN

STATUS

FOR TENDER

SCALE AT A3	DRAWN	CO-DRAWN	CO-EDITED	PLUTDATE
1 :150	AK	CP	CP	10/04/2020
JOB NO.	DRAWING NUMBER	REVISION		
PTD 20.001	D-103	T1		

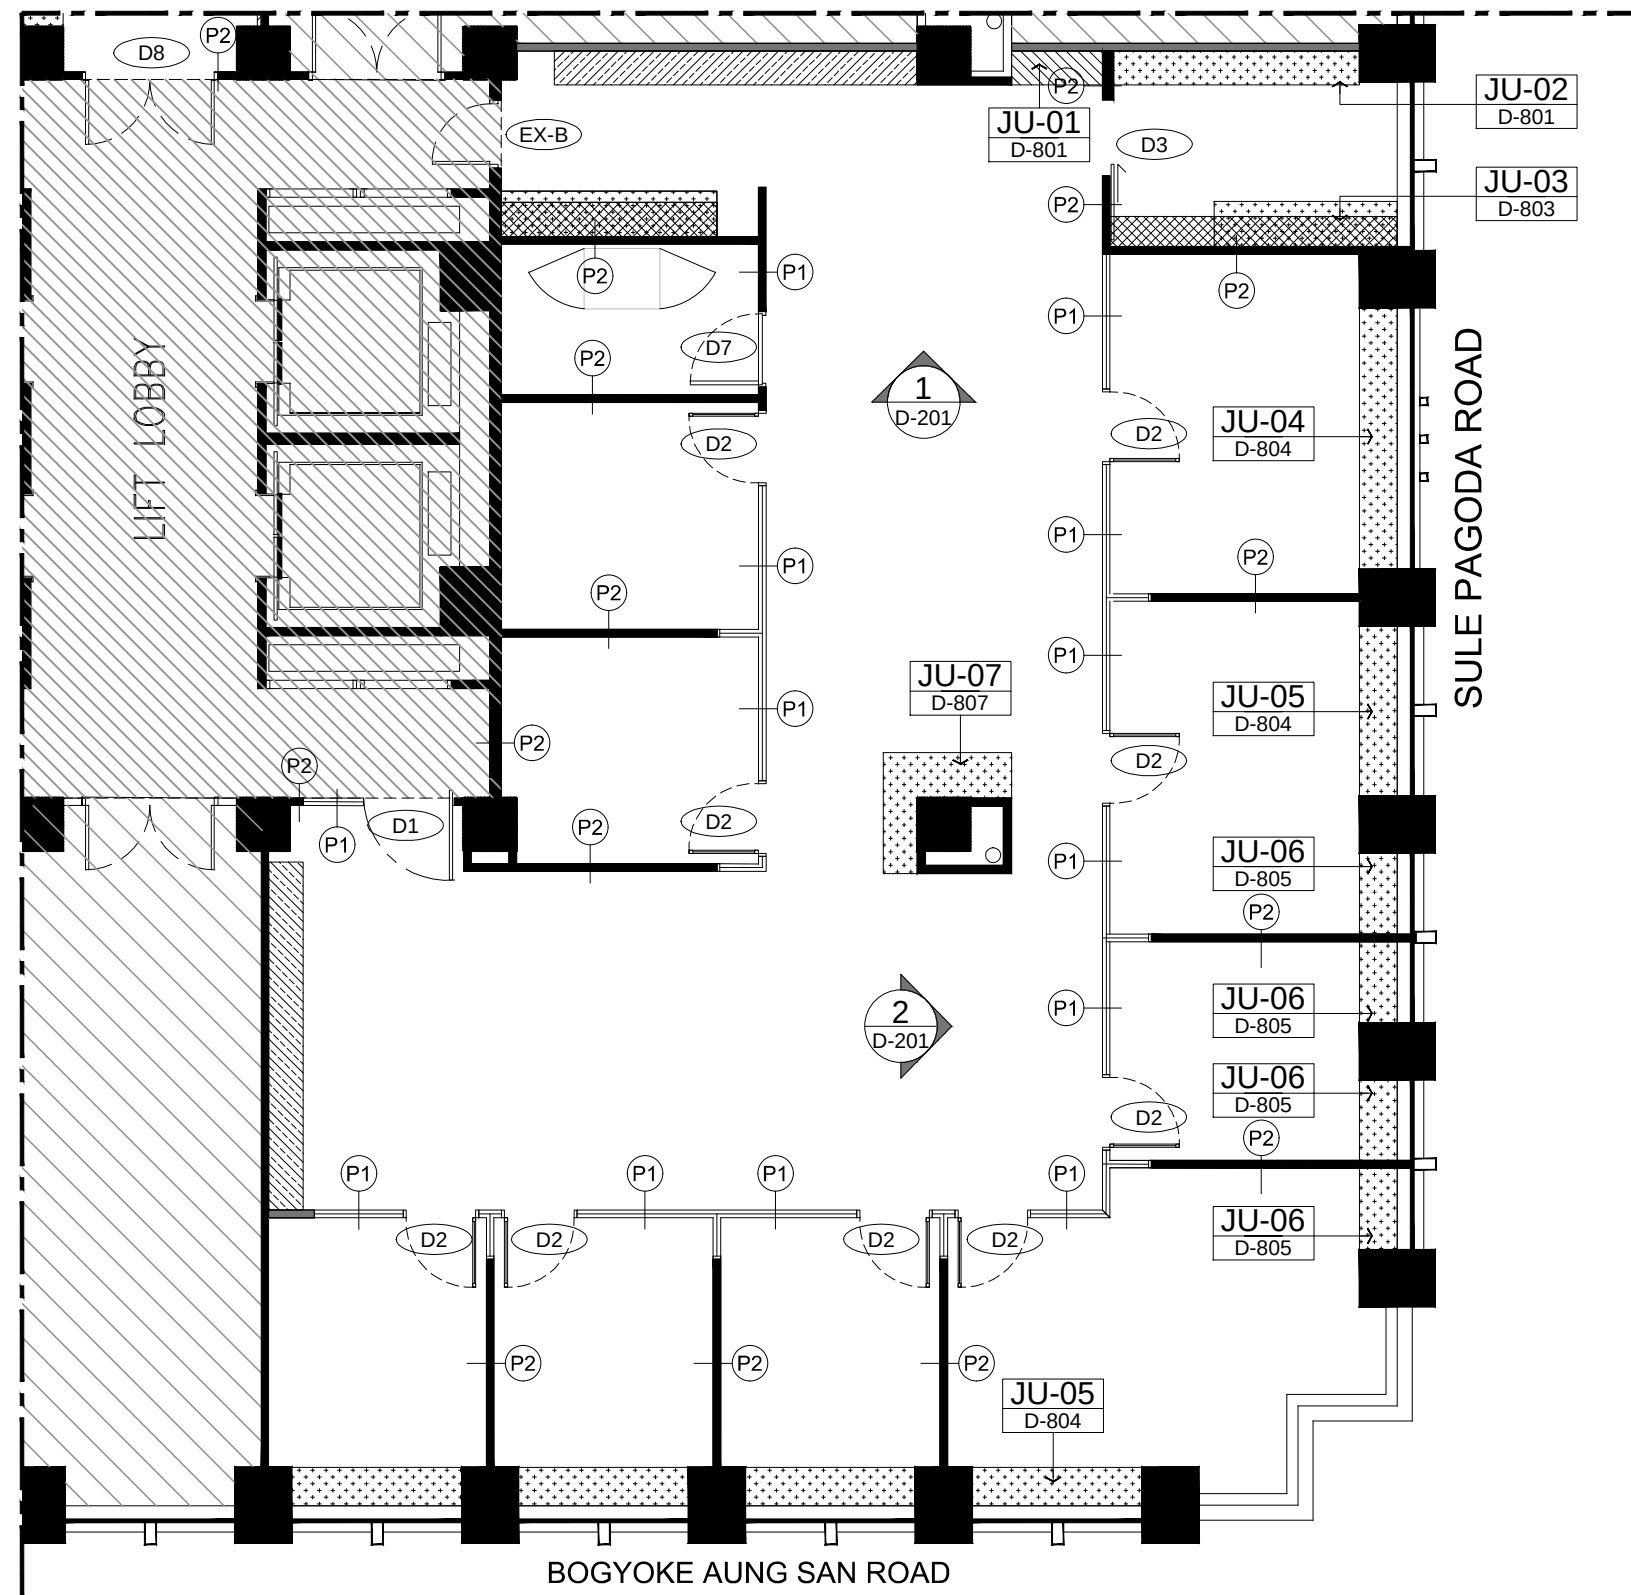

PHASE 1 : NEW OFFICE

CLOSE OFFICE

MANAGER	1 ROOM	11.00 sqm.
OFFICE 2 PAX #5 ROOMS		10.00 -11.00 sqm.
OFFICE 4 PAX #2 ROOMS		16.50 - 17.00 sqm.
MEETINGROOM 10 PAX # 1 ROOM		22.00 sqm.

STAFF	
WORKSTATION 1500x750	= 8 PAX
PANTRY AREA	10.00 sqm.
HUB ROOM	7 sqm.

DETAIL MARK LEGEND:

	DOOR TYPE
	ELEVATION NO.
	REFERENCE DWG NO.

DOOR LEGEND

	EXISTING DOOR
--	---------------

PARTITION LEGEND

	EXISTING PARTITION
	FULL HEIGHT 10mm. THK. CLEAR LAMINATED GLASS PARTITION TO UNDERSIDE OF SUSPENDED CEILING
	FULL HEIGHT DRYWALL PARTITION TO UNDER SIDE OF CEILING WITH SINGLE SHEET OF GYPSUM PLASTERBOARD TO BOTH SIDES
	FULL HEIGHT DRYWALL PARTITION TO UNDER SIDE OF CEILING WITH SINGLE SHEET OF GYPSUM PLASTERBOARD TO BOTH SIDES WITH CLEAR GLASS VISION
	FULL HEIGHT DRYWALL PARTITION TO UNDER SIDE OF CEILING WITH SINGLE SHEET OF GYPSUM PLASTERBOARD TO BOTH SIDES WITH CLEAR GLASS VISION

NOTE

- UNLESS OTHERWISE NOTED ALL SKIRTING TO BE 100MM. SILVER ALUMINUM.
- APPLY P1 TO ALL GYPSUM BOARD DRYWALL & COLUMN UNDER PERIMETER WINDOW THROUGHOUT , UNLESS SPECIFIED OTHERWISE
- CONTRACTOR TO CLOSE UP THE BRICK WALL ABOVE AHU ROOM WHERE IS NOT REQUIRED FOR RETURN A/C DUCT
- SKIRTING JOINTS TO ALIGN WITH JOINERY OR FINISHING JOINTS.
- ALL PARTITIONS SHOWN TO BE CENTRED ON CEILING GRID TAKE PRECEDENCE OVER DIMENSIONS. CONFIRM CONFLICTS WITH ID
- REFER TO D-150 FOR DETAILS OF WALL FINISHES. FOR EXPOSED SLAB CEILING AREAS ALLOW FOR PLASTERBOARD TO UNDER SIDE OF SLAB TO TOP OF THE ADJACENT PARTITION TYPE. THIS IS NOT SPECIFIC TO ANY PARTITION TYPE, TYPES WILL VARY, CONTRACTOR TO CO-ORDINATE.
- GLAZED PARTITION / SKIRTING SUPPLIERS AS SPECIFICATION, ALL GLASS PARTITION TO BE G1 THROUGH OUT UNLESS SPECIFIED OTHERWISE
- PARTITION DETAILS REFER D-300 , DOOR DETAILS REFER D-400

FURNITURE LEGEND

	BUILT-IN FURNITURE ITEM, FULL HEIGHT
	BUILT-IN FURNITURE ITEM, HANGING CABINET
	BUILT-IN FURNITURE ITEM, NOT FULL HEIGHT
	EXISTING FURNITURE

REFERENCE MAP

NORTH

NOTES

1. DO NOT SCALE DRAWINGS. WRITTEN DIMENSIONS GOVERN.


2. ALL DIMENSIONS ARE IN MILLIMETERS UNLESS NOTED OTHERWISE.

3. ALL DIMENSIONS SHALL BE VERIFIED ON SITE BEFORE PROCEEDING WITH THE WORK. LUX89 SHALL BE NOTIFIED IN WRITING OF ANY DISCREPANCIES.

4. THIS DRAWING MUST BE READ IN CONJUNCTION WITH ALL RELEVANT CONTRACTS, SPECIFICATIONS, REPORTS AND DRAWINGS.

© 2020 COPYRIGHT OF THIS DRAWING IS VESTED IN LUX89 CO., LTD.

THIS DRAWING IS AN UNCONTROLLED COPY, UNLESS NOTED OTHERWISE

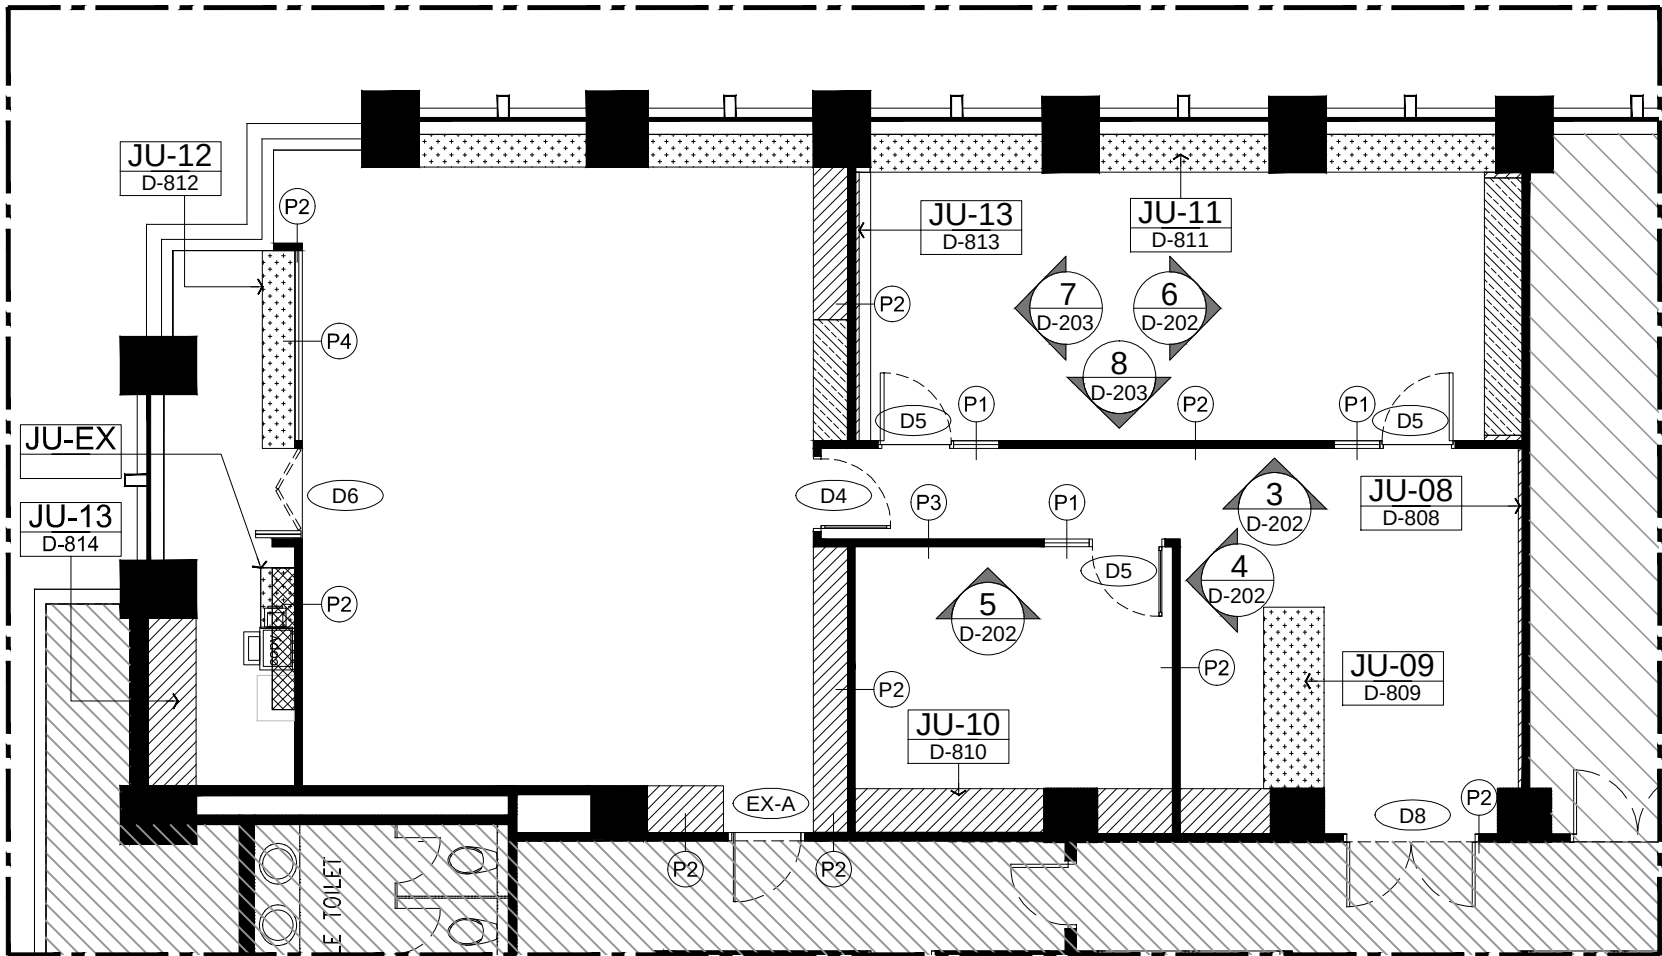

PHASE 2 : NEW OFFICE

RECEPTION	23.00 sqm.	STAFF WORKSTATION 1500x750 = 16 PAX
MEETING ROOM1 #16 PAX	35.00 sqm.	UTILITY & PANTRY 10.00 sqm.
MEETING ROOM 2 # 4 PAX	15.50 sqm.	HUB 2.00 sqm.

DETAIL MARK LEGEND:

- DOOR TYPE
ELEVATION NO.
REFERENCE DWG NO.

FURNITURE LEGEND

- BUILT-IN FURNITURE ITEM, FULL HEIGHT
BUILT-IN FURNITURE ITEM, HANGING CABINET
BUILT-IN FURNITURE ITEM, NOT FULL HEIGHT
EXISTING FURNITURE

DOOR LEGEND

- EXISTING DOOR

PARTITION LEGEND

- EXISTING PARTITION
FULL HEIGHT 10mm. THK. CLEAR LAMINATED GLASS PARTITION TO UNDERSIDE OF SUSPENDED CEILING
FULL HEIGHT DRYWALL PARTITION TO UNDER SIDE OF CEILING WITH SINGLE SHEET OF GYPSUM PLASTERBOARD TO BOTH SIDES
FULL HEIGHT DRYWALL PARTITION TO UNDER SIDE OF CEILING WITH SINGLE SHEET OF GYPSUM PLASTERBOARD TO BOTH SIDES WITH CLEAR GLASS VISION
FULL HEIGHT DRYWALL PARTITION TO UNDER SIDE OF CEILING WITH SINGLE SHEET OF GYPSUM PLASTERBOARD TO BOTH SIDES WITH CLEAR GLASS VISION

NOTE

1. UNLESS OTHERWISE NOTED ALL SKIRTING TO BE 100MM. SILVER ALUMINUM.
2. APPLY P1 TO ALL GUPSUM BOARD DRYWALL & COLUMN UNDER PERIMETER WINDOW THOUGHOUT , UNLESS SPECIFIED OTHERWISE
3. CONTRACTOR TO CLOSE UP THE BRICK WALL ABOVE AHU ROOM WHERE IS NOT REQUIRED FOR RETURN A/C DUCT
4. SKIRTING JOINTS TO ALIGN WITH JOINERY OR FINISHING JOINTS.
5. ALL PARTITIONS SHOWN TO BE CENTRED ON CEILING GRID TAKE PRECEDENCE OVER DIMENSIONS. CONFIRM CONFLICTS WITH ID
6. REFER TO D-150 FOR DETAILS OF WALL FINISHES. FOR EXPOSED SLAB CEILING AREAS ALLOW FOR PLASTERBOARD TO UNDER SIDE OF SLAB TO TOP OF THE ADJACENT PARTITION TYPE. THIS IS NOT SPECIFIC TO ANY PARTITION TYPE, TYPES WILL VARY, CONTRACTOR TO CO-ORDINATE.
7. GLAZED PARTITION / SKIRTING SUPPLIERS AS SPECIFICATION, ALL GLASS PARTITION TO BE G1 THOUGH OUT UNLESS SPECIFIED OTHERWISE
8. PARTITION DETAILS REFER D-300 , DOOR DETAILS REFER D-400

REFERENCE MAP

NORTH

NOTES

1. DO NOT SCALE DRAWINGS. WRITTEN DIMENSIONS GOVERN.
2. ALL DIMENSIONS ARE IN MILLIMETERS UNLESS NOTED OTHERWISE.
3. ALL DIMENSIONS SHALL BE VERIFIED ON SITE BEFORE PROCEEDING WITH THE WORK. LUX89 SHALL BE NOTIFIED IN WRITING OF ANY DISCREPANCIES.
4. THIS DRAWING MUST BE READ IN CONJUNCTION WITH ALL RELEVANT CONTRACTS, SPECIFICATIONS, REPORTS AND DRAWINGS.

© 2020 COPYRIGHT OF THIS DRAWING IS VESTED IN LUX89 CO., LTD.

THIS DRAWING IS AN UNCONTROLLED COPY, UNLESS NOTED OTHERWISE

T1	CP	FOR TENDER	10/04/2020
REV	BY	DESCRIPTION	DATE

CLIENT / PROJECT

**Tilleke & Gibbins
Myanmar Limited.**

PROJECT MANAGER & INTERIOR DESIGNER

LUX 89 CO., LTD.
7/89 Soi Rama 2 Soi 54/4 Samae Dam,
Bang Khun Thian, Bangkok, Thailand 10150
E LUX89.BKK@GMAIL.COM W LUX89.COM
T 66(2) 416 9189

ARCHITECTURE

STRUCTURE ENGINEER

M&E ENGINEER

ACCO ENGINEERING CO., LTD.
1213/430 Soi Ladprao94 (Panjarnit) Plubpla, Wang Thonglang,
Bangkok, Thailand. 10310
E APISAK@ACCO.CO.TH W ACCO@ACCO.CO.TH
T 66(2) 559 0177-9, F 66 (2) 559 0176

DRAWING


**PARTITION & DOOR PLAN
PHASE 2**

STATUS

FOR TENDER

SCALE AT A1/A3	DRAWN	CO-ORDINATED	CHECKED	PLOTTED
1:100	AK	CP	CP	10/04/2020
JOB NO.	DRAWING NUMBER	REVISION		
PTD 20.001	D-108	T1		

© LUX89 CO., LTD. April 2020

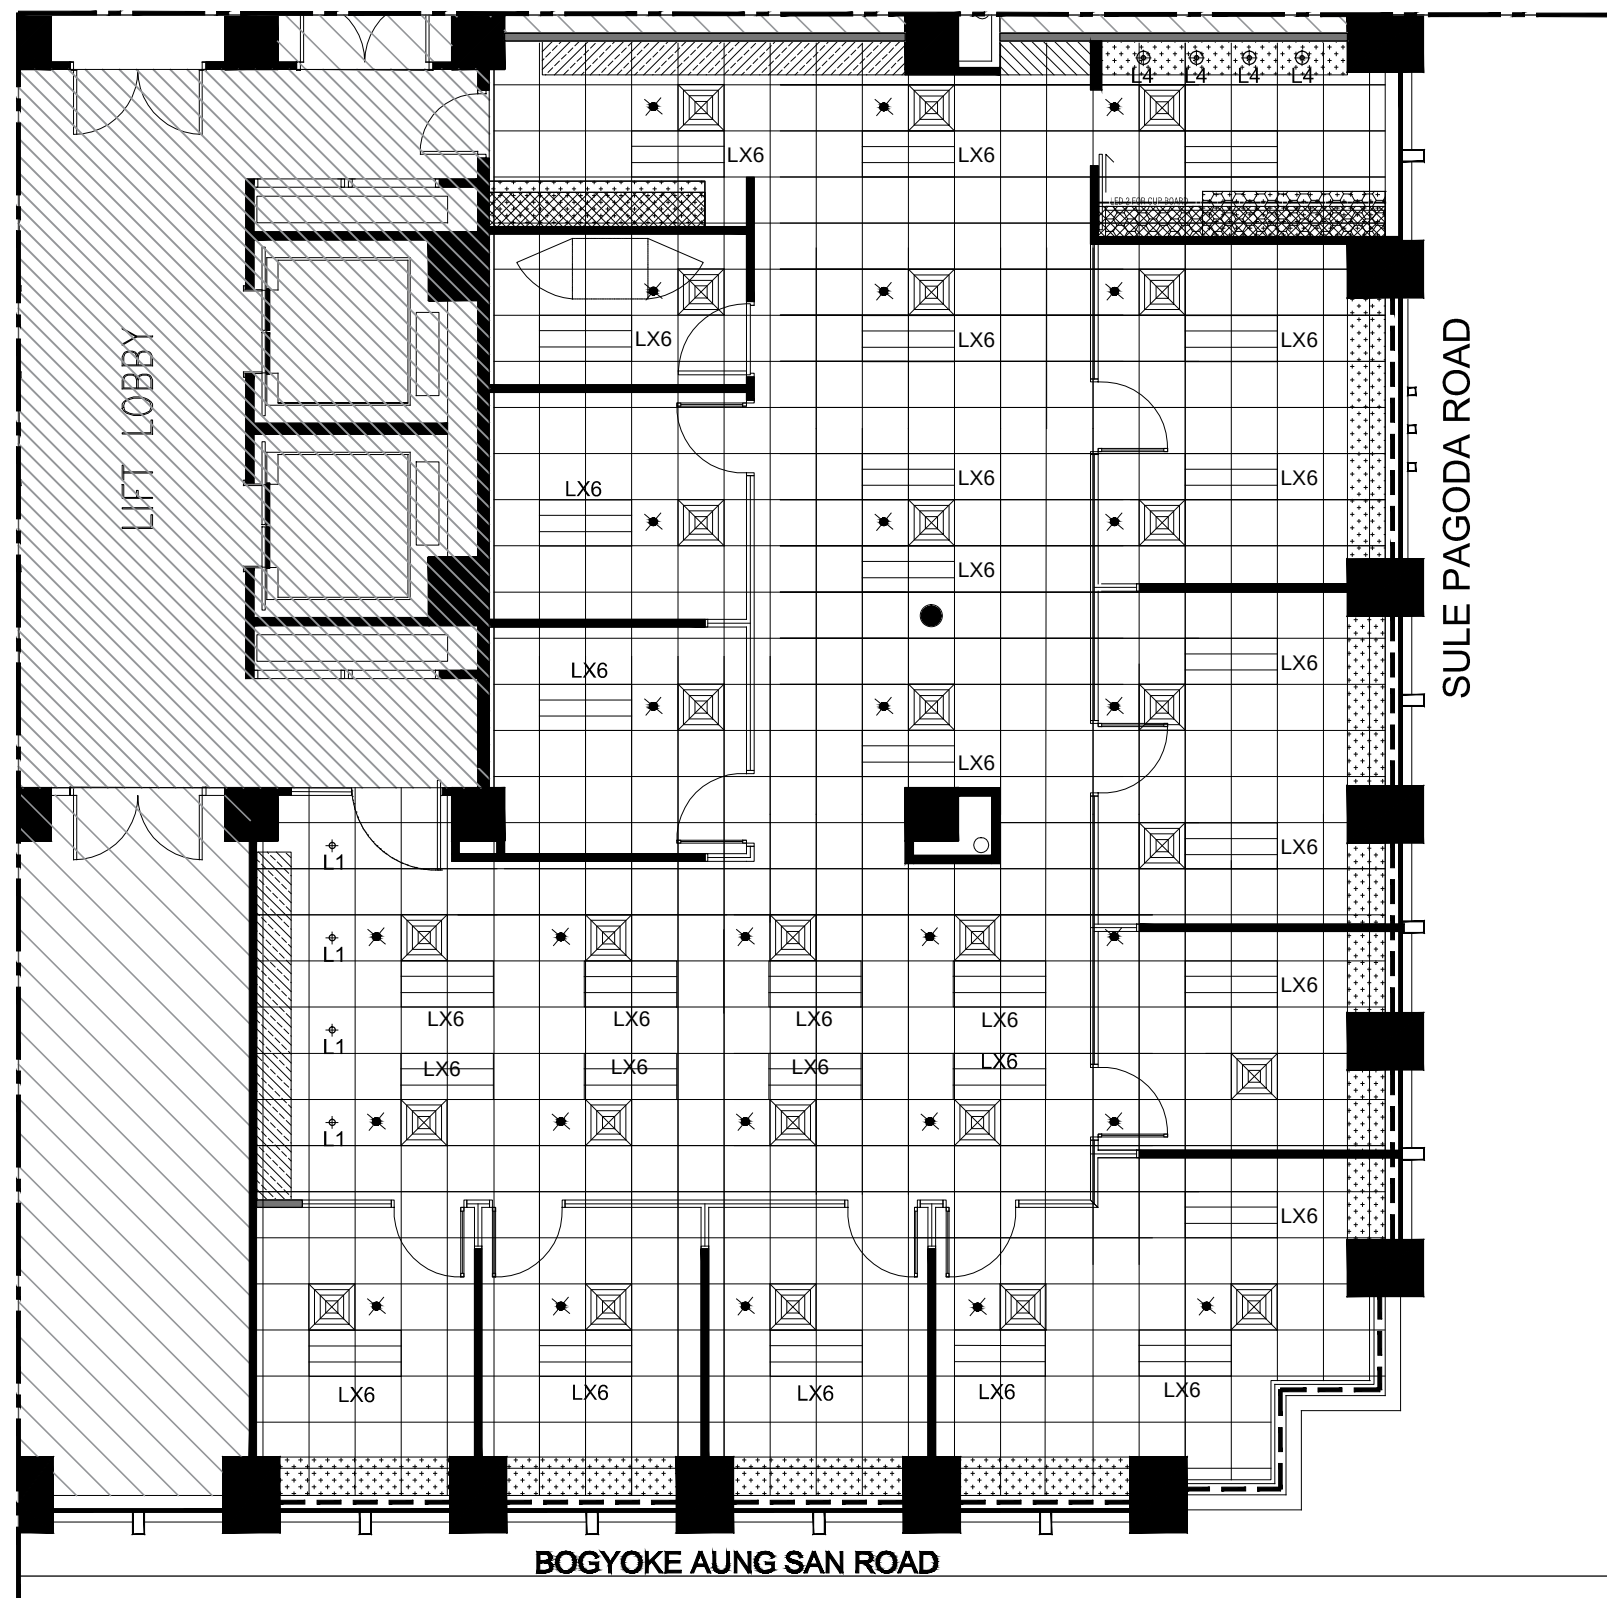


CEILING FINISHES LEGEND

	CLEX : EXISTING T-BAR CEILING TILES
	CL01 : NEW GYPSUM PLASTERBOARD CEILING WITH OFF WHITE PAINT FINISHED
	CL02 : NEW TIMBER LAMINATED CEILING
	CL03 : NEW GYPSUM PLASTERBOARD CEILING WITH DARK GREY PAINT FINISHED
	CL04 : NEW PLYWOOD CEILING WITH BLACK PAINT FINISHED
	CL05 : REUSE & RELOCATION EXISTING T-BAR CEILING TILES

REFLECTED CEILING NOTE:

1. REFER TO M&E DWGS. FOR ALL AIR CONDITIONING, FIRE PROTECTION AND ELECTRICAL SERVICES. INFORM ID SHOULD ANY DISCREPANCY OR INCONSISTENCY OCCUR BETWEEN ID AND M&E DWGS.
2. MAIN CONTRACTOR TO CO-ORDINATE ALL M&E WORKS BY NORMINATED CONTRACTOR
3. CONTRACTOR TO MAKE GOOD AND APPLY NEW PAINT PA1 , TO ALL CEILING
4. ALL SERVICES REFER M&E DRAWING & SPEC.
5. MAIN CONTRACTOR TO INSTALL ALL NEW CEILING TILES
6. LIGHTING SPECIFICATIOND REFER TO LIGHTING SCHEDULE DWG. NO. D-902 IN CONJUNCTION WITH M&E SPEC.
7. ALL WALL MOUNTED SWITCHES/DIMMER TO BE 1000mm H THROUGH OUT UNLESS SPECIFIED OTHERWISE
8. NEW CEILING TILES TO MATCH EXISTING IN TYPE AND FINISHES
9. MAIN CONTRACTOR TO SURVEY AND CONFIRMED ALL EXISTING & NEW EXIT SIGN LOCATIONS, FINAL LOCATION TO BE CONFIRMED BY ID DESIGNER
10. MAINTAIN ALL SMOKE DETECTORS UNLESS SPECIFIED OTHERWISE
11. FINAL LOCATION OF LIGHT IN GYPSUM CEILING AREA CO-ORDINATE ON SITE WITH ID AND ENGINEER.
12. ALL CEILING LEVELS TO BE EXISTING UNLESS SPECIFIED OTHERWISE
13. ALL SPRINKLER IN ALL GYPSUM CEILING AREA TO BE CONCEALED TYPE UNLESS SPECIFIED OTHERWISE
14. ALL NEW GYPSUM PLASTER BOARD CEILING TO BE PAINTED P3
15. FLUORESCENT LIGHT L6 SHALL BE UNDER ALL HANGING CABINETS AND ABOVE CABINET LINK IN THE SAME CIRCVIT WITH LOCALLY SWITCH TO EACH JOINERY UNIT REFER TO CABINET DETAIL DRAWING
16. ELECTRICAL CONTRACTOR TO CONFIRM THE GENERAL/OVERALL LIGHTING LEVEL TO MEET REQUIRED STANDARD
17. ALL ENDCLOSED ROOMS TO HAVE INDIVIDUAL LIGHT SWITCH.
18. L5-AND INSTALL OVER LAPPING (NO DARK SHADOW) TO MEET STANDARD/REQUIRED 500 LUX LIGHTING AND TO BE LINK IN THE SAME CIRCUIT
19. ALL CEILING LEVEL TO BE MAINTAINED AS EXISTING UNLESS SPECIFIED OTHERWISE

REFLECTED CEILING LEGEND:

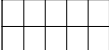	L1	SINGLE / ADJUSTABLE LED 5W. LAMP
	L2	ADJUSTABLE LED 5W. LAMP
	L3	REUSE EXISTING PENDANT LAMP
	L4	PENDANT LAMP AT PANTRY PHASE 1
	L5	PENDANT LAMP AT PANTRY PHASE 2
	LX6	EXISTING STANDARD LIGHT TROFFER DIFFUSER ,NOM.SIZE 1200 x 600 mm.
	L7	STANDARD LIGHT TROFFER DIFFUSER, NOM.SIZE 1200 x 600 mm.
	L8	STANDARD LIGHT TROFFER DIFFUSER, NOM.SIZE 600 x 600 mm.
	L9	LED STRIP LIGHT

© LUX89 CO., LTD. April 2020

REFERENCE MAP

TH

NOTES

1. DO NOT SCALE DRAWINGS. WRITTEN DIMENSIONS GOVERN.
2. ALL DIMENSIONS ARE IN MILLIMETERS UNLESS NOTED OTHERWISE.
3. ALL DIMENSIONS SHALL BE VERIFIED ON SITE BEFORE PROCEEDING WITH THE WORK. LUX89 SHALL BE NOTIFIED IN WRITING OF ANY DISCREPANCIES.
4. THIS DRAWING MUST BE READ IN CONJUNCTION WITH ALL RELEVANT CONTRACTS, SPECIFICATIONS, REPORTS AND DRAWINGS.

THIS DRAWING IS AN UNCONTROLLED COPY. UNLESS NOTED OTHERWISE

T1	CP	FOR TENDER	10/04/2020
REV	BY	DESCRIPTION	DATE

CLIENT / PROJECT

**Tilleke & Gibbins
Myanmar Limited.**

PROJECT MANAGER & INTERIOR DESIGNER

LUX 89 CO., LTD.
7/89 Soi Rama 2 Soi 54/4, Samae Dam,
Bang Khun Thian, Bangkok, Thailand 10150
E LUX89.BKK@GMAIL.COM W LUX89.COM
T 66(2) 416 9189

ARCHITECTURE

STRUCTURE ENGINEER

M&E ENGINEER

ACCO ENGINEERING CO., LTD.
1213/430 Soi Ladprao94 (Panjamit) Plubpla, Wang Thonglang,
Bangkok, Thailand. 10310
E APISAK@ACCO.CO.TH **W** ACCO@ACCO.CO.TH
T 66(2) 559 0177-9, **F** 66 (2) 559 0176

DRAWING


REFLECTED CEILING PLAN

PHASE 1

STATUS

STATUS FOR TENDER

SCALE AT 1/8"=1'-0"	DRAWN AK	CO-ORDINATED CP	CHECKED CP	PLotted DATE 10/04/2020
JOB NO. PTD 20.001	DRAWING NUMBER D-109		REVISION T1	

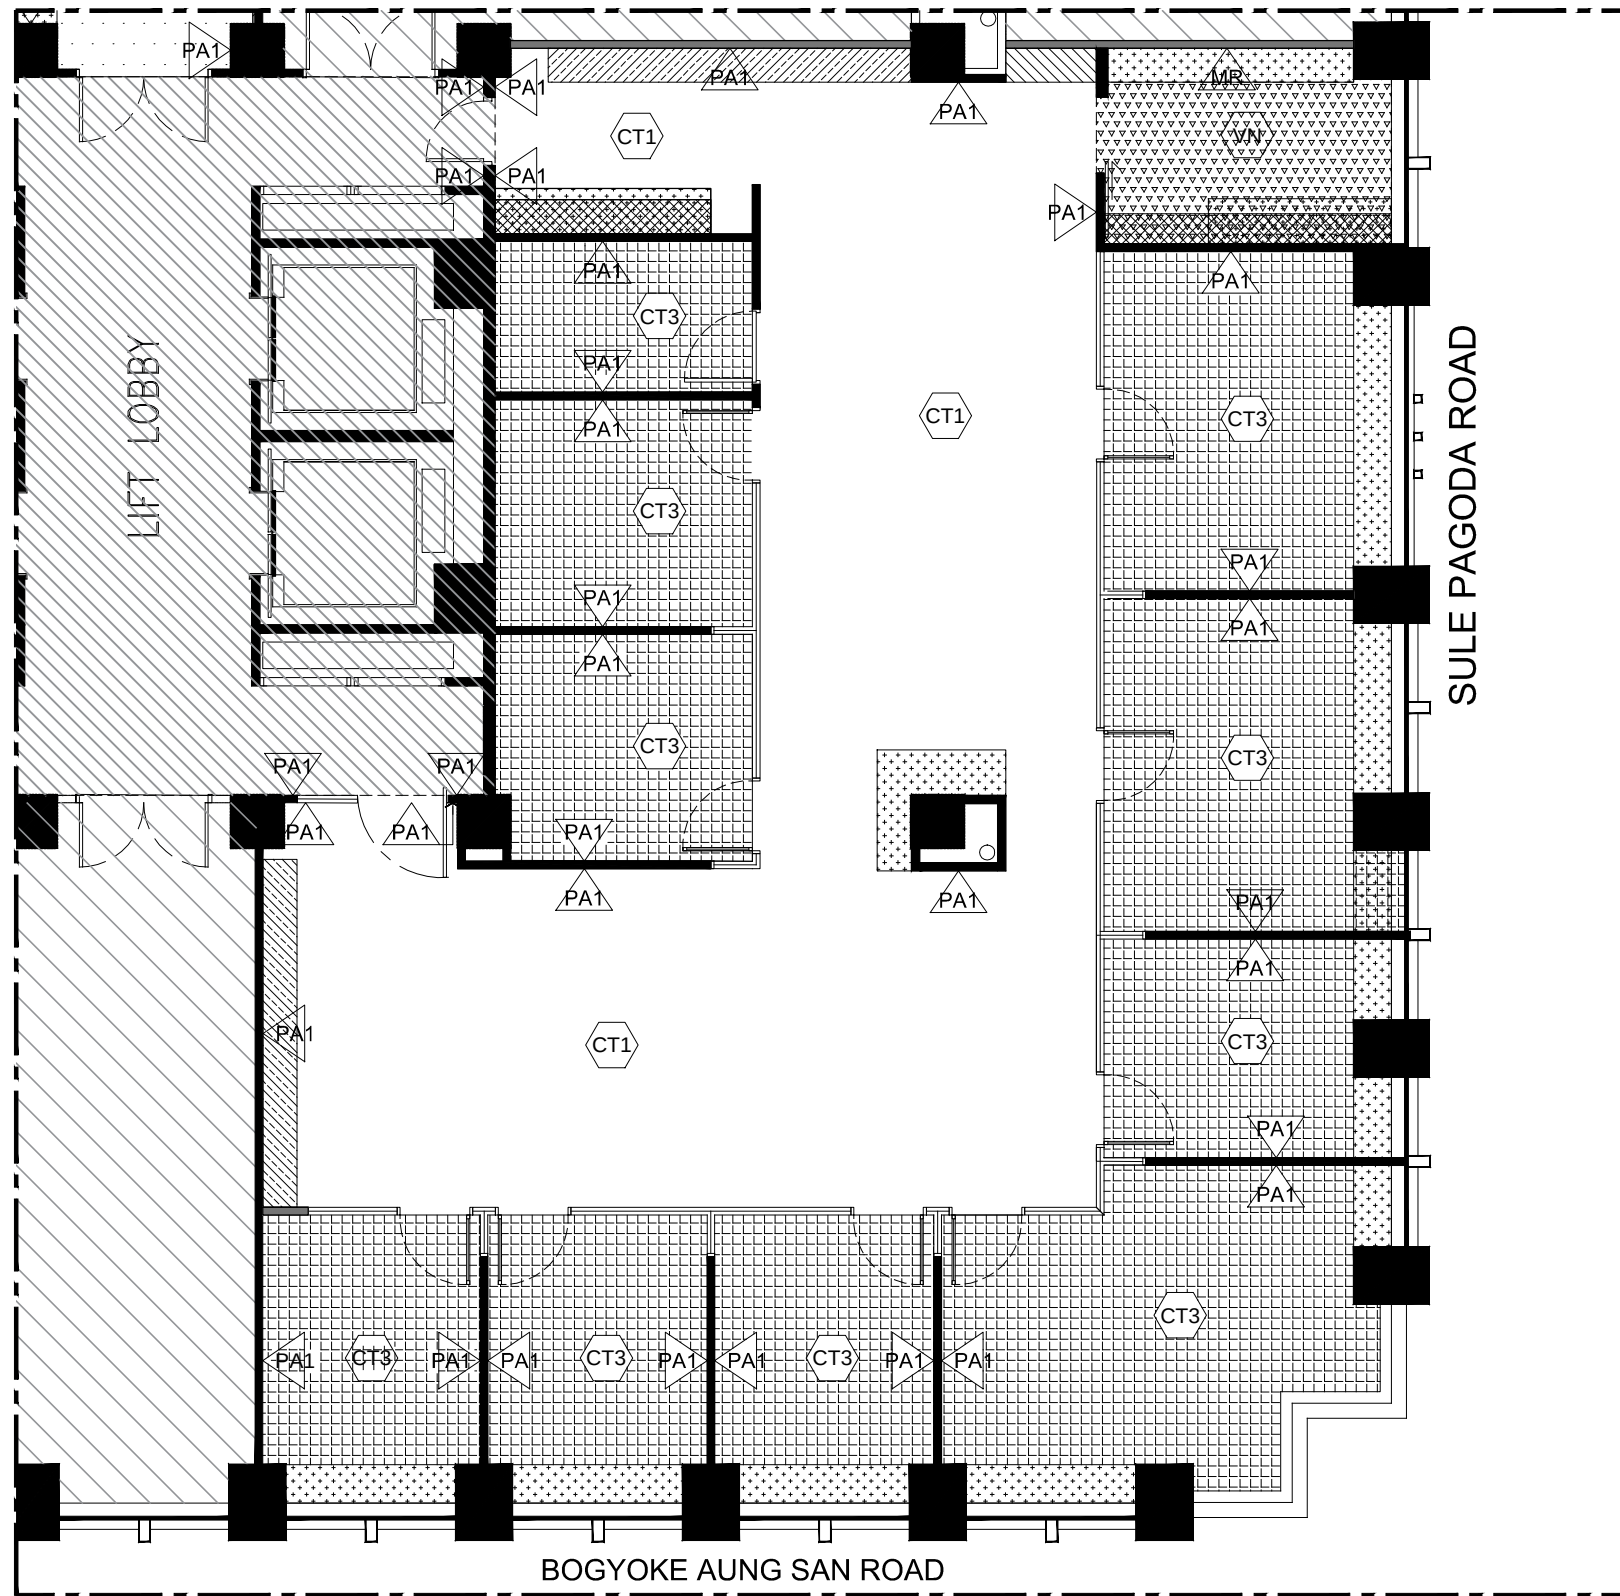

WALL FINISH LEGEND

PA1	PAINT WALL - WHITE
FB1	FABRIC - WALL
FB2	FABRIC - BENCH
WB	WHITE BOARD
MR	MIRROR
G1	CLEAR GLASS
G2	WHITE GLASS
LA1	LAMINATE

FLOOR FINISH LEGEND

CT1	CARPET TILE
CT2	CARPET TILE
CT3	CARPET TILE
TL1	TILE FLOOR SIZE 600 x 1200 mm.
VN1	VINYL FLOOR

PHASE 1 : NEW OFFICE

CLOSE OFFICE

MANAGER	1 ROOM	11.00 sqm.
OFFICE 2 PAX #5 ROOMS	10.00 -11.00 sqm.	
OFFICE 4 PAX #2 ROOMS	16.50 - 17.00 sqm.	
MEETINGROOM 10 PAX # 1 ROOM	22.00 sqm.	

STAFF	
WORKSTATION 1500x750	= 8 PAX
PANTRY AREA	10.00 sqm.
HUB ROOM	7 sqm.

REFERENCE MAP

NORTH

NOTES

1. DO NOT SCALE DRAWINGS. WRITTEN DIMENSIONS GOVERN.

2. ALL DIMENSIONS ARE IN MILLIMETERS UNLESS NOTED OTHERWISE.

3. ALL DIMENSIONS SHALL BE VERIFIED ON SITE BEFORE PROCEEDING WITH THE WORK. LUX89 SHALL BE NOTIFIED IN WRITING OF ANY DISCREPANCIES.


4. THIS DRAWING MUST BE READ IN CONJUNCTION WITH ALL RELEVANT CONTRACTS, SPECIFICATIONS, REPORTS AND DRAWINGS.

© 2020 COPYRIGHT OF THIS DRAWING IS VESTED IN LUX89 CO., LTD.

THIS DRAWING IS AN UNCONTROLLED COPY, UNLESS NOTED OTHERWISE

--	--	

REFERENCE MAP		NORTH	
NOTES 1. DO NOT SCALE DRAWINGS. WRITTEN DIMENSIONS COVER. 2. ALL DIMENSIONS ARE IN MILLIMETERS UNLESS NOTED OTHERWISE. 3. ALL DIMENSIONS SHALL BE VERIFIED ON SITE BEFORE PROCEEDING WITH THE WORK. LUX89 SHALL BE NOTIFIED IN WRITING OF ANY DISCREPANCIES. 4. THIS DRAWING MUST BE READ IN CONJUNCTION WITH ALL RELEVANT CONTRACTS, SPECIFICATIONS, REPORTS AND DRAWINGS. © 2020 COPYRIGHT OF THIS DESIGN IS VESTED IN LUX89 CO., LTD.	
THIS DRAWING IS AN UNCONTROLLED COPY. UNLESS NOTED OTHERWISE	
<table><tr><td></td><td></td><td></td><td></td></tr><tr><td></td><td></td><td></td><td></td></tr><tr><td></td><td></td><td></td><td></td></tr><tr><td></td><td></td><td></td><td></td></tr><tr><td></td><td></td><td></td><td></td></tr><tr><td></td><td></td><td></td><td></td></tr><tr><td></td><td></td><td></td><td></td></tr><tr><td></td><td></td><td></td><td></td></tr><tr><td></td><td></td><td></td><td></td></tr><tr><td></td><td></td><td></td><td></td></tr><tr><td></td><td></td><td></td><td></td></tr><tr><td></td><td></td><td></td><td></td></tr><tr><td></td><td></td><td></td><td></td></tr><tr><td></td><td></td><td></td><td></td></tr><tr><td></td><td></td><td></td><td></td></tr><tr><td>T1</td><td>CP</td><td>FOR TENDER</td><td>10/04/2020</td></tr><tr><td>REV</td><td>BY</td><td>DESCRIPTION</td><td>DATE</td></tr></table>	T1	CP	FOR TENDER	10/04/2020	REV	BY	DESCRIPTION	DATE
T1	CP	FOR TENDER	10/04/2020	
REV	BY	DESCRIPTION	DATE	
CLIENT / PROJECT Tilleke & Gibbins Myanmar Limited. PROJECT MANAGER & INTERIOR DESIGNER LUX 89 CO., LTD. 7/89 Soi Rama 2 Soi 54/4,Samae Dam, Bang Khun Thian, Bangkok , Thailand10150 E LUX89.BKK@GMAIL.COM W LUX89.COM T 66(2) 416 9189	
ARCHITECTURE	
STRUCTURE ENGINEER	
M&E ENGINEER ACCO ENGINEERING CO., LTD. 1213/430 Soi Ladprao94 (Panjamit) Plubpla, Wang Thonglang, Bangkok, Thailand. 10310 E APISAK@ACCO.CO.TH W ACCO@ACCO.CO.TH T 66(2) 559 0177-9, F 66 (2) 559 0176	
DRAWING WALL & FLOOR FINISHES PLAN PHASE 2	
STATUS FOR TENDER	
SCALE AT A4 AS	DRAWN	CHECKED	PLOTTED	
1 :100	AK	CP	CP	
JOB NO.	DRAWING NUMBER	REVISION	
PTD 20.001	D-112	T1	

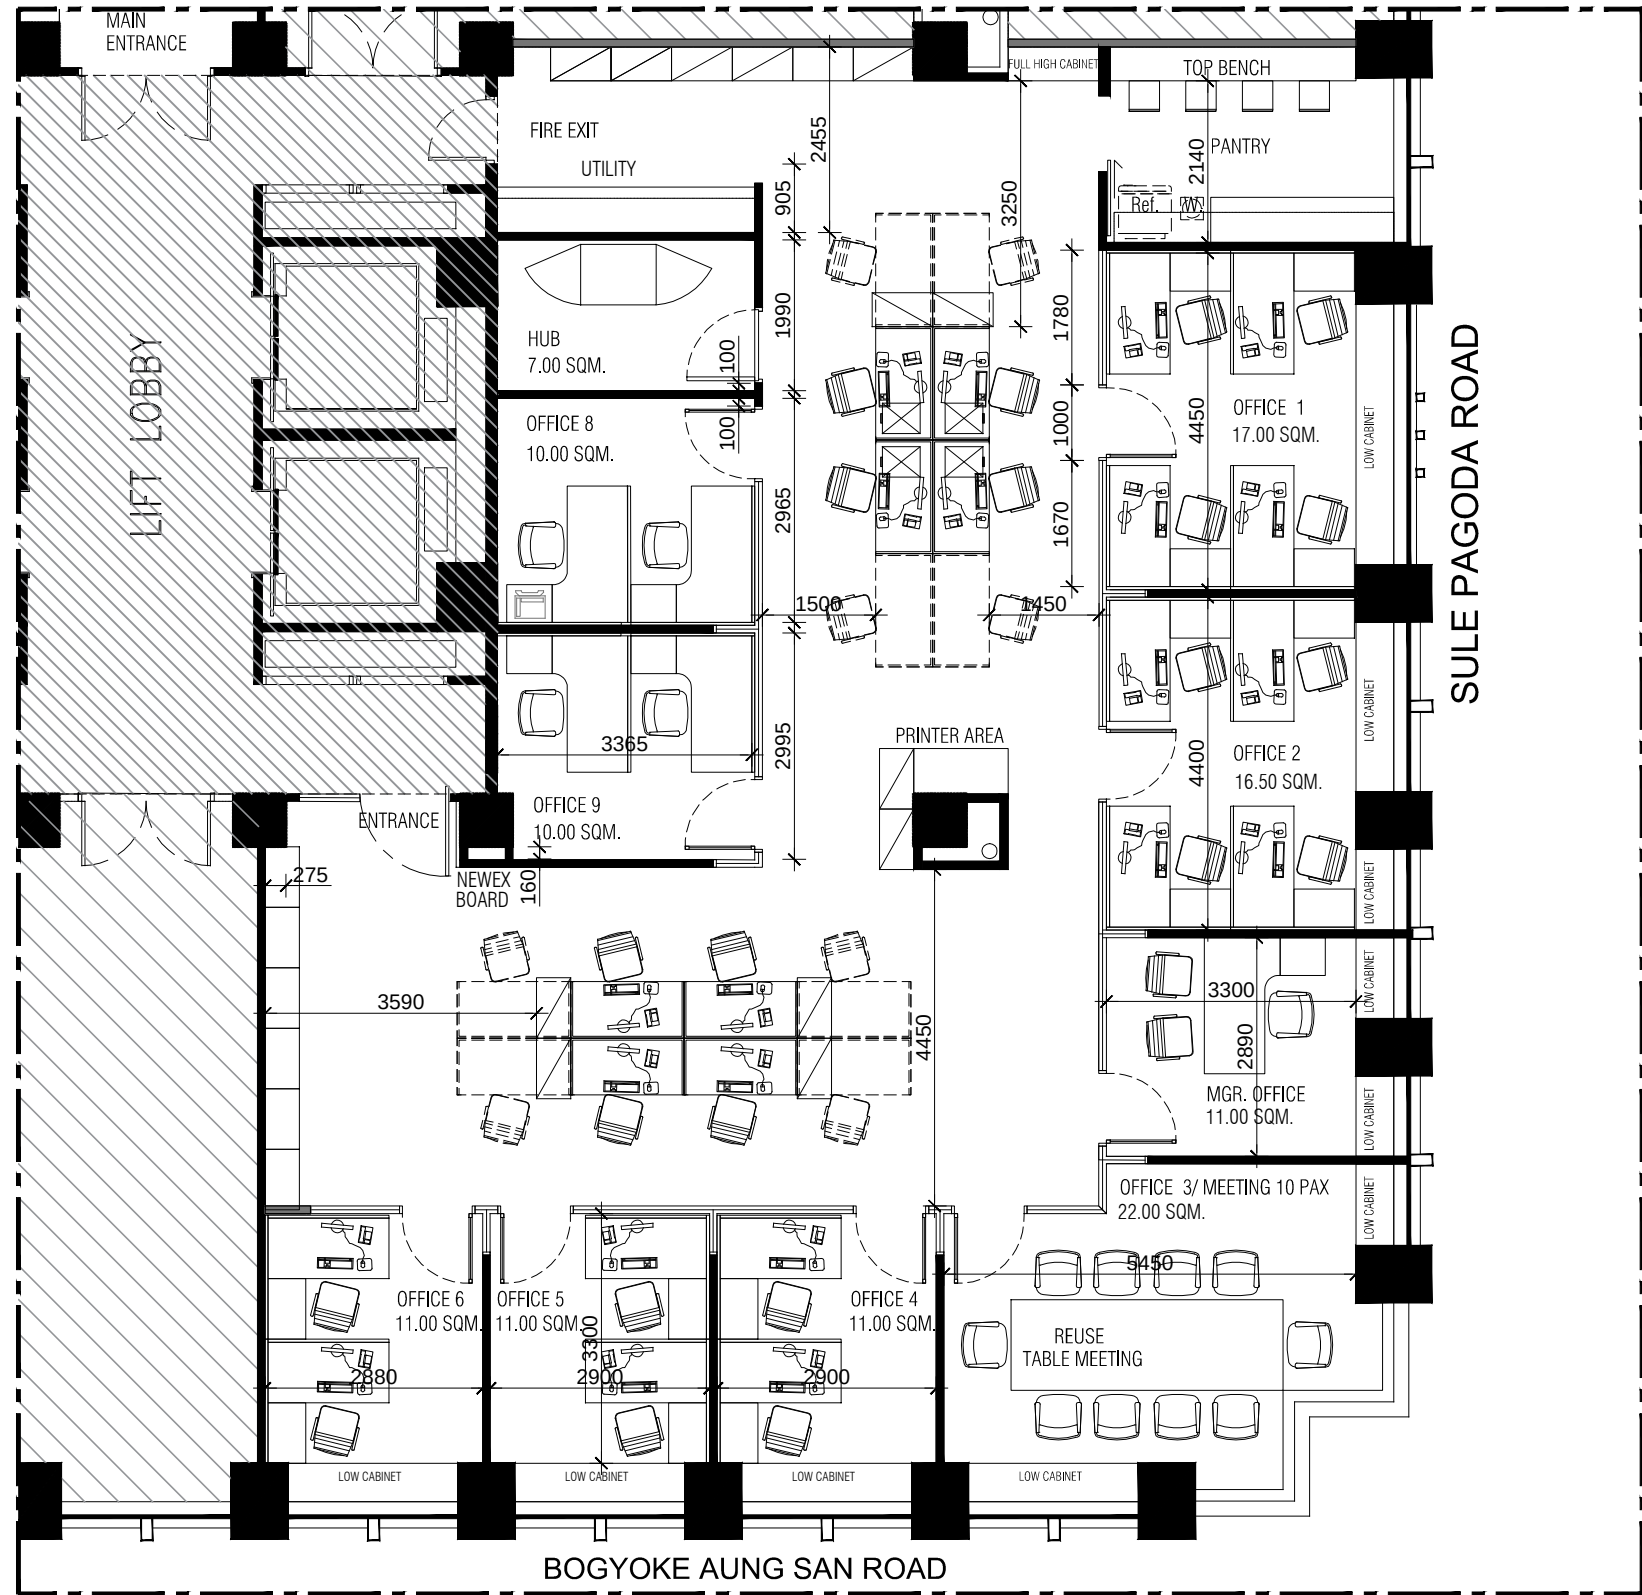

CLOSE OFFICE

MANAGER	1 ROOM	11.00 sqm.
OFFICE 2 PAX #5 ROOMS	10.00 -11.00 sqm.	
OFFICE 4 PAX #2 ROOMS	16.50 - 17.00 sqm.	
MEETINGROOM 10 PAX # 1 ROOM	22.00 sqm.	

STAFF	
WORKSTATION 1500x750	= 8 PAX
PANTRY AREA	10.00 sqm.
HUB ROOM	7 sqm.

REFERENCE MAP

NORTH

NOTES

1. DO NOT SCALE DRAWINGS. WRITTEN DIMENSIONS GOVERN.

2. ALL DIMENSIONS ARE IN MILLIMETERS UNLESS NOTED OTHERWISE.

3. ALL DIMENSIONS SHALL BE VERIFIED ON SITE BEFORE PROCEEDING WITH THE WORK. LUX89 SHALL BE NOTIFIED IN WRITING OF ANY DISCREPANCIES.

4. THIS DRAWING MUST BE READ IN CONJUNCTION WITH ALL RELEVANT CONTRACTS, SPECIFICATIONS, REPORTS AND DRAWINGS.

© 2020 COPYRIGHT OF THIS DRAWING IS VESTED IN LUX89 CO., LTD.

THIS DRAWING IS AN UNCONTROLLED COPY, UNLESS NOTED OTHERWISE

T1	CP	FOR TENDER	10/04/2020
REV	BY	DESCRIPTION	DATE

CLIENT / PROJECT

Tilleke & Gibbins
Myanmar Limited.

PROJECT MANAGER & INTERIOR DESIGNER

LUX 89 CO., LTD.

7/89 Soi Rama 2 Soi 54/4 Samae Dam,

Bang Khun Thian, Bangkok, Thailand10150

E LUX89.BKK@GMAIL.COM W LUX89.COM

T 66(2) 416 9189

ARCHITECTURE

STRUCTURE ENGINEER

M&E ENGINEER

ACCO ENGINEERING CO., LTD.

1213/430 Soi Ladprao94 (Panjamit) Plubpla, Wang Thonglang,

Bangkok, Thailand. 10310

E APISAK@ACCO.CO.TH W ACCO@ACCO.CO.TH

T 66(2) 559 0177-9, F 66 (2) 559 0176

DRAWING

SETOUT PLAN

PHASE 1


STATUS

FOR TENDER

SCALE AT A3	DRAWN	CO-ORDINATED	CHECKED	PLOTTED
1:100	AK	CP	CP	10/04/2020
JOB NO.	DRAWING NUMBER	REVISION		
PTD 20.001	D-113	T1		




JOB NO. PTD 20.001	DRAWING NUMBER D-114	REASON T1
------------------------------	--------------------------------	---------------------

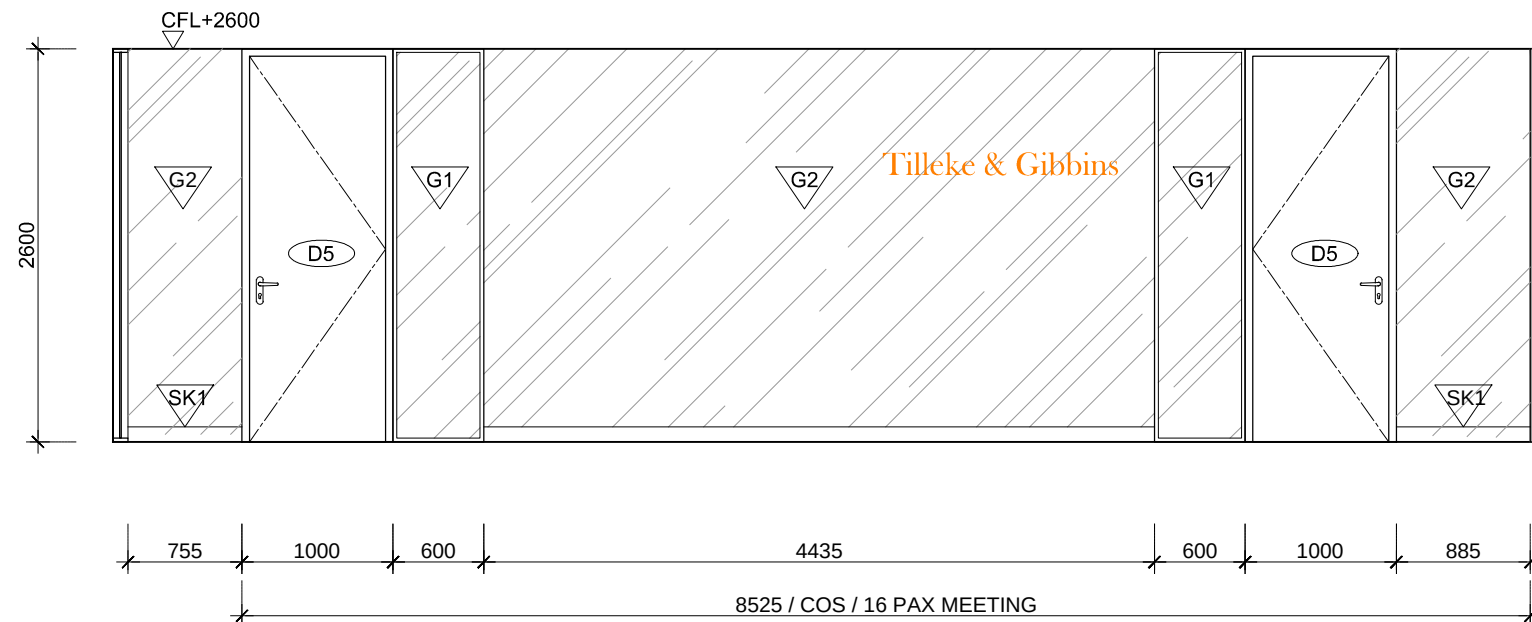

3

ELEVATION


Scale: 1:50

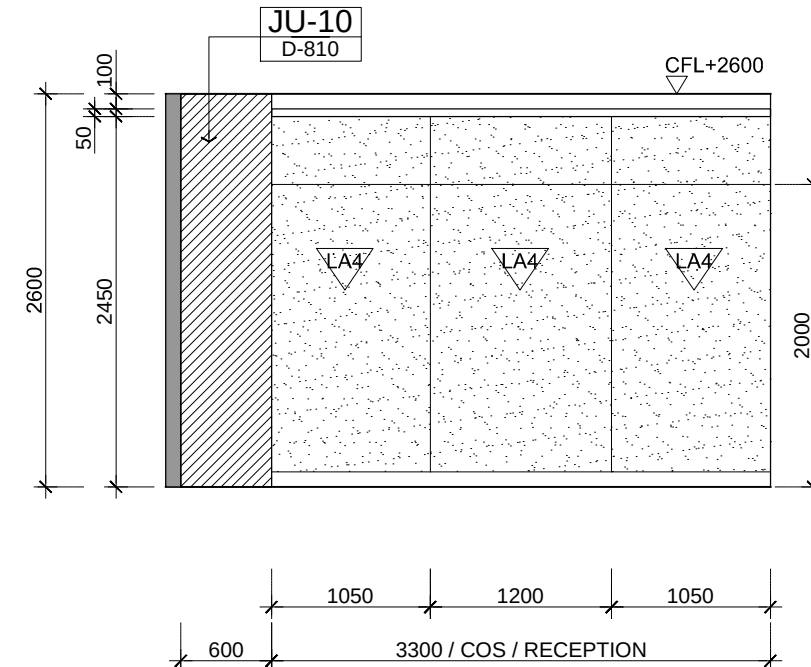

4

ELEVATION


Scale: 1:50

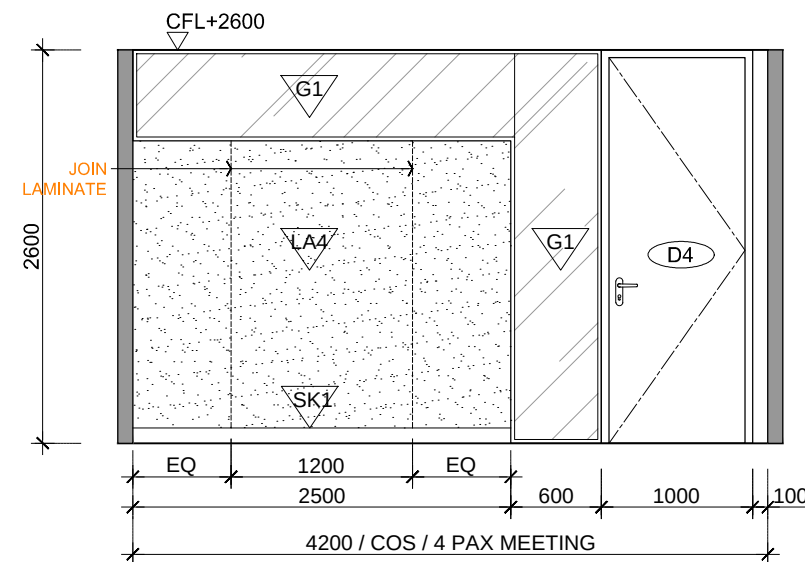

5

ELEVATION

Scale: 1:50

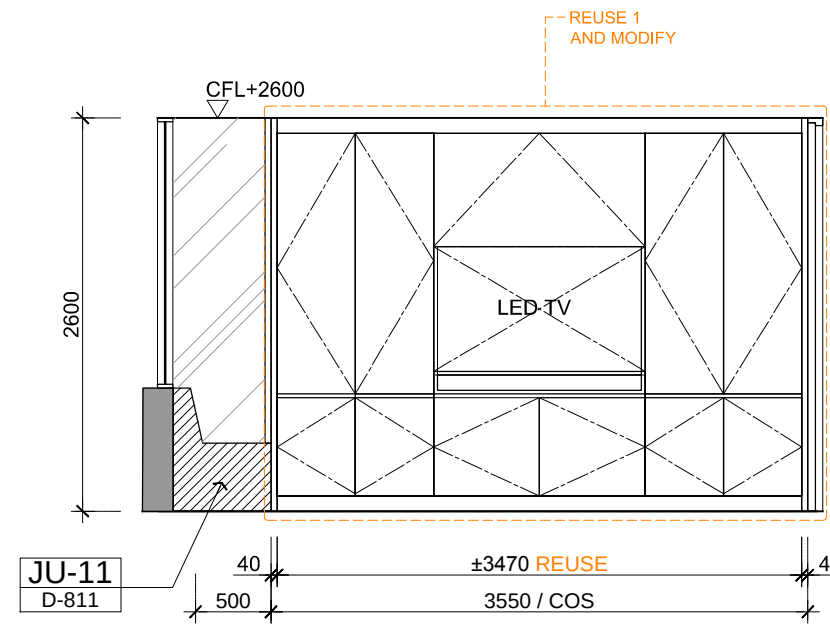

6

ELEVATION


Scale: 1:50

REFERENCE MAP


</



JOB NO. PTD 20.001	DRAWING NUMBER D-203	REVISION T1
------------------------------	--------------------------------	-----------------------

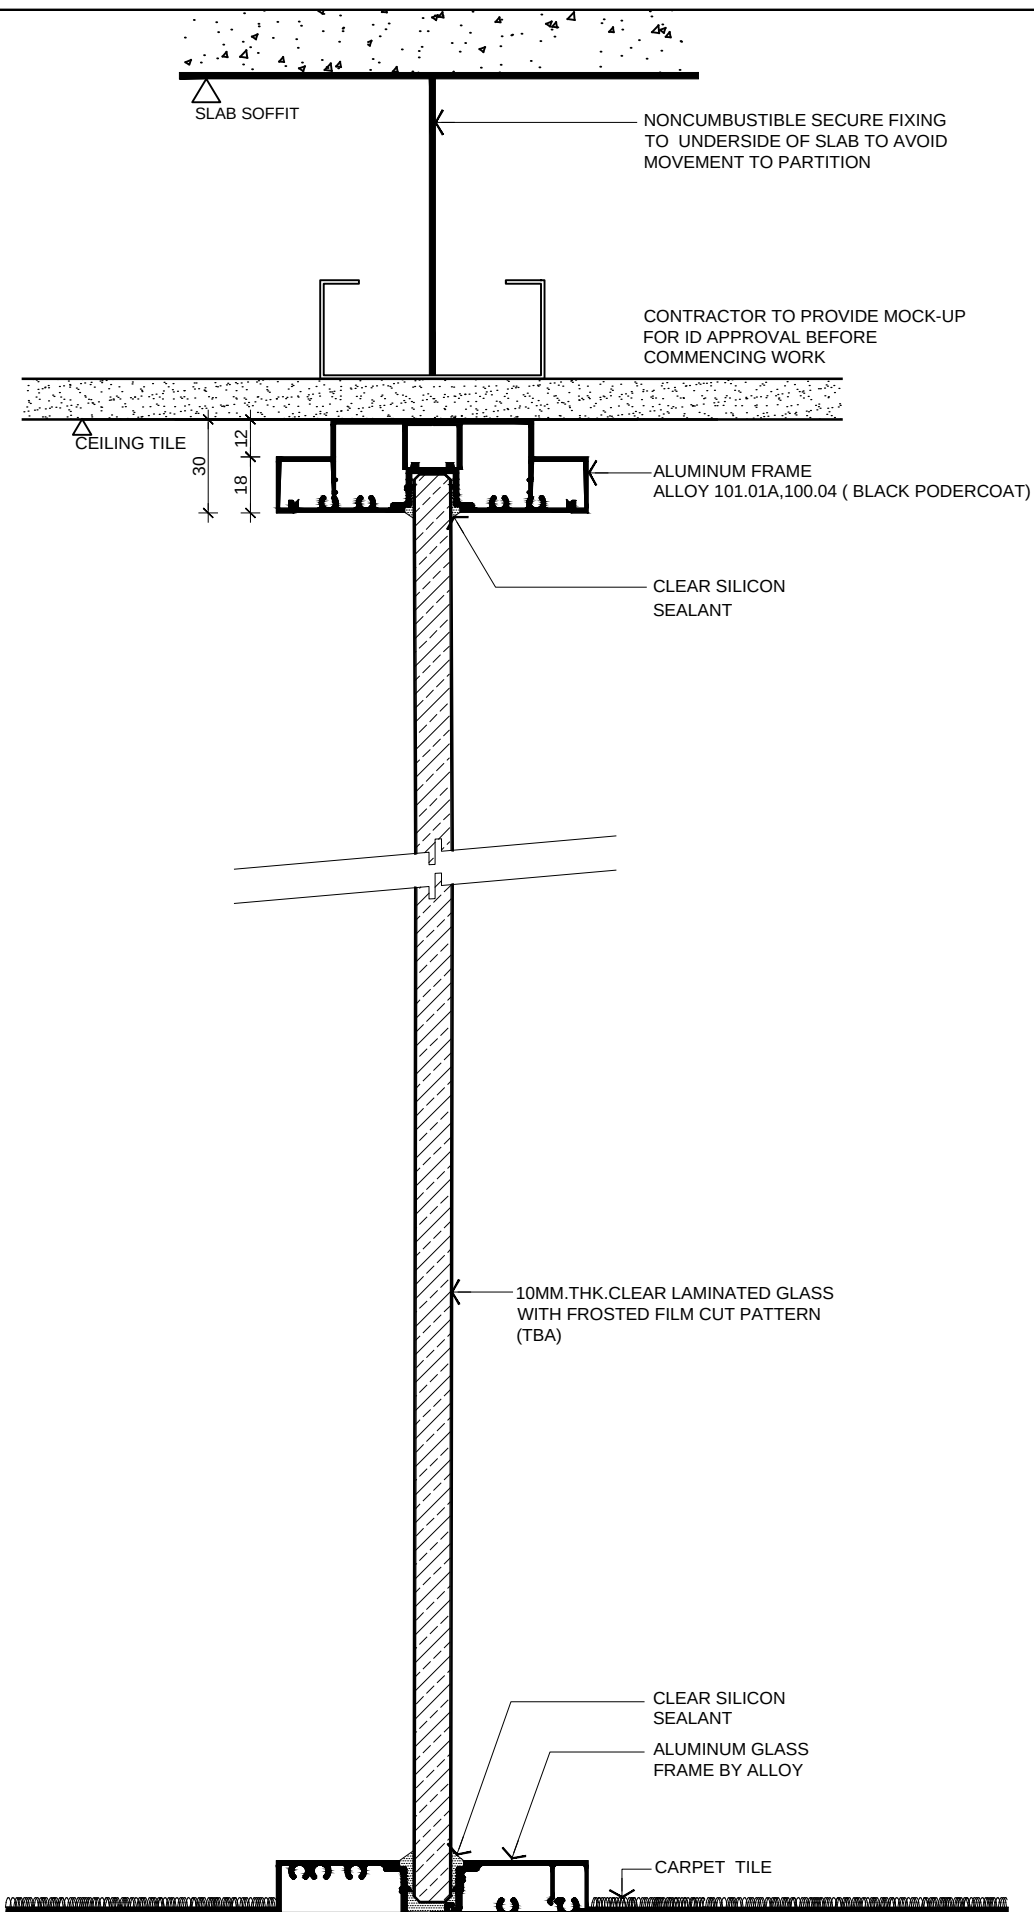

P1 DETAIL - GLASS PARTITION-SINGLE LAYER

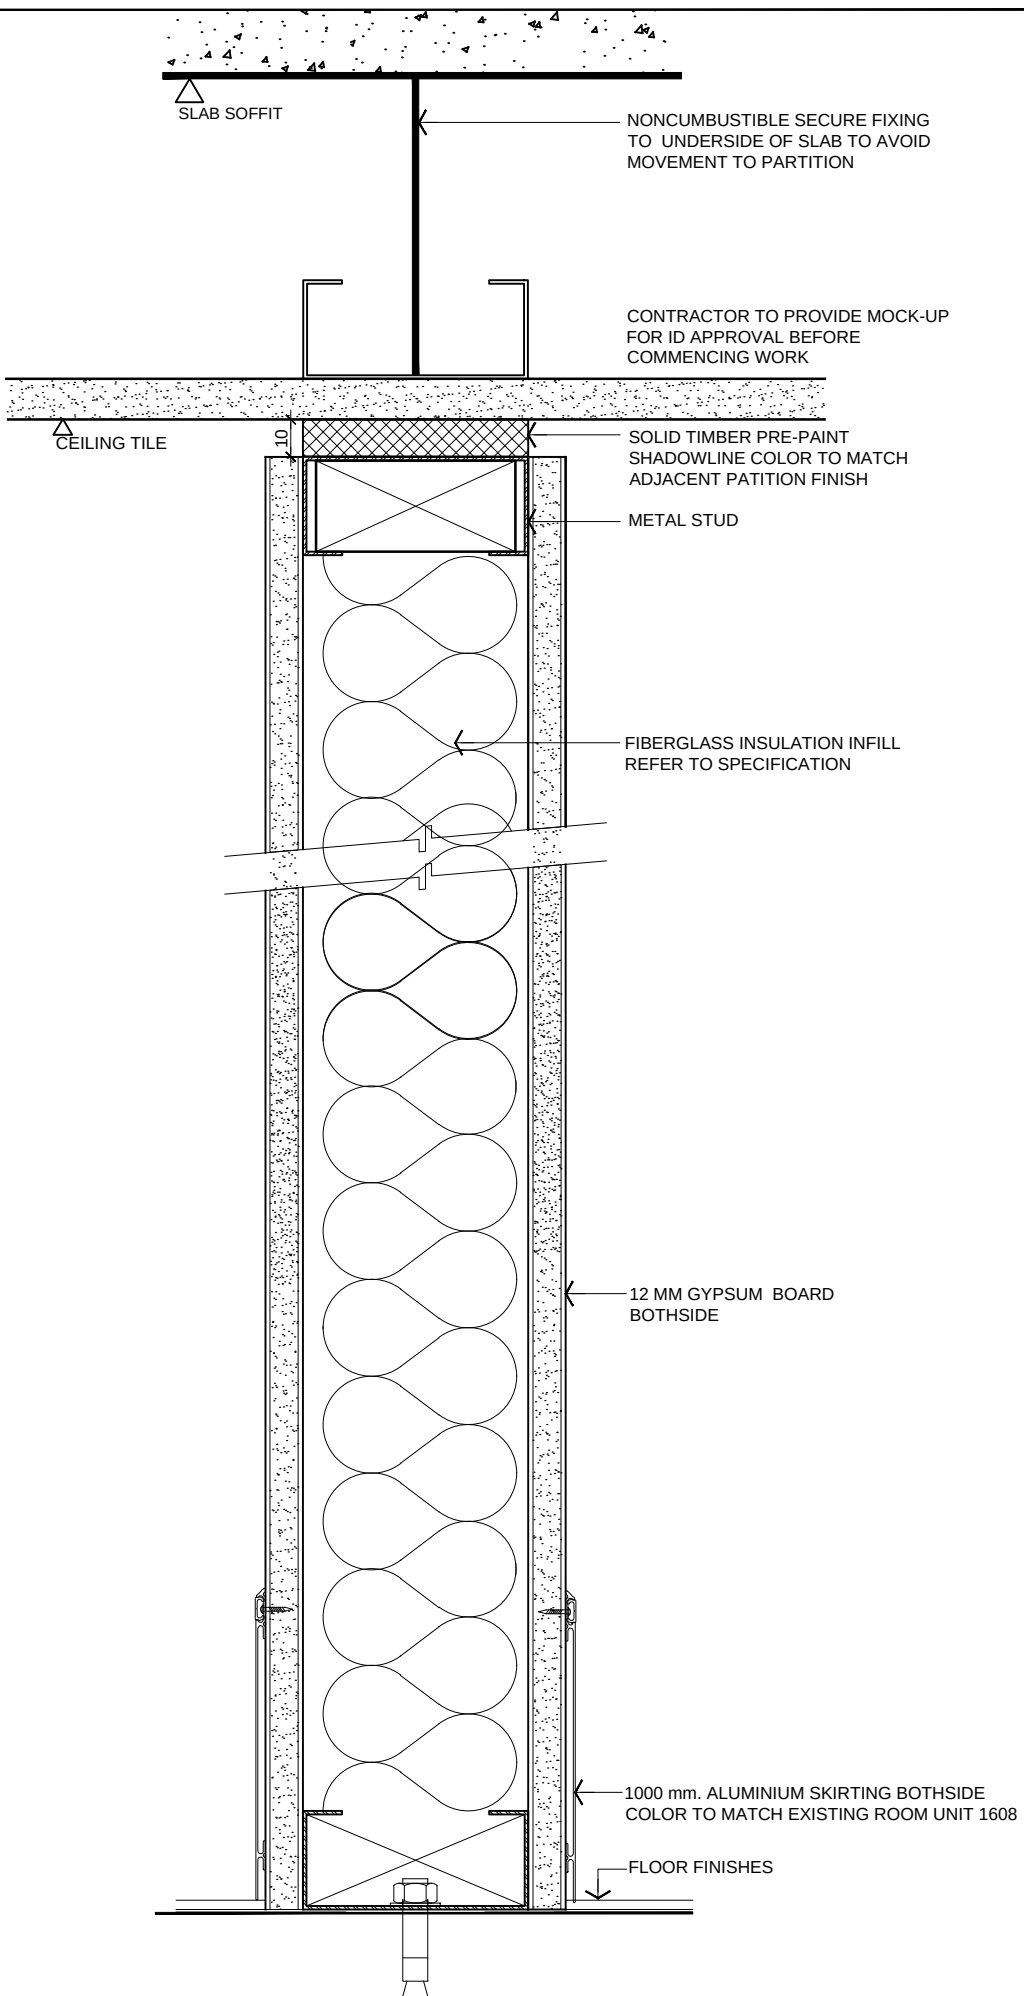

P2 DETAIL - DRYWALL PARTITION-SINGLE LAYER Scale: N.T.S.

© LUX89 CO., LTD. April 2020

REFERENCE MAP

RTH

NOTES

1. DO NOT SCALE DRAWINGS. WRITTEN DIMENSIONS GOVERN.
2. ALL DIMENSIONS ARE IN MILLIMETERS UNLESS NOTED OTHERWISE.
3. ALL DIMENSIONS SHALL BE VERIFIED ON SITE BEFORE PROCEEDING WITH THE WORK. LUX89 SHALL BE NOTIFIED IN WRITING OF ANY DISCREPANCIES.
4. THIS DRAWING MUST BE READ IN CONJUNCTION WITH ALL RELEVANT CONTRACTS, SPECIFICATIONS, REPORTS AND DRAWINGS.

© 2020 COPYRIGHT OF THIS DRAWING IS VESTED IN LUX89 CO., LTD.

THIS DRAWING IS AN UNCONTROLLED COPY. UNLESS NOTED OTHERWISE

[illegible]

T1	CP	FOR TENDER	10/04/2020
REV	BY	DESCRIPTION	DATE

CLIENT / PROJECT

**Tilleke & Gibbins
Myanmar Limited.**

PROJECT MANAGER & INTERIOR DESIGNER

LUX 89 CO., LTD.
7/89 Soi Rama 2 Soi 54/4, Samae Dam,
Bang Khun Thian, Bangkok , Thailand 10150
E LUX89.BKK@GMAIL.COM W LUX89.COM
T 66(2) 416 9189

68 XN1

ARCHITECTURE

STRUCTURE ENGINEER

M&E ENGINEER

ACCO ENGINEERING CO., LTD.
1213/430 Soi Ladprao94 (Panjamit) Plubpla, Wang Thonglang,
Bangkok, Thailand. 10310
E APISAK@ACCO.CO.TH W ACCO@ACCO.CO.TH
T 66(2) 559 0177-9. F 66 (2) 559 0176

DEVELOP


PARTITION DETAILS

STATU

FOR TENDER

SCALE AT A1, A3	DRAWN	CO-OPERATED	CHECKED	PLOT DATE
NTS	AK	CB	CB	10/04/2020


JOB NO.	DRAWING NUMBER	REVISION
PTD 20-001	D-300	T1

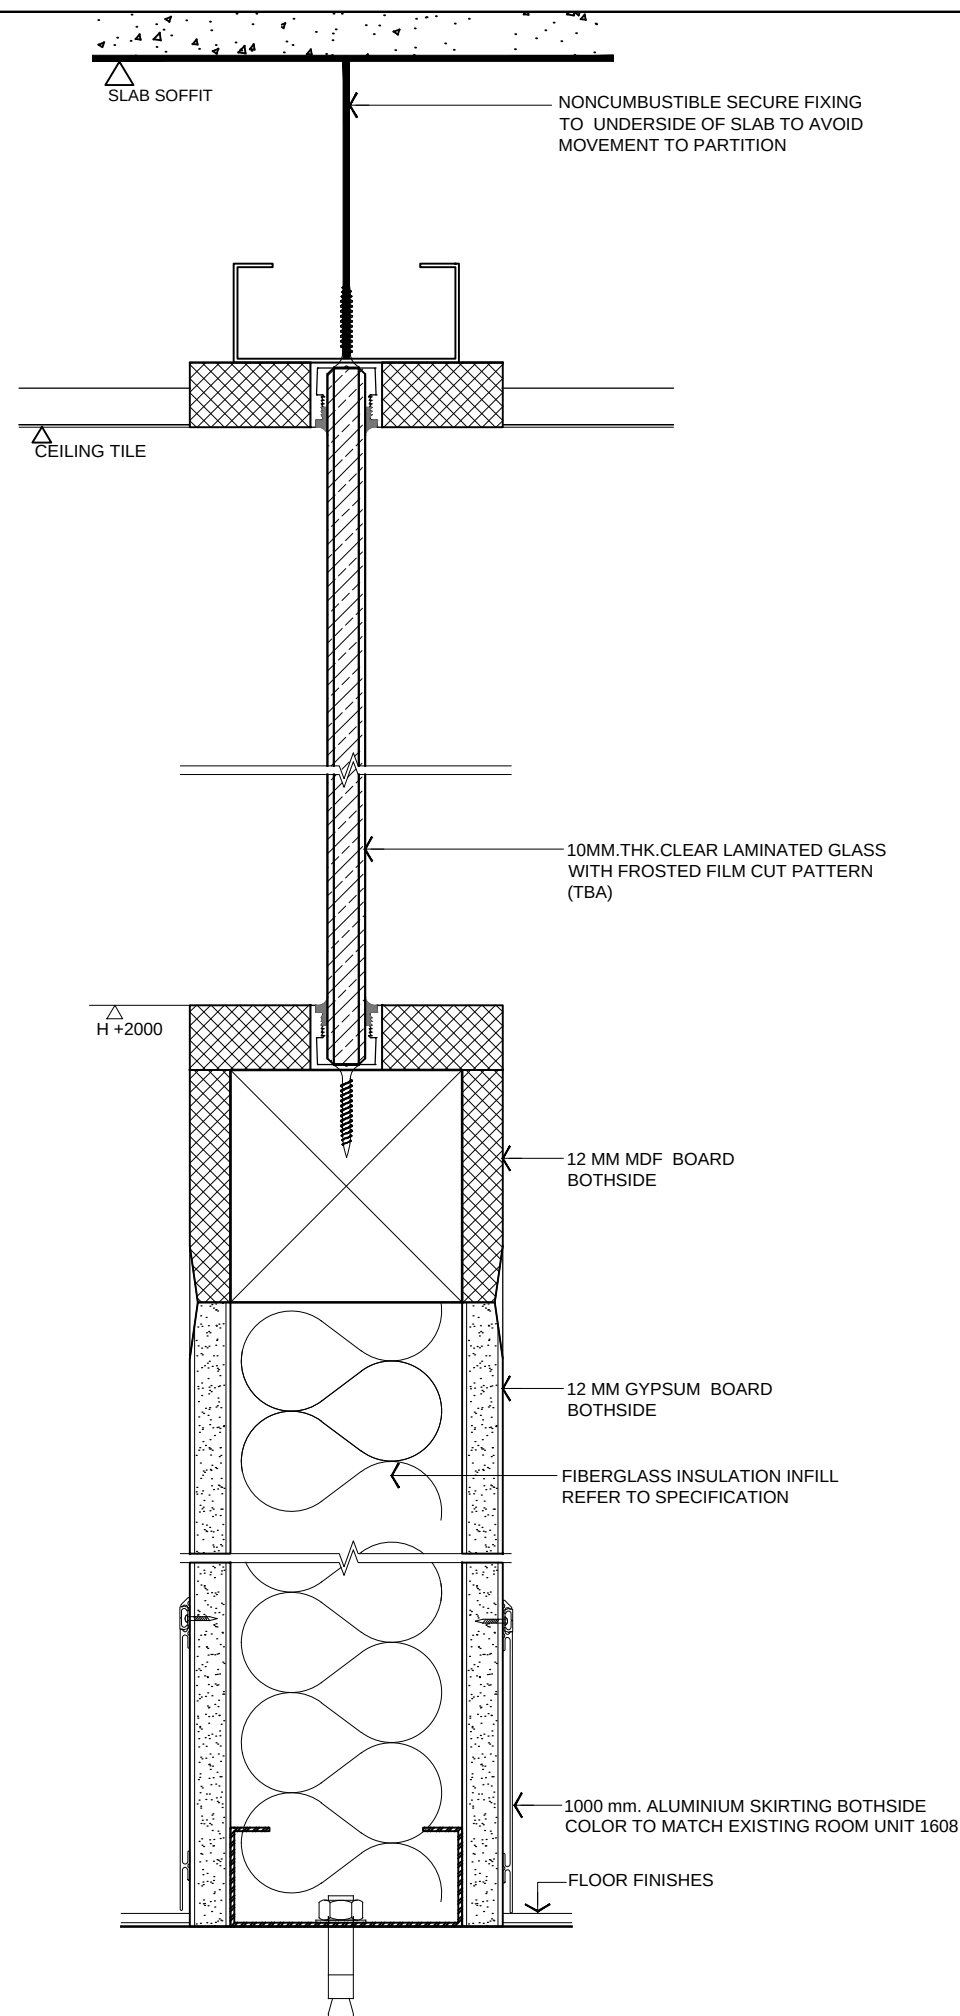

P3

DETAIL - DRYWALL PARTITION-SINGLE LAYER

Scale: N.T.S.

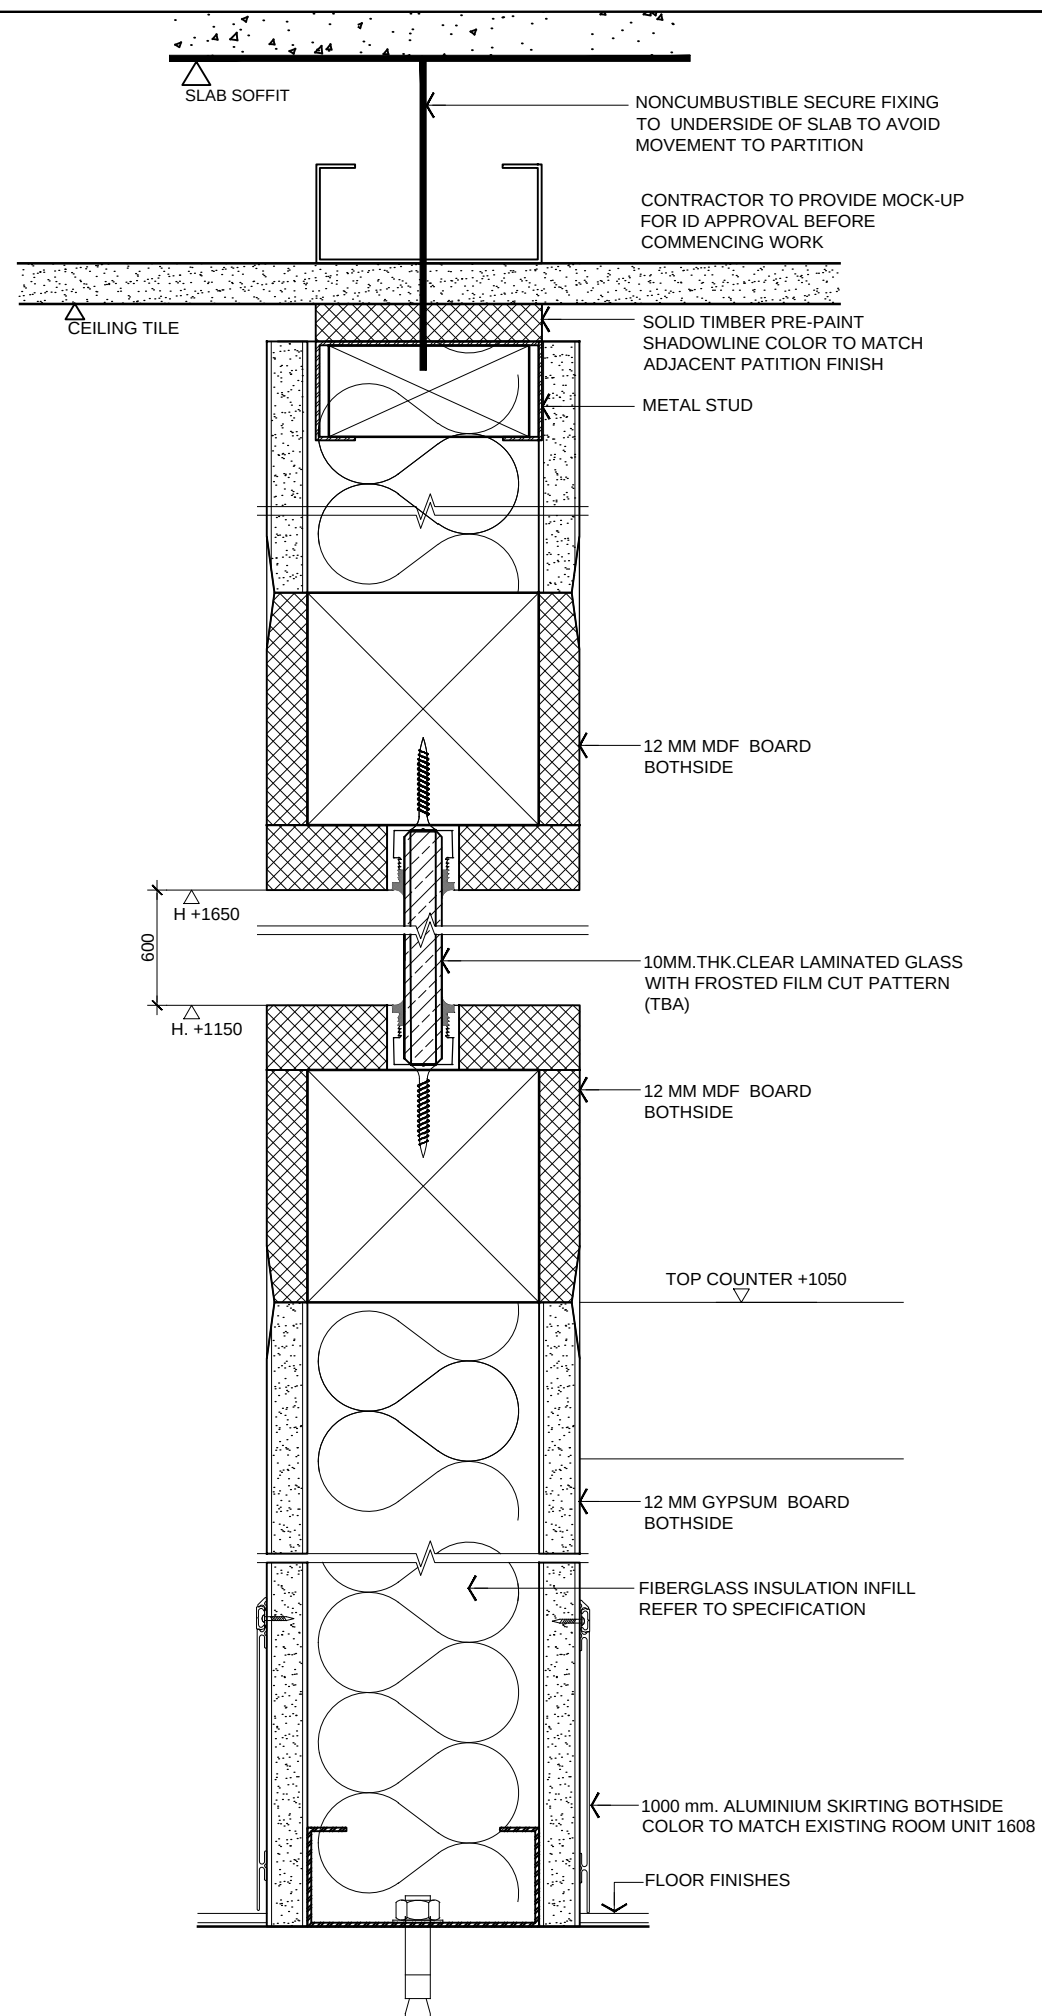

P4

DETAIL - DRYWALL PARTITION-SINGLE LAYER

Scale: N.T.S.

© LUX89 CO., LTD. April 2020

REFERENCE MAP

TH

NOTES

1. DO NOT SCALE DRAWINGS. WRITTEN DIMENSIONS GOVERN.
2. ALL DIMENSIONS ARE IN MILLIMETERS UNLESS NOTED OTHERWISE.
3. ALL DIMENSIONS SHALL BE VERIFIED ON SITE BEFORE PROCEEDING WITH THE WORK. LUX89 SHALL BE NOTIFIED IN WRITING OF ANY DISCREPANCIES.
4. THIS DRAWING MUST BE READ IN CONJUNCTION WITH ALL RELEVANT CONTRACTS, SPECIFICATIONS, REPORTS AND DRAWINGS.

© 2020 COPYRIGHT OF THIS DRAWING IS VESTED IN LUX89 CO., LTD.

THIS DRAWING IS AN UNCONTROLLED COPY. UNLESS NOTED OTHERWISE

[illegible]

CLIENT / PROJECT

**Tilleke & Gibbins
Myanmar Limited.**

PROJECT MANAGER & INTERIOR DESIGNER

LUX 89 CO., LTD.
7/89 Soi Rama 2 Soi 54/4, Samae Dam,
Bang Khun Thian, Bangkok, Thailand 10150
E LUX89.BKK@GMAIL.COM W LUX89.COM
T 66(2) 416 9189

ARCHITECTURE

STRUCTURE ENGINEER

M&E ENGINEER

ACCO ENGINEERING CO., LTD.
1213/430 Soi Ladprao94 (Panjamit) Plubpla, Wang Thonglang,
Bangkok, Thailand. 10310
E APISAK@ACCO.CO.TH **W** ACCO@ACCO.CO.TH
T 66(2) 559 0177-9, **F** 66 (2) 559 0176

DRAWING

PARTITION DETAILS


STATUS

FOR TENDER

SCALE AT 11 A3	DRAWN	CO-ORDINATED	CHECKED	PLOT DATE
1:100	AK	CP	CP	10/04/2020


JOB NO.	DRAWING NUMBER	REVISION
PTD 20.001	D-301	T1

CONTRACTOR TO SUBMIT SAMPLE FOR APPROVAL

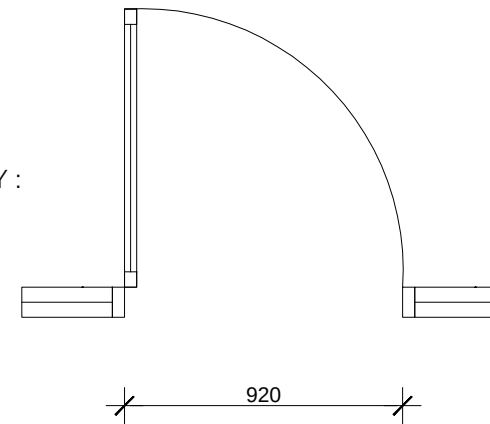


D1 PLAN - MAIN ENTRANCE PHASE 1

Scale: 1:25

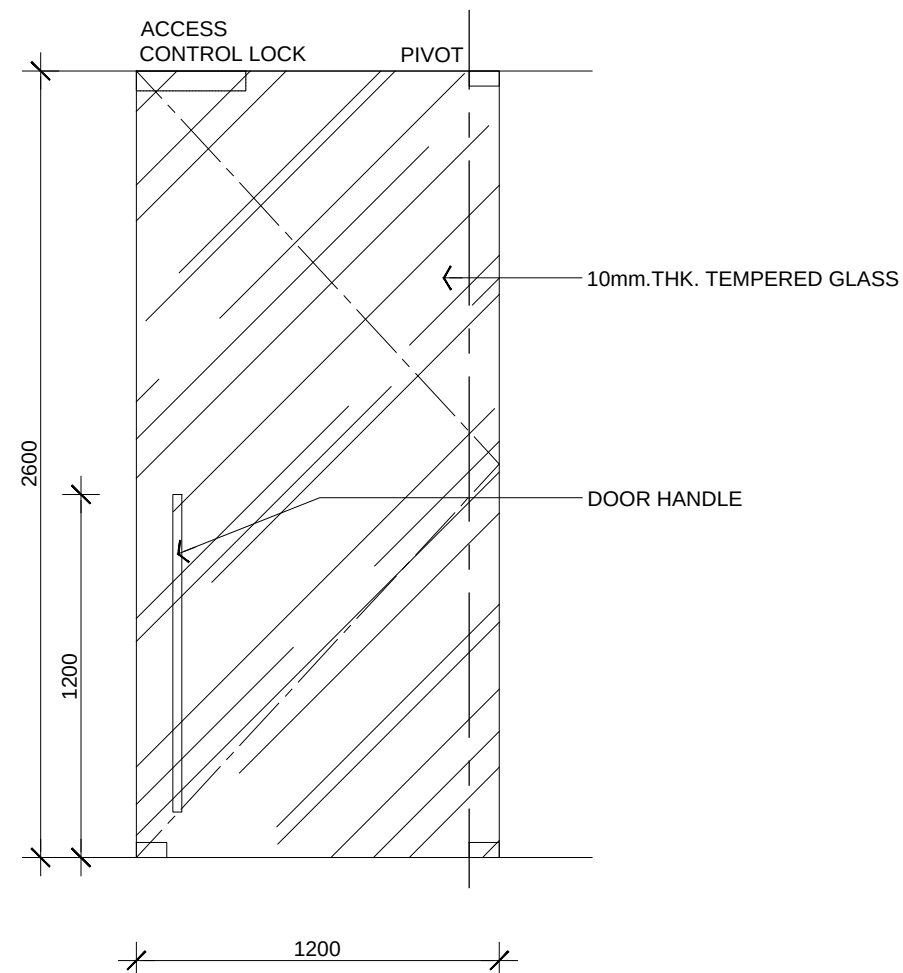

D1 **ELEVATION**
Scale: 1:25

D2 PLAN - GENERAL ROOM Scale: 1:25

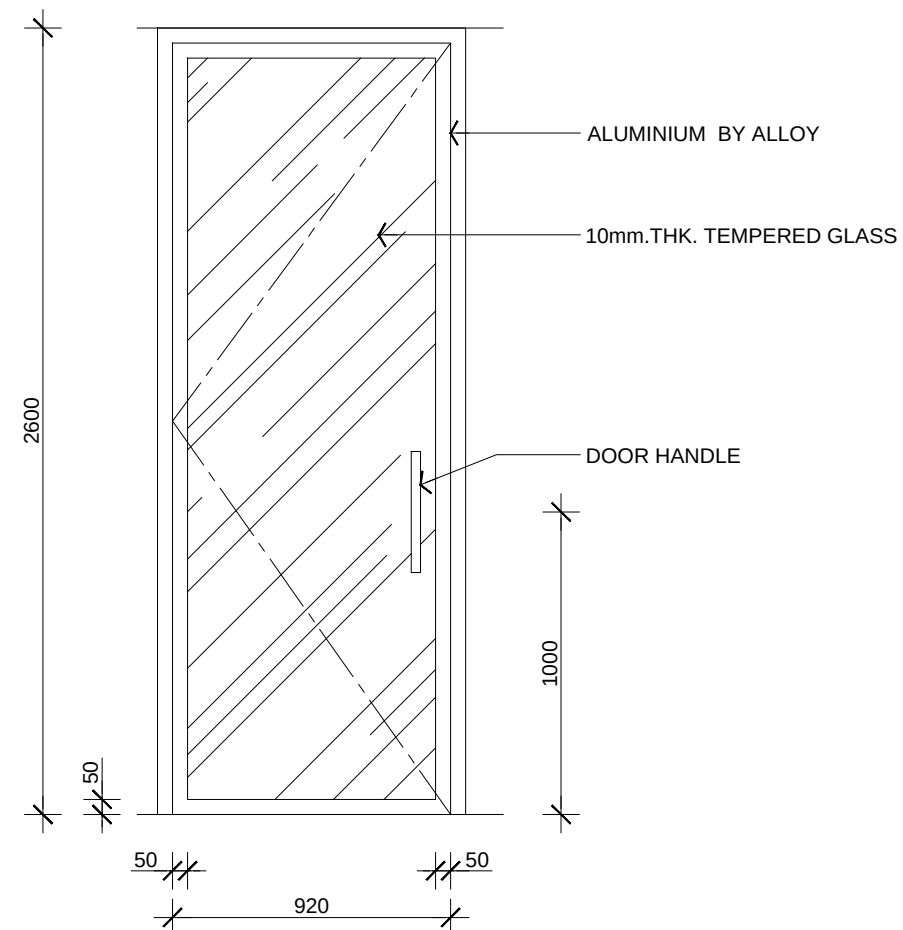

D2 **ELEVATION**
Scale: 1:25

REFERENCE MAP	NORTH

NOTES

1. DO NOT SCALE DRAWINGS. WRITTEN DIMENSIONS GOVERN.
2. ALL DIMENSIONS ARE IN MILLIMETERS UNLESS NOTED OTHERWISE.
3. ALL DIMENSIONS SHALL BE VERIFIED ON SITE BEFORE PROCEEDING WITH THE WORK. LUX89 SHALL BE NOTIFIED IN WRITING OF ANY DISCREPANCIES.
4. THIS DRAWING MUST BE READ IN CONJUNCTION WITH ALL RELEVANT CONTRACTS, SPECIFICATIONS, REPORTS AND DRAWINGS.

© 2020 COPYRIGHT OF THIS DRAWING IS VESTED IN LUX89 CO., LTD.

THIS DRAWING IS AN UNCONTROLLED COPY. UNLESS NOTED OTHERWISE

T1	CP	FOR TENDER	10/04/2020
REV	BY	DESCRIPTION	DATE

CLIENT / PROJECT

**Tilleke & Gibbins
Myanmar Limited.**

PROJECT MANAGER & INTERIOR DESIGNER

LUX 89 CO., LTD.
7/89 Soi Rama 2 Soi 54/4, Samae Dam,
Bang Khun Thian, Bangkok , Thailand 10150
E LUX89.BKK@GMAIL.COM W LUX89.COM
T 66(2) 416 9189

68 X01

ARCHITECTURE

STRUCTURE ENGINEER

M&E ENGINEER

ACCO ENGINEERING CO., LTD.
1213/430 Soi Ladprao94 (Panjarnit) Plubpla, Wang Thonglang,
Bangkok, Thailand. 10310
E APISAK@ACCO.CO.TH W ACCO@ACCO.CO.TH
T 66(2) 559 0177-9, F 66 (2) 559 0176

DRAFTING

DOOR ELEVATION

D1, D2

STATUS FOR TENDER

SCALE AT A1/A3	DRAWN	COORDINATED	CHECKED	PLT DATE
1 :25	AK	CP	CP	10/04/2020
JOB NO.	DRAWING NUMBER			REVISION
PTD 20.001	D400			T1

- ALL ALUMINUM FRAME AND HINGE BY ALLOY :
CONTACT BUNCHA 082 422 5699
- FITTING BY H'A'FELE :
CONTACT PRACHUAB MUIKHAM

A diagram of a horizontal beam of length 900 units. The beam is supported by two black rectangular blocks at its ends. A dimension line below the beam indicates the total length is 900. An arrow points to the right above the beam, indicating the direction of motion.

A diagram showing a quarter-circle arch. The arch is defined by a quarter-circle curve connecting two vertical lines. The horizontal distance between the base of these two vertical lines is labeled as 920. The vertical lines are represented by double lines, with the outer line being black and the inner line being white. The arch itself is a thin black curve. The overall shape is a quarter-circle with a radius of 920.

Technical drawing of a quarter-circle arch. The arch is defined by a quarter-circle curve with a radius of 900 units. The total width of the base is 1000 units, and the total height is 950 units. The base consists of a 50-unit wide section on the left and a 50-unit wide section on the right, with a 900-unit wide section in the middle. The height is composed of a 900-unit vertical section and a 50-unit horizontal section at the top. The drawing includes dimension lines and arrows indicating these measurements.

Technical drawing of a sliding door assembly. The drawing shows a vertical rectangular door with diagonal hatching, indicating it is made of 10mm thick tempered glass. The door is mounted on a sliding track at the top. The door handle is located on the left side. Dimensions are provided: the total height is 2600, the total width is 900, and the door width is 50. The door is labeled "SLIDING DOOR". The track is labeled "SLIDING TRACK". The door frame is labeled "ALUMINIUM BY ALLOY". The glass is labeled "10mm.THK. TEMPERED GLASS". The handle is labeled "DOOR HANDLE".

Technical drawing of a door assembly. The drawing shows a vertical door with a diagonal hatching pattern. The door is framed by an aluminium alloy. The glass is 10mm thick tempered glass. A door handle is shown on the left side. Dimensions are indicated: overall height is 2600, height of the glass panel is 1000, overall width is 920, and the width of the aluminium frame on each side is 25.

Labels and dimensions:

- 2600 (Overall height)
- 1000 (Glass panel height)
- 920 (Overall width)
- 25 (Aluminium frame width on each side)
- ALUMINIUM BY ALLOY
- 10mm.THK. TEMPERED GLASS
- DOOR HANDLE


Technical drawing of a door assembly. The drawing shows a vertical door with a diagonal dashed line indicating a split or hinge line. The door is labeled with a triangle containing the text "LA2". The door is shown within a frame. Dimensions are provided for the door and the frame. The door height is 2600, and the door width is 900. The frame width is 1000, with 50 units on each side. The door handle is located at a height of 1000 from the bottom. The door is labeled "ALUMINIUM BY ALLOY" and "SOLID DOOR PANEL". The door handle is labeled "DOOR HANDLE".

REFERENCE MAP		NORTH	
NOTES 1. DO NOT SCALE DRAWINGS. WRITTEN DIMENSIONS GOVERN. 2. ALL DIMENSIONS ARE IN MILLIMETERS UNLESS NOTED OTHERWISE. 3. ALL DIMENSIONS SHALL BE VERIFIED ON SITE BEFORE PROCEEDING WITH THE WORK. LUX89 SHALL BE NOTIFIED IN WRITING OF ANY DISCREPANCIES. 4. THIS DRAWING MUST BE READ IN CONJUNCTION WITH ALL RELEVANT CONTRACTS, SPECIFICATIONS, REPORTS AND DRAWINGS.	
© 2020 COPYRIGHT OF THIS DESIGN IS VESTED IN LUX89 CO., LTD.	
THIS DRAWING IS AN UNCONTROLLED COPY. UNLESS NOTED OTHERWISE	
<table><tr><td></td><td></td><td></td><td></td></tr><tr><td></td><td></td><td></td><td></td></tr><tr><td></td><td></td><td></td><td></td></tr><tr><td></td><td></td><td></td><td></td></tr><tr><td></td><td></td><td></td><td></td></tr><tr><td></td><td></td><td></td><td></td></tr><tr><td></td><td></td><td></td><td></td></tr><tr><td></td><td></td><td></td><td></td></tr><tr><td></td><td></td><td></td><td></td></tr><tr><td></td><td></td><td></td><td></td></tr><tr><td></td><td></td><td></td><td></td></tr><tr><td></td><td></td><td></td><td></td></tr><tr><td></td><td></td><td></td><td></td></tr><tr><td></td><td></td><td></td><td></td></tr><tr><td>T1</td><td>CP</td><td>FOR TENDER</td><td>10/04/2020</td></tr><tr><td>REV</td><td>BY</td><td>DESCRIPTION</td><td>DATE</td></tr></table>	T1	CP	FOR TENDER	10/04/2020	REV	BY	DESCRIPTION	DATE
T1	CP	FOR TENDER	10/04/2020	
REV	BY	DESCRIPTION	DATE	
CLIENT / PROJECT Tilleke & Gibbins Myanmar Limited. LUX 89	
PROJECT MANAGER & INTERIOR DESIGNER LUX 89 CO., LTD. 7/89 Soi Rama 2 Soi 54/4,Samae Dam, Bang Khun Thian, Bangkok , Thailand10150 E LUX89.BKK@GMAIL.COM W LUX89.COM T 66(2) 416 9189	
ARCHITECTURE	
STRUCTURE ENGINEER	
M&E ENGINEER ACCO ENGINEERING CO., LTD. 1213/430 Soi Ladprao94 (Panjamit) Plubpla, Wang Thonglang, Bangkok, Thailand. 10310 E APISAK@ACCO.CO.TH W ACCO@ACCO.CO.TH T 66(2) 559 0177-9, F 66 (2) 559 0176	
DRAWING DOOR ELEVATION D3, D4, D5	
STATUS FOR TENDER	
SCALE AT A4 A3	DRAWN	CHECKED	PLOTTED	
1 : 25	AK	CP	10/04/2020	
JOB NO.	DRAWING NUMBER	REVISION	
PTD 20.001	D401	T1	


NOTE

- ALL ALUMINUM FRAME AND HINGE BY ALLOY :
CONTACT BUNCHA 082 422 5699
- FITTING BY H'A'FELE :
CONTACT PRACHUAB MUIKHAM


CONTRACTOR TO SUBMIT SAMPLE FOR APPROVAL

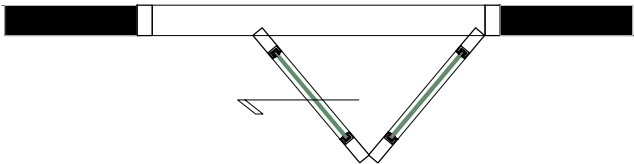


D6 PLAN
Scale: 1:25

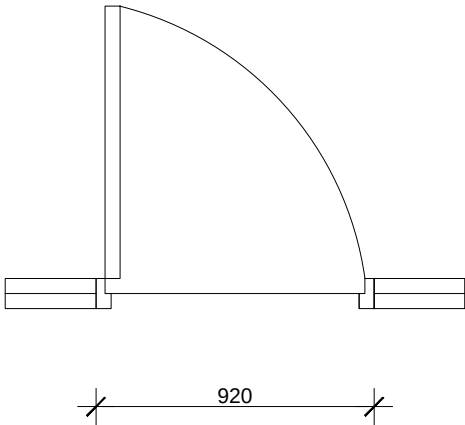


D7 PLAN
Scale: 1:25

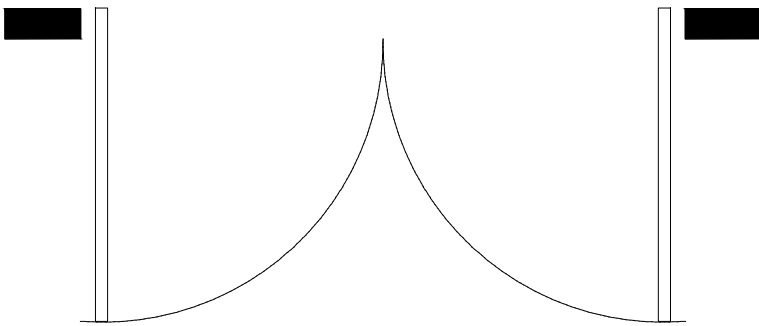


D8 PLAN - MAIN ENTRANCE PHASE 2
Scale: 1:25

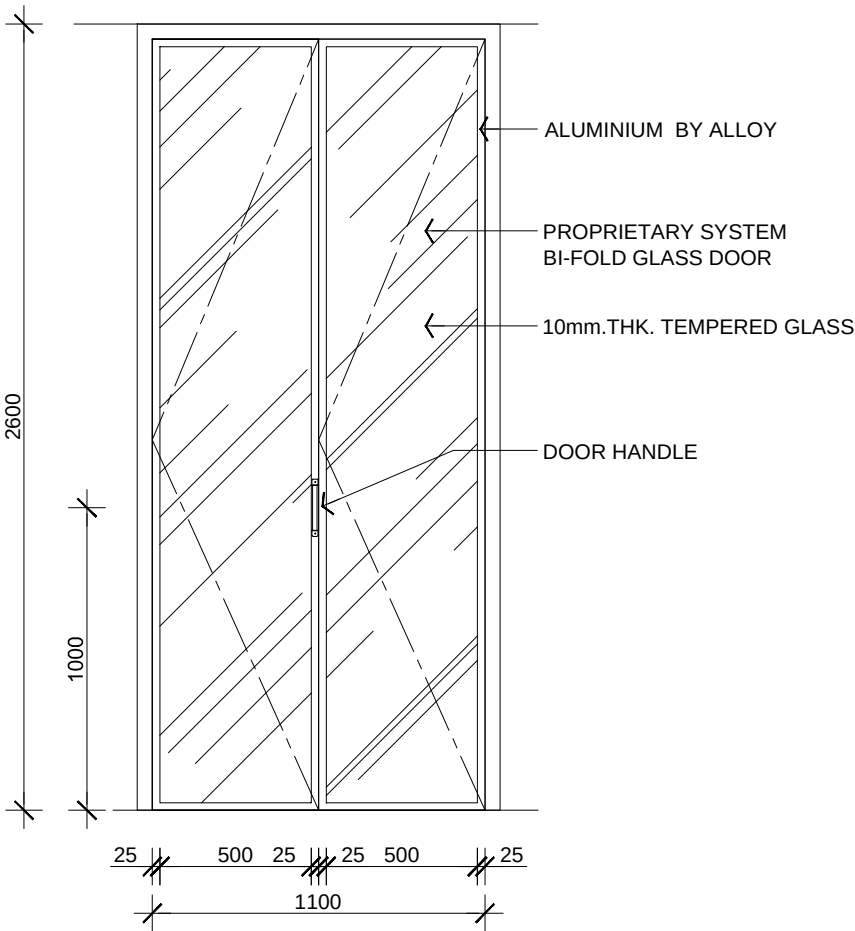


D6 ELEVATION
Scale: 1:25

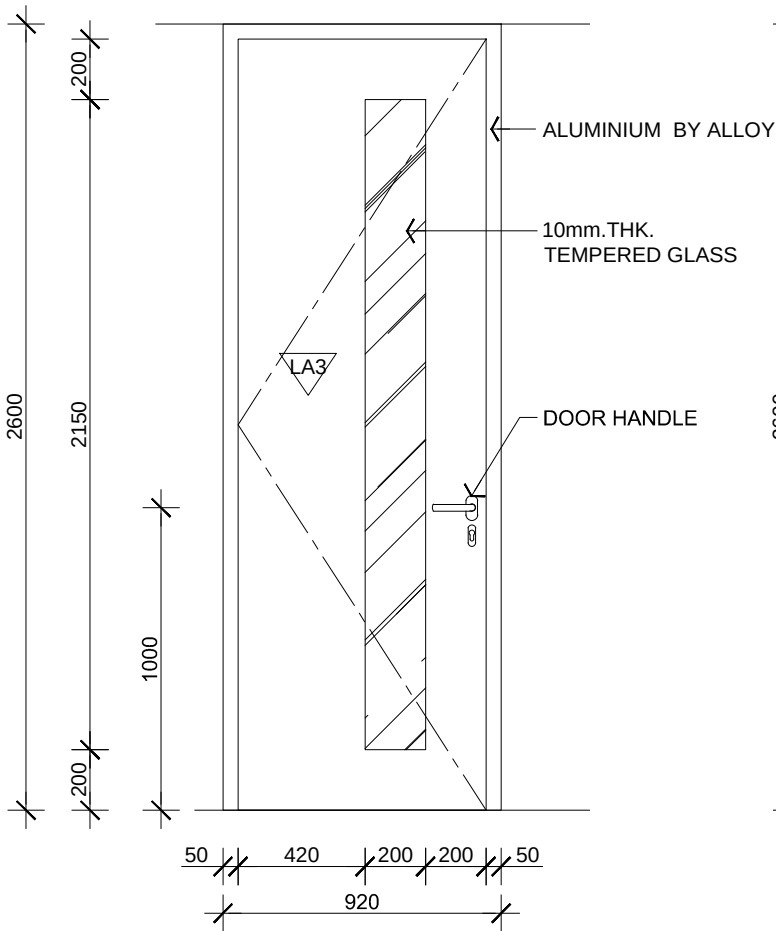

D7 ELEVATION
Scale: 1:25

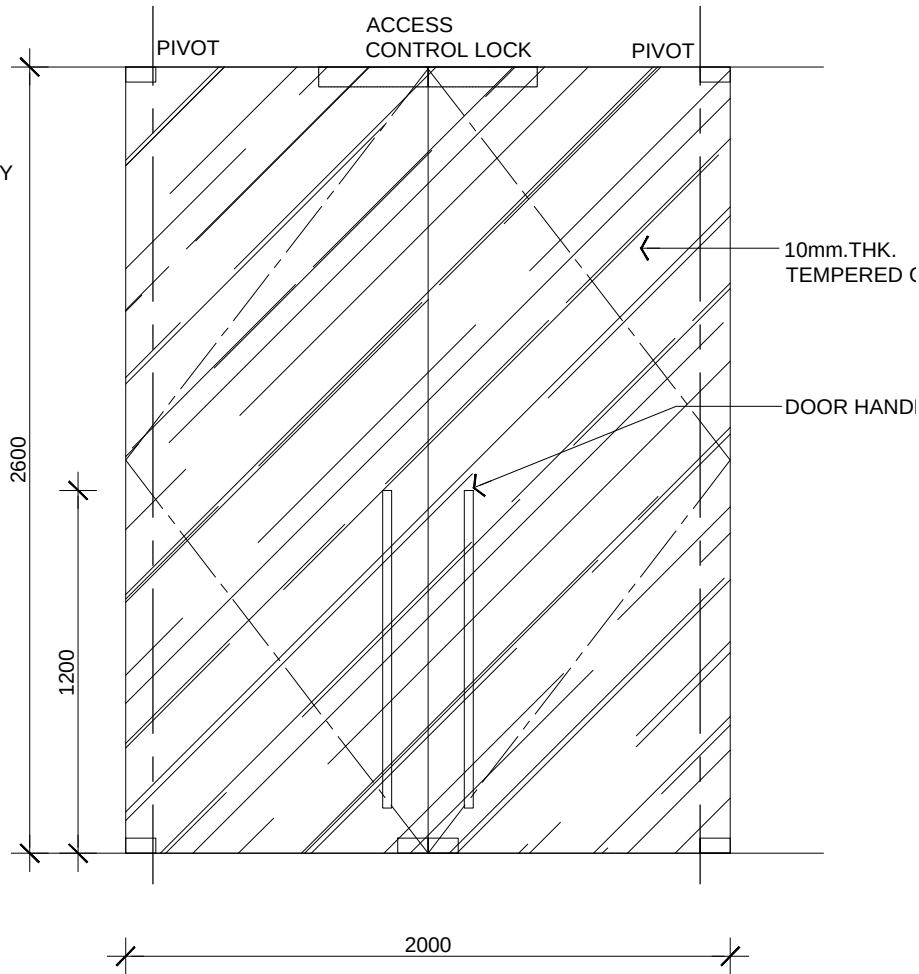

D1 ELEVATION
Scale: 1:25

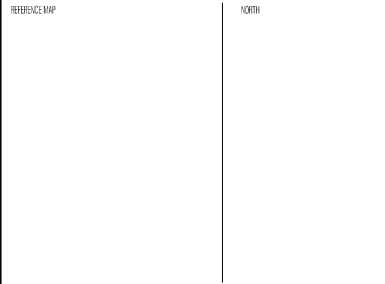

NOTES
1. DO NOT SCALE DRAWINGS. WRITTEN DIMENSIONS GOVERN.
2. ALL DIMENSIONS ARE IN MILLIMETERS UNLESS NOTED OTHERWISE.
3. ALL DIMENSIONS SHALL BE VERIFIED ON SITE BEFORE PROCEEDING WITH THE WORK. LUX89 SHALL BE NOTIFIED IN WRITING OF ANY DISCREPANCIES.
4. THIS DRAWING MUST BE READ IN CONJUNCTION WITH ALL RELEVANT CONTRACTS, SPECIFICATIONS, REPORTS AND DRAWINGS.

© 2020 COPYRIGHT OF THIS DRAWING IS VESTED IN LUX89 CO., LTD.

THIS DRAWING IS AN UNCONTROLLED COPY, UNLESS NOTED OTHERWISE

REV	BY	DESCRIPTION	DATE
T1	CP	FOR TENDER	10/04/2020

CLIENT / PROJECT

**Tilleke & Gibbins
Myanmar Limited.**

PROJECT MANAGER & INTERIOR DESIGNER

LUX 89 CO., LTD.
7/89 Soi Rama 2 Soi 54/4 Samae Dam,
Bang Khun Thian, Bangkok, Thailand 10150
E LUX89.BKK@GMAIL.COM W LUX89.COM
T 66(2) 416 9189

ARCHITECTURE

STRUCTURE ENGINEER

M&E ENGINEER

ACCO ENGINEERING CO., LTD.
1213/430 Soi Ladprao94 (Panjamit) Plubpla, Wang Thonglang,
Bangkok, Thailand. 10310
E APISAK@ACCO.CO.TH W ACCO@ACCO.CO.TH
T 66(2) 559 0177-9, F 66 (2) 559 0176

DRAWING


**DOOR ELEVATION
D6, D7, D8**


FOR TENDER

SCALE AT A1/A3	DRAWN	CO-ORDINATED	CHECKED	PLT/DATE
1:25	AK	CP	CP	10/04/2020
JOB NO.	DRAWING NUMBER			REVISION
PTD 20.001	D402			T1



JCB NO.	DRAWING NUMBER	REVISION
PTD 20.001	D-802	T1

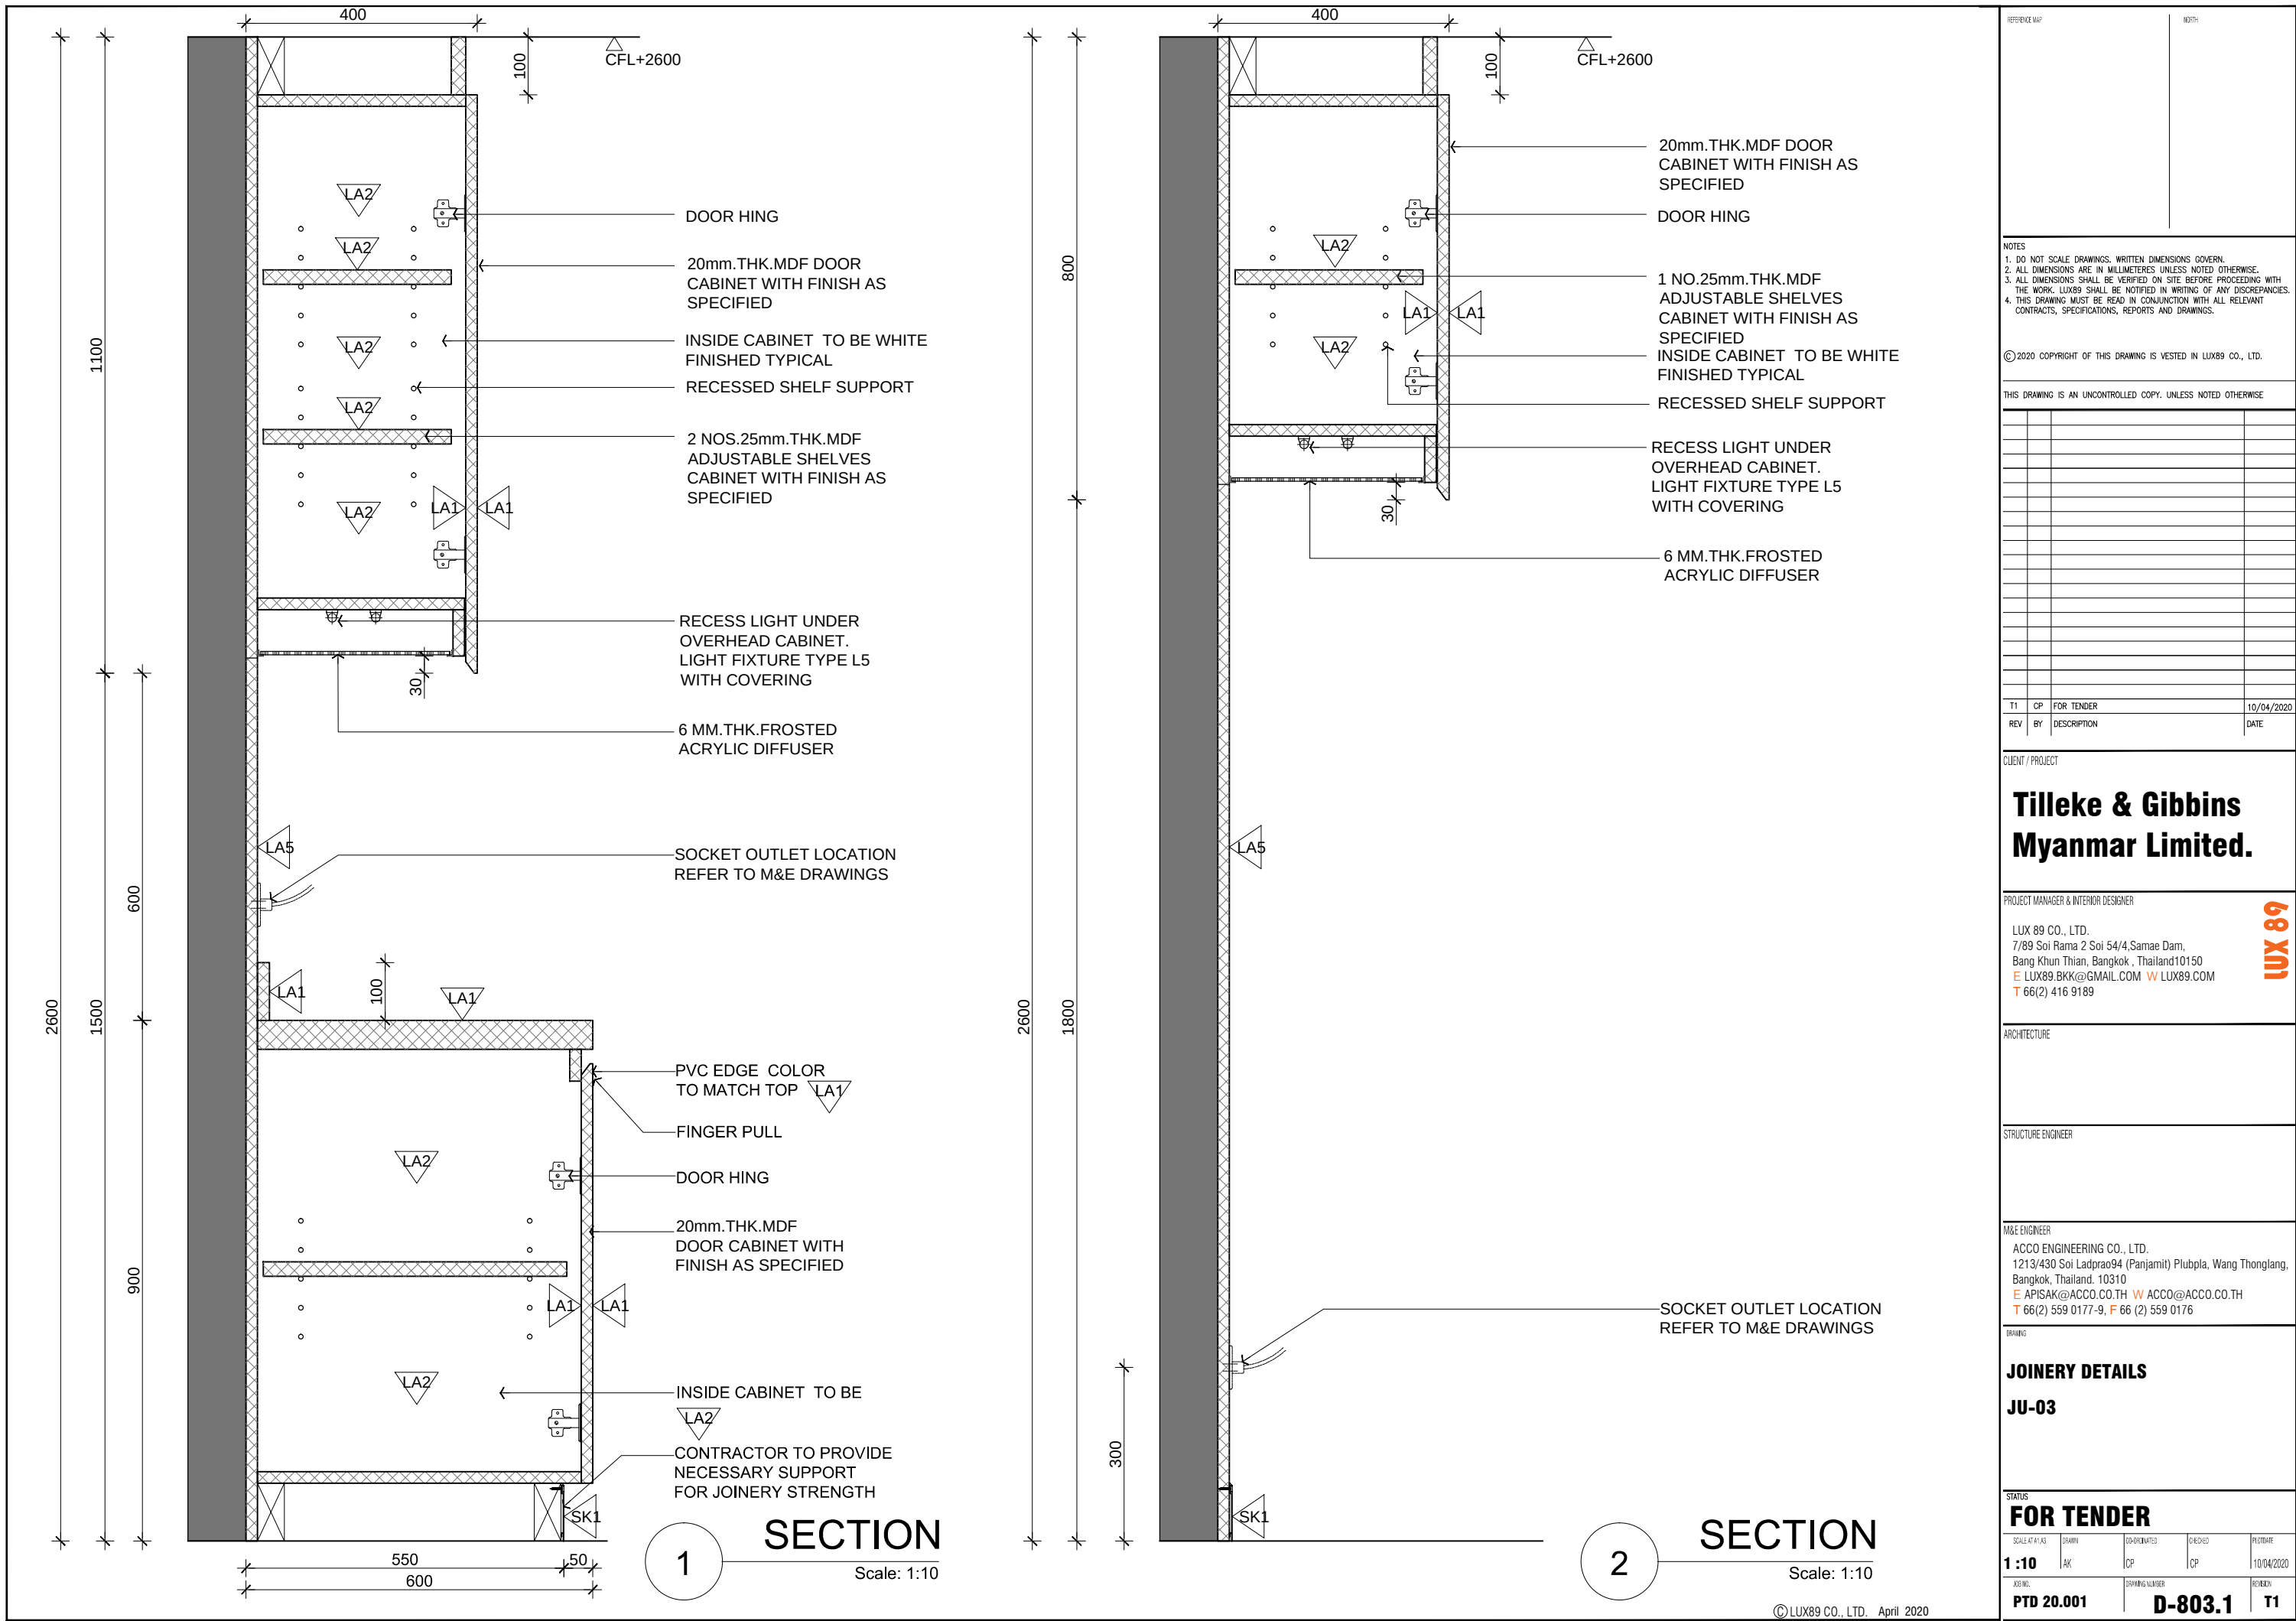

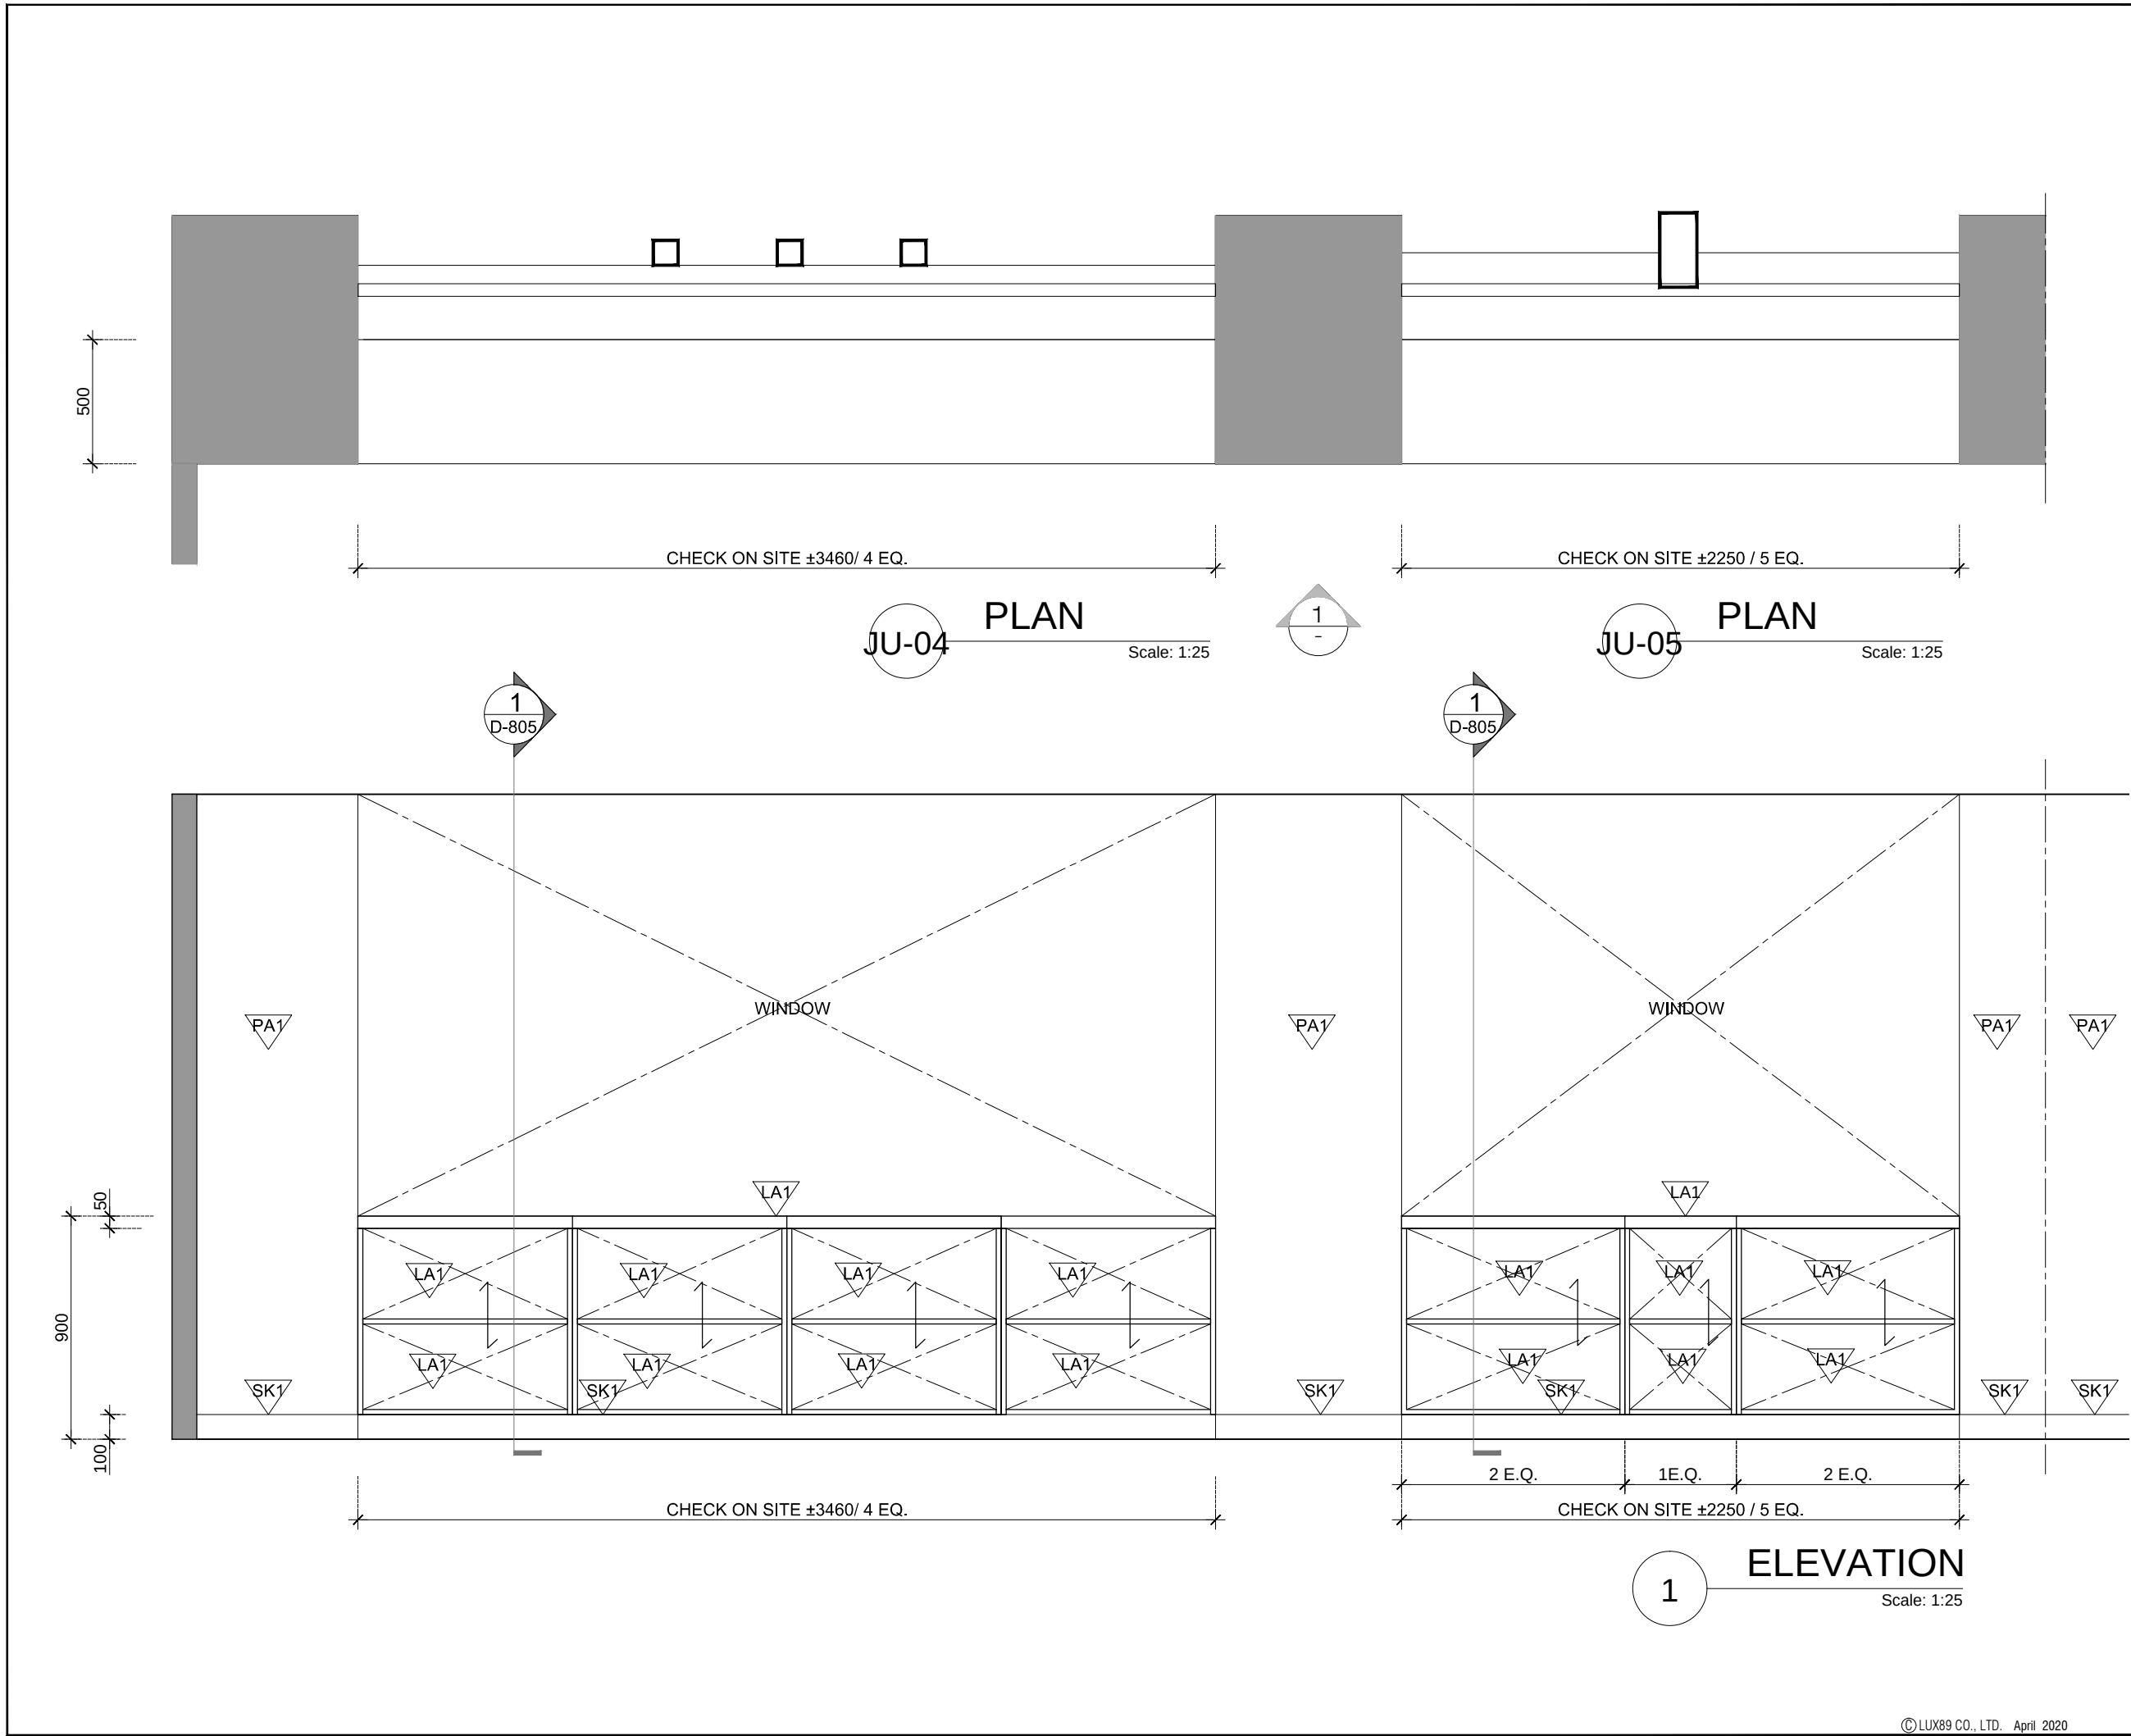

REFERENCE MAP

NORTH

NOTES

1. DO NOT SCALE DRAWINGS. WRITTEN DIMENSIONS GOVERN.

2. ALL DIMENSIONS ARE IN MILLIMETERS UNLESS NOTED OTHERWISE.

3. ALL DIMENSIONS SHALL BE VERIFIED ON SITE BEFORE PROCEEDING WITH THE WORK. LUX89 SHALL BE NOTIFIED IN WRITING OF ANY DISCREPANCIES.

4. THIS DRAWING MUST BE READ IN CONJUNCTION WITH ALL RELEVANT CONTRACTS, SPECIFICATIONS, REPORTS AND DRAWINGS.

© 2020 COPYRIGHT OF THIS DRAWING IS VESTED IN LUX89 CO., LTD.

THIS DRAWING IS AN UNCONTROLLED COPY, UNLESS NOTED OTHERWISE

T1	CP	FOR TENDER	10/04/2020
REV	BY	DESCRIPTION	DATE

CLIENT / PROJECT

Tilleke & Gibbins
Myanmar Limited.

PROJECT MANAGER & INTERIOR DESIGNER

LUX 89 CO., LTD.

7/89 Soi Rama 2 Soi 54/4 Samae Dam,
Bangkok, Thailand. 10310

E LUX89.BKK@GMAIL.COM W LUX89.COM

T 66(2) 416 9189

ARCHITECTURE

STRUCTURE ENGINEER

M&E ENGINEER

ACCO ENGINEERING CO., LTD.

1213/430 Soi Ladprao94 (Panjamit) Plubpla, Wang Thonglang,
Bangkok, Thailand. 10310

E APISAK@ACCO.CO.TH W ACCO@ACCO.CO.TH

T 66(2) 559 0177-9, F 66 (2) 559 0176

DRAWING

JOINERY DETAILS


JU-04, JU-05


STATUS

FOR TENDER



SCALE AT A3	DRAWN	CHECKED	DATE
1:25	AK	CP	10/04/2020

JOB NO.	DRAWING NUMBER	REVISION
PTD 20.001	D-804	T1

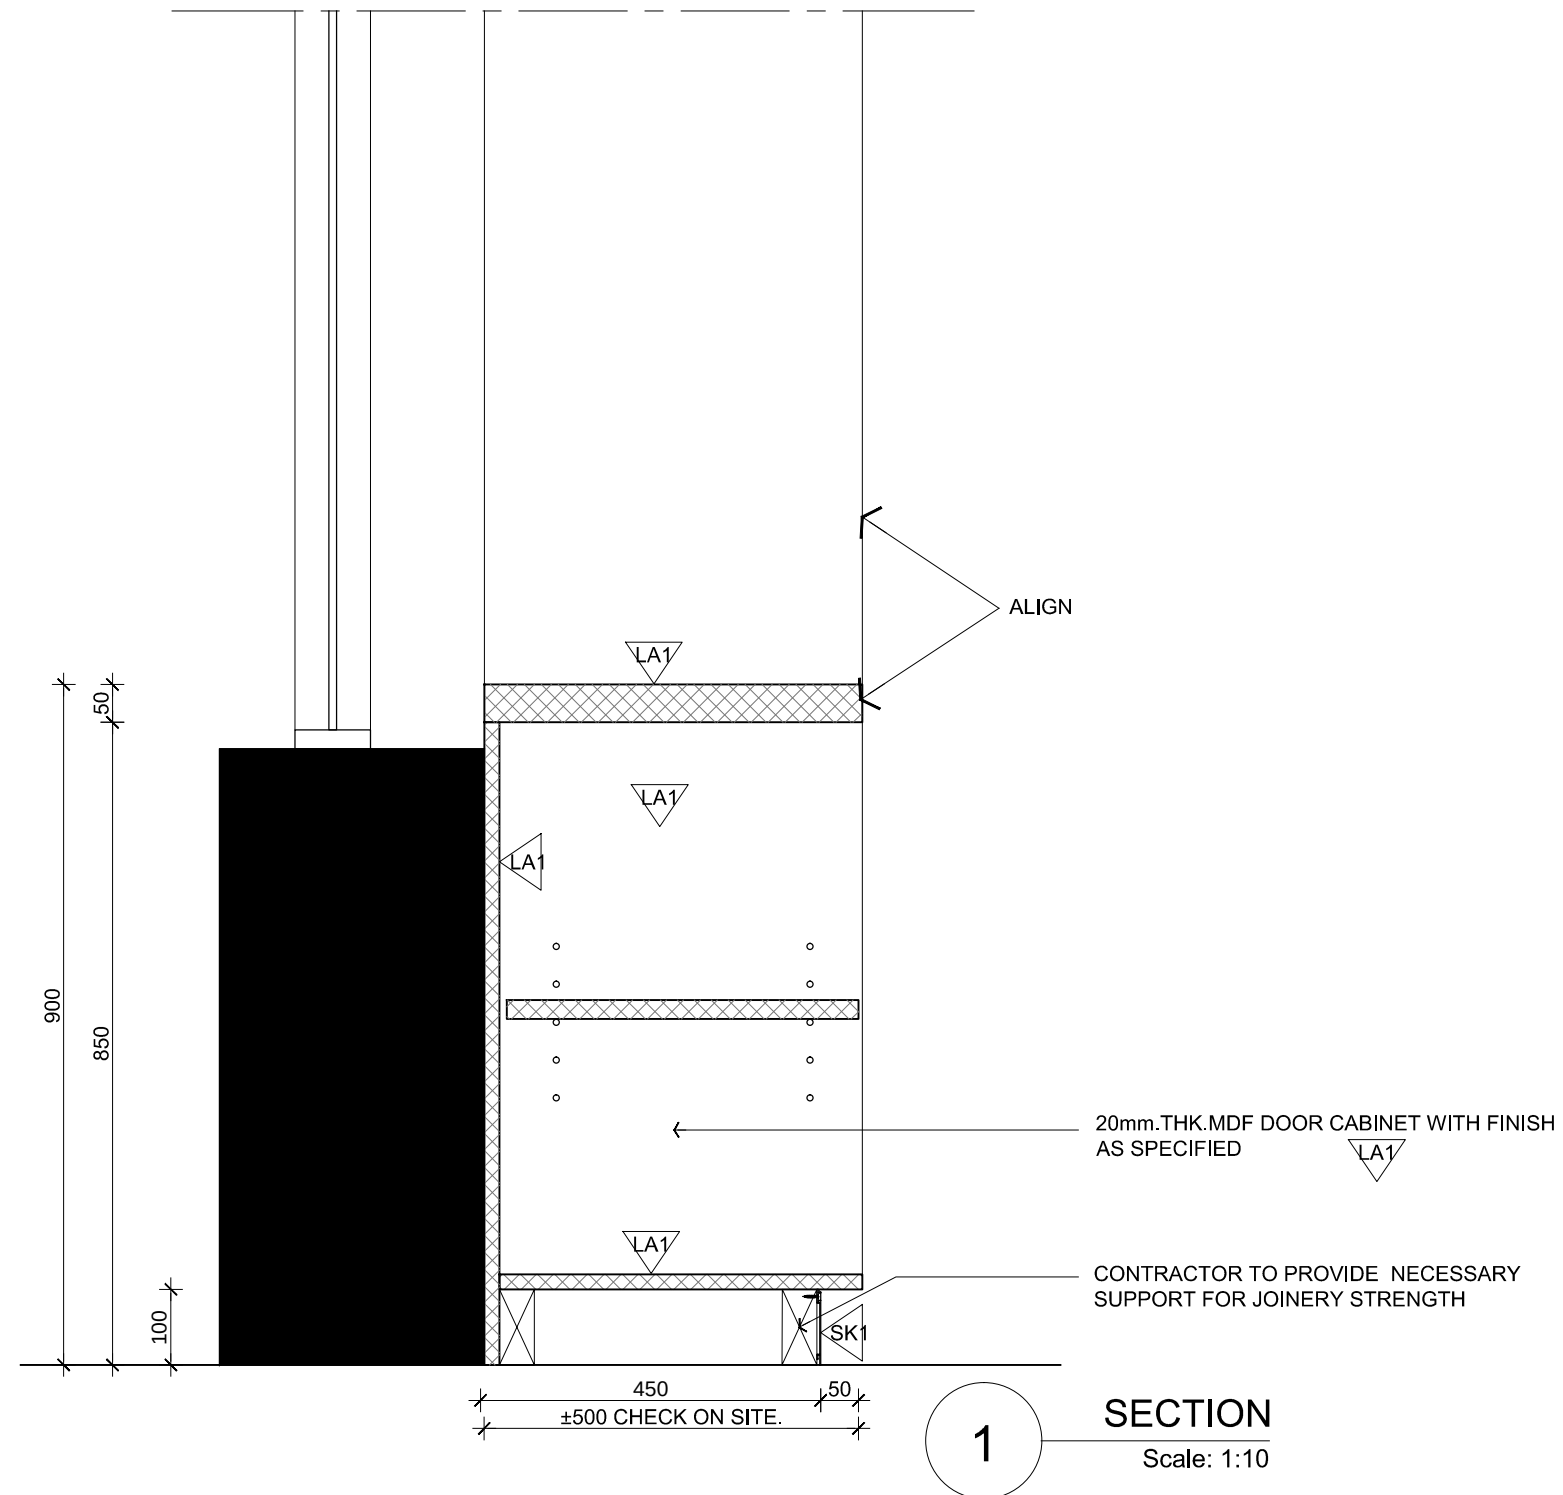


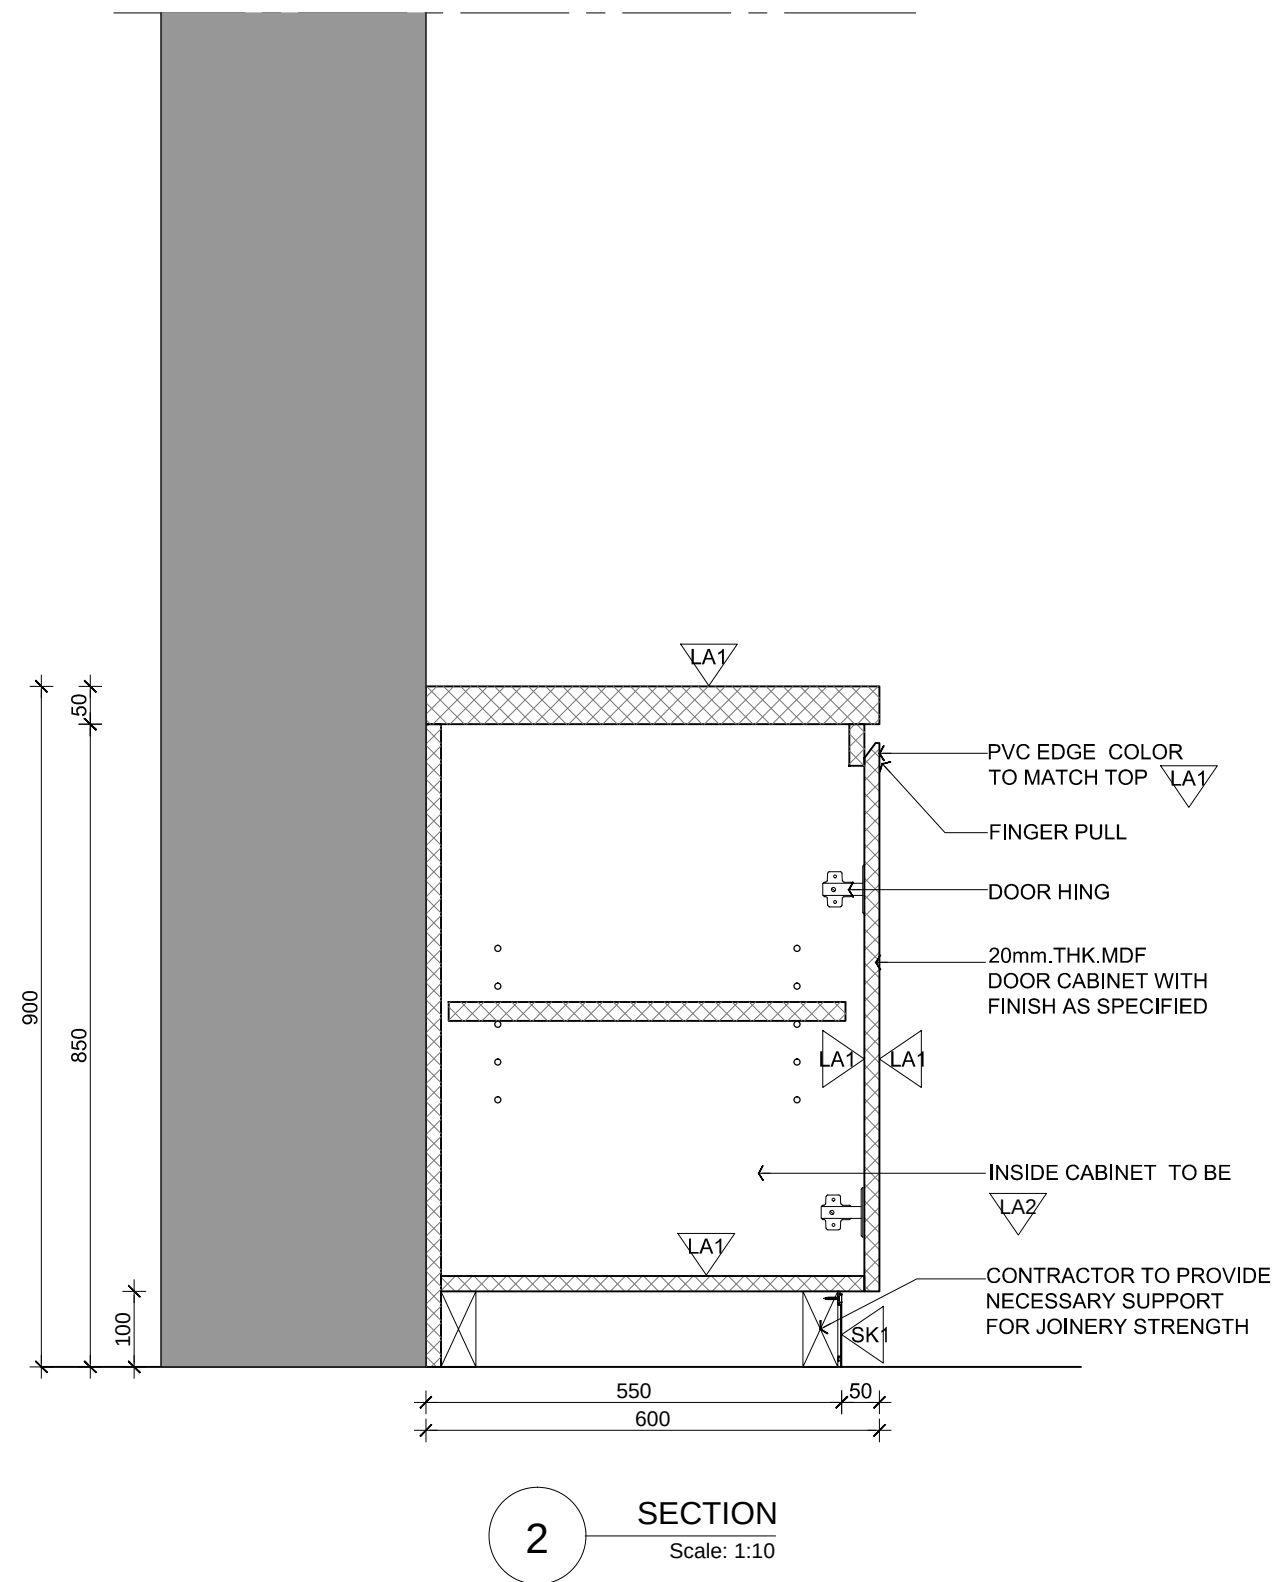


JOB NO. PTD 20.001	DRAWING NUMBER D-807	REVISION T1
------------------------------	--------------------------------	-----------------------

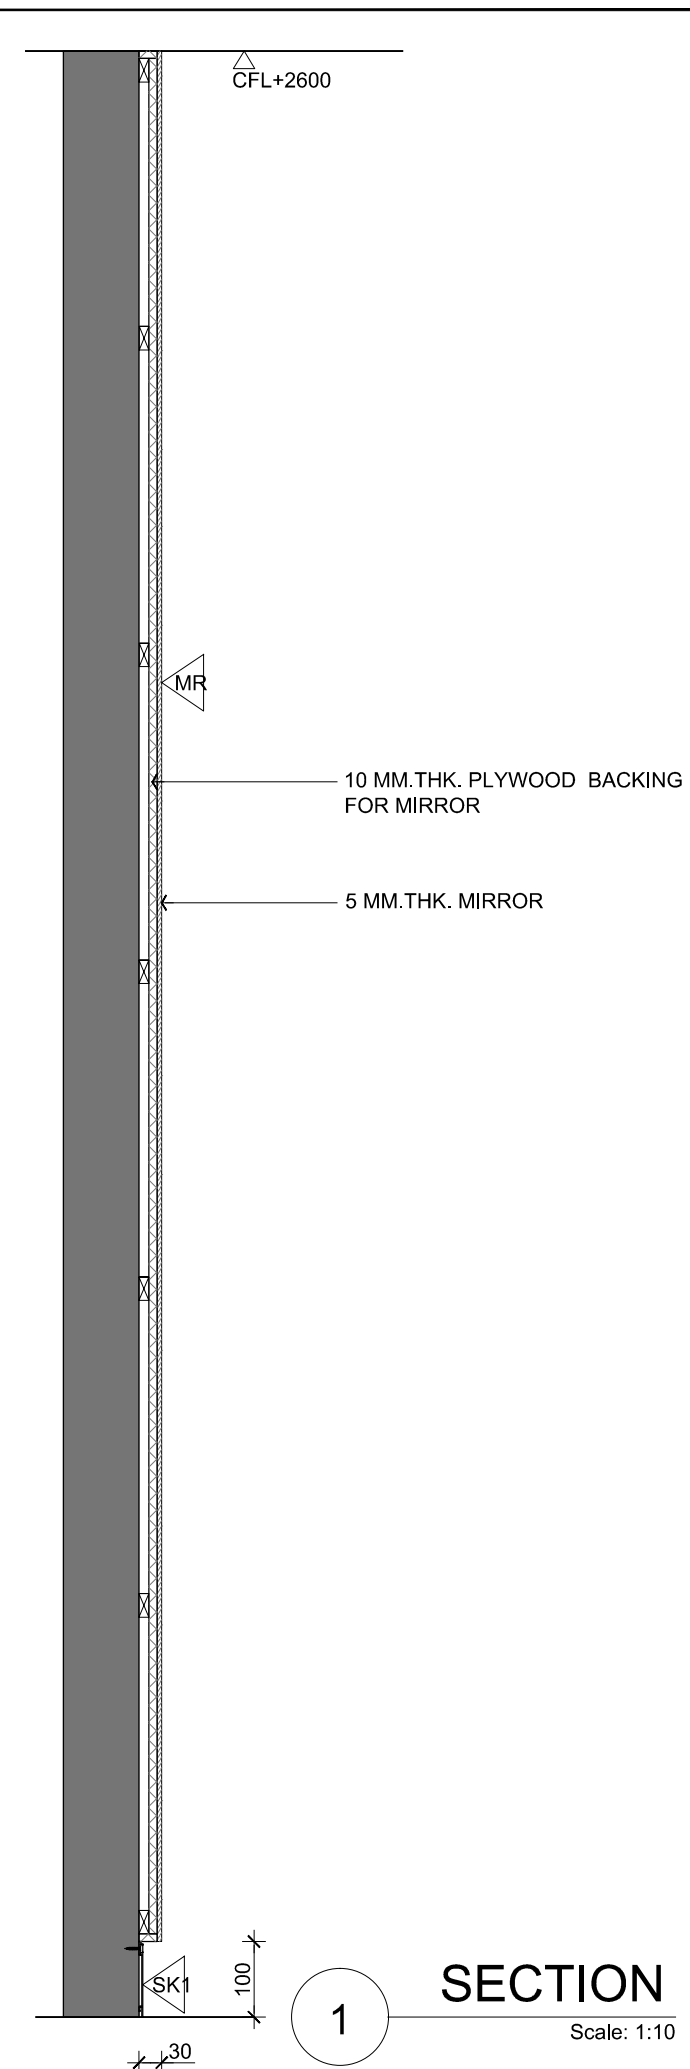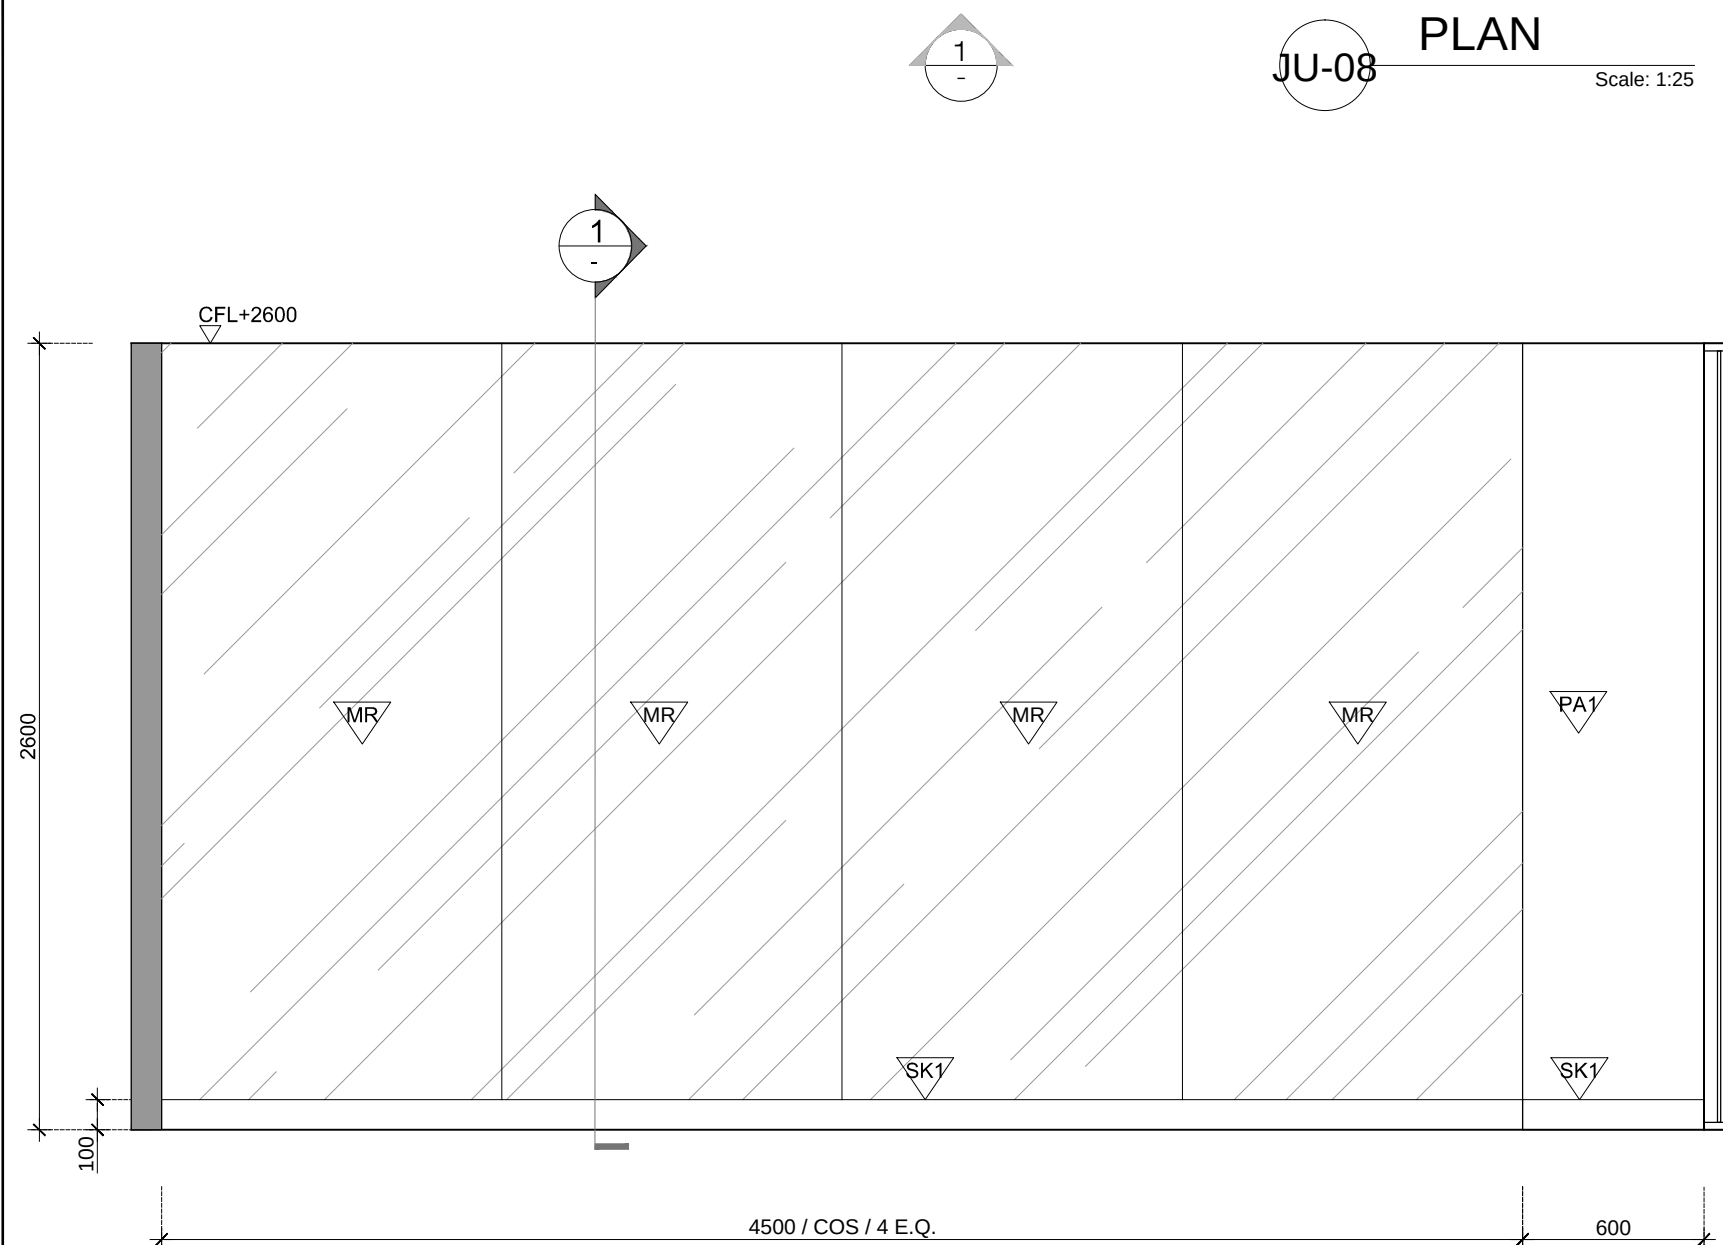


REFERENCE MAP		NORTH	
NOTES 1. DO NOT SCALE DRAWINGS. WRITTEN DIMENSIONS GOVERN. 2. ALL DIMENSIONS ARE IN MILLIMETERS UNLESS NOTED OTHERWISE. 3. ALL DIMENSIONS SHALL BE VERIFIED ON SITE BEFORE PROCEEDING WITH THE WORK. LUX89 SHALL BE NOTIFIED IN WRITING OF ANY DISCREPANCIES. 4. THIS DRAWING MUST BE READ IN CONJUNCTION WITH ALL RELEVANT CONTRACTS, SPECIFICATIONS, REPORTS AND DRAWINGS.			
© 2020 COPYRIGHT OF THIS DRAWING IS VESTED IN LUX89 CO., LTD.			
THIS DRAWING IS AN UNCONTROLLED COPY. UNLESS NOTED OTHERWISE			
T1	CP	FOR TENDER	10/04/2020
REV	BY	DESCRIPTION	DATE
CLIENT / PROJECT			
Tilleke & Gibbins Myanmar Limited.			
PROJECT MANAGER & INTERIOR DESIGNER			
LUX 89 CO., LTD. 7/89 Soi Rama 2 Soi 54/4,Samae Dam, Bang Khun Thian, Bangkok , Thailand10150 E LUX89.BKK@GMAIL.COM W LUX89.COM T 66(2) 416 9189			
ARCHITECTURE			
STRUCTURE ENGINEER			
M&E ENGINEER			
ACCO ENGINEERING CO., LTD. 1213/430 Soi Ladpraø94 (Panjarnit) Plubpla, Wang Thonglang, Bangkok, Thailand. 10310 E APISAK@ACCO.CO.TH W ACCO@ACCO.CO.TH T 66(2) 559 0177-9, F 66 (2) 559 0176			
DRAWING			
JOINERY DETAILS JU-08			
STATUS			
FOR TENDER			
SCALE 1:1 AS SHOWN	CO-DRAWN	CHECKED	PLOTTED
1 :25.10 AK	CP	CP	10/04/2020
JOB NO. PTD 20.001	DRAWING NUMBER D-808	REVISION T1	

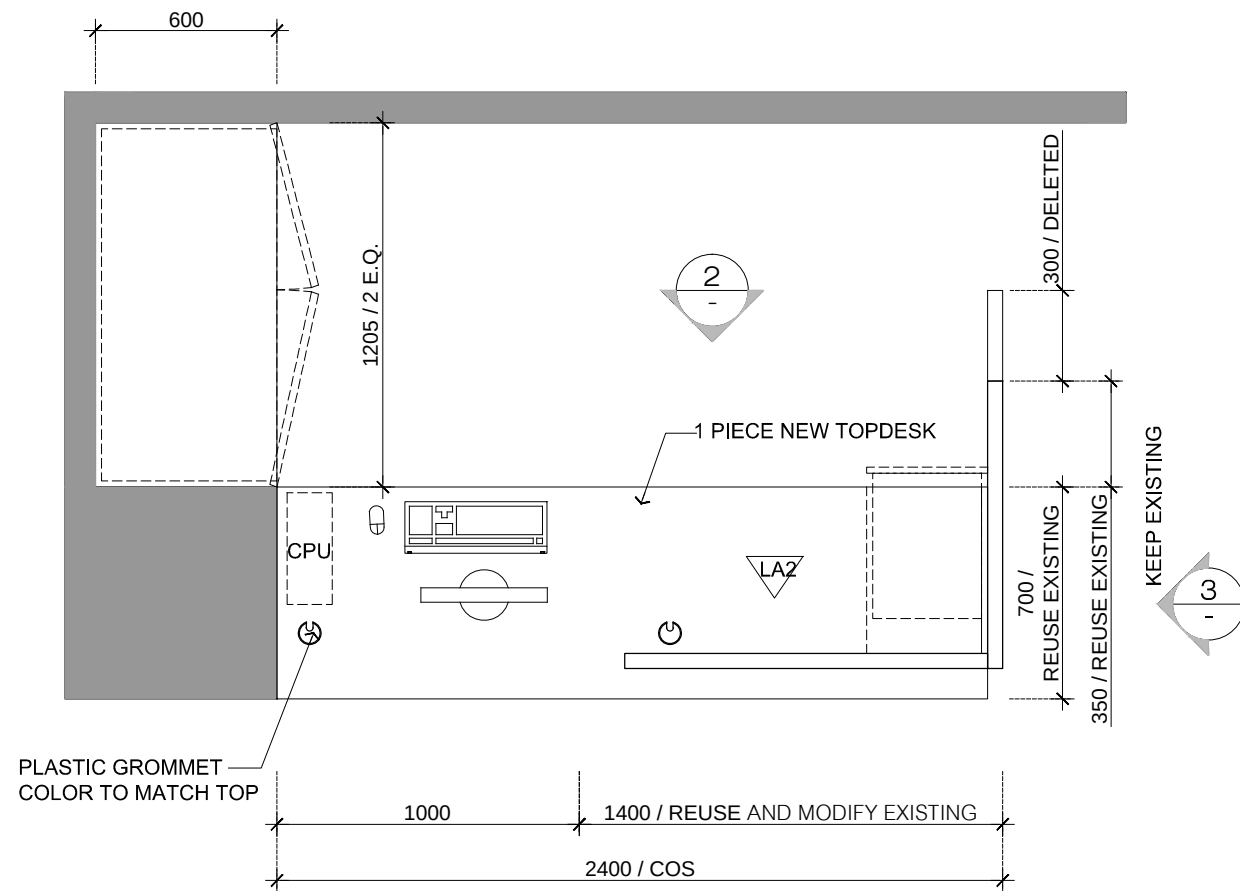


PLAN
Scale: 1:25
JU-09

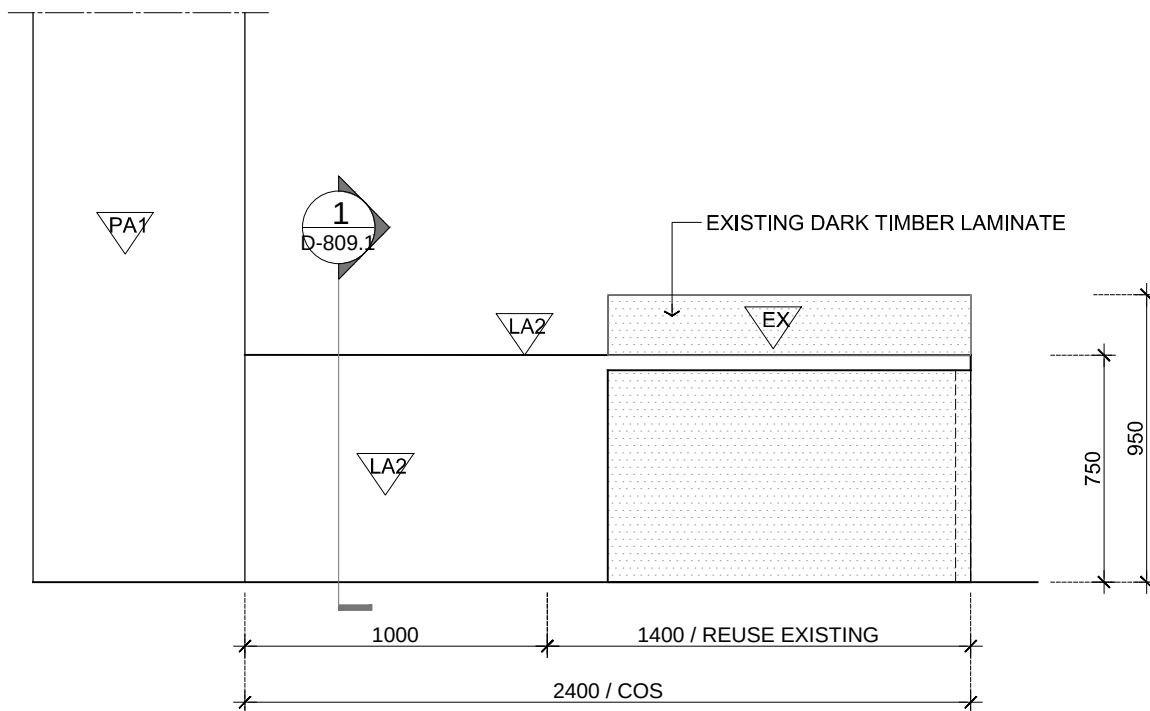

ELEVATION 1
Scale: 1:25

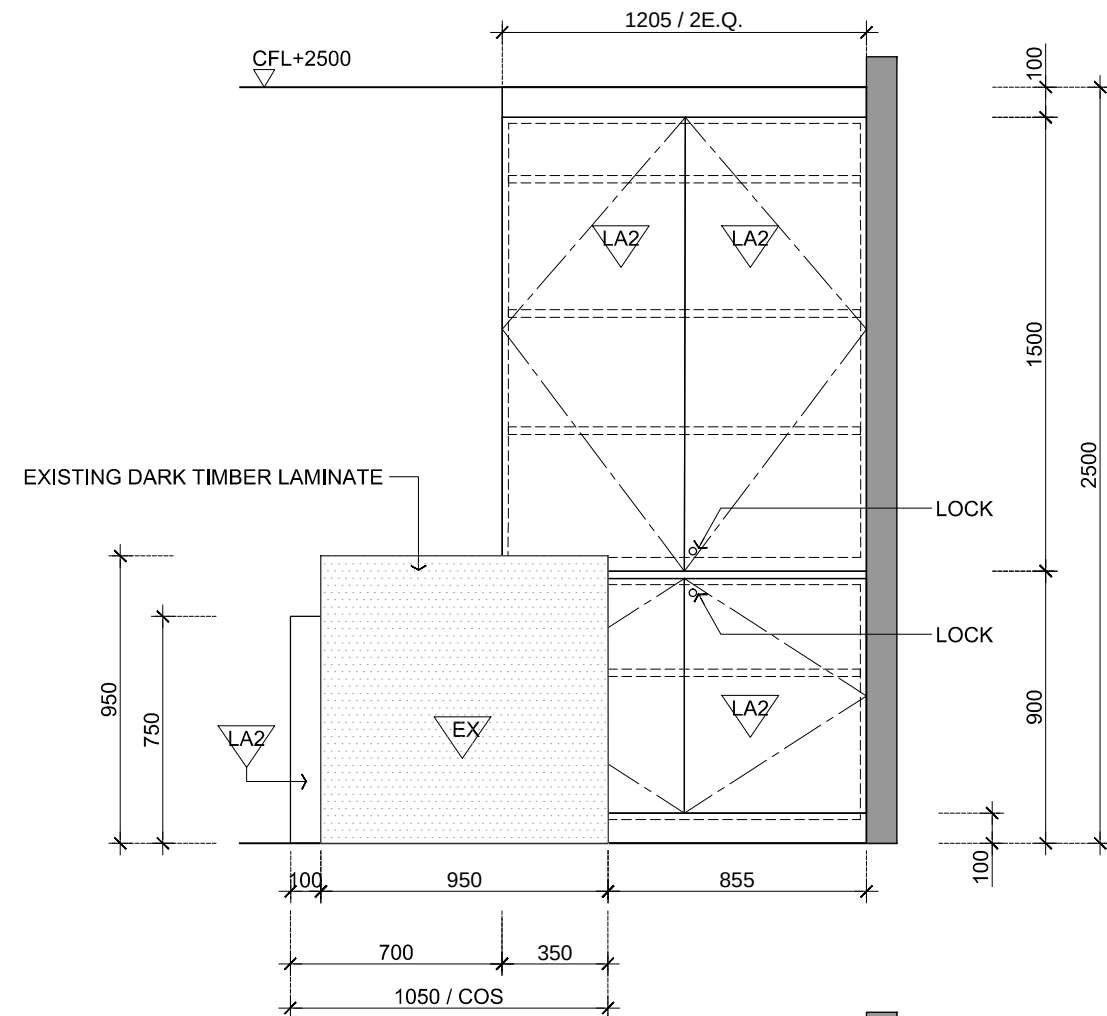

ELEVATION 3
Scale: 1:25

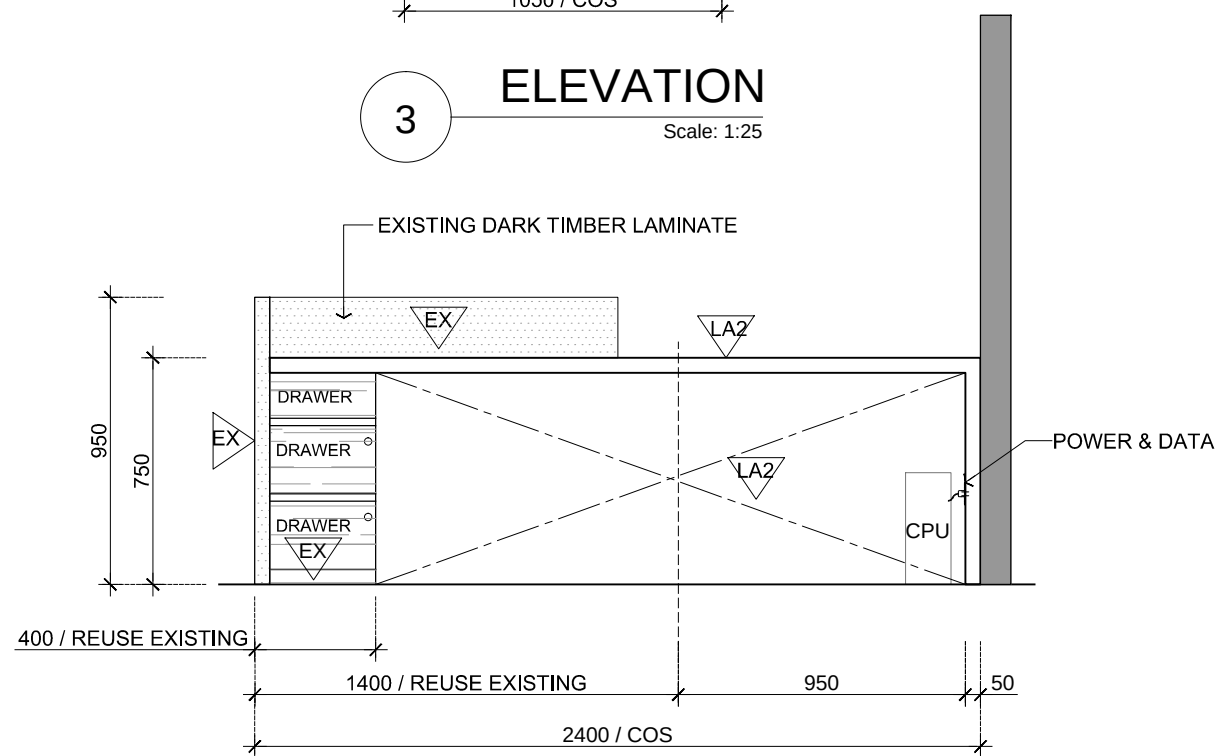

ELEVATION 2
Scale: 1:25

REFERENCE MAP

NORTH

NOTES

- DO NOT SCALE DRAWINGS. WRITTEN DIMENSIONS GOVERN.
- ALL DIMENSIONS ARE IN MILLIMETERS UNLESS NOTED OTHERWISE.
- ALL DIMENSIONS SHALL BE VERIFIED ON SITE BEFORE PROCEEDING WITH THE WORK. LUX89 SHALL BE NOTIFIED IN WRITING OF ANY DISCREPANCIES.
- THIS DRAWING MUST BE READ IN CONJUNCTION WITH ALL RELEVANT CONTRACTS, SPECIFICATIONS, REPORTS AND DRAWINGS.

© 2020 COPYRIGHT OF THIS DRAWING IS VESTED IN LUX89 CO., LTD.

THIS DRAWING IS AN UNCONTROLLED COPY, UNLESS NOTED OTHERWISE

T1	CP	FOR TENDER	10/04/2020
REV	BY	DESCRIPTION	DATE

CLIENT / PROJECT

**Tilleke & Gibbins
Myanmar Limited.**

PROJECT MANAGER & INTERIOR DESIGNER

LUX 89 CO., LTD.
7/89 Soi Rama 2 Soi 54/4 Samae Dam,
Bang Khun Thian, Bangkok, Thailand 10150
E LUX89.BKK@GMAIL.COM W LUX89.COM
T 66(2) 416 9189

ARCHITECTURE

STRUCTURE ENGINEER

M&E ENGINEER

ACCO ENGINEERING CO., LTD.
1213/430 Soi Ladprao94 (Panjamit) Plubpla, Wang Thonglang,
Bangkok, Thailand. 10310
E APISAK@ACCO.CO.TH W ACCO@ACCO.CO.TH
T 66(2) 559 0177-9, F 66 (2) 559 0176

DRAWING

JOINERY DETAILS

JU-09

STATUS

FOR TENDER

SCALE AT A3	DRAWN	CO-ORDINATED	CHECKED	PLOTTED
1:25	AK	CP	CP	10/04/2020
JOB NO.	DRAWING NUMBER	REVISION		
PTD 20.001	D-809	T1		



© LUX89 CO., LTD. April 2020

REFERENCE MAP	DEPTH

NOTES

1. DO NOT SCALE DRAWINGS. WRITTEN DIMENSIONS GOVERN.
2. ALL DIMENSIONS ARE IN MILLIMETERS UNLESS NOTED OTHERWISE.
3. ALL DIMENSIONS SHALL BE VERIFIED ON SITE BEFORE PROCEEDING WITH THE WORK. LUX89 SHALL BE NOTIFIED IN WRITING OF ANY DISCREPANCIES.
4. THIS DRAWING MUST BE READ IN CONJUNCTION WITH ALL RELEVANT CONTRACTS, SPECIFICATIONS, REPORTS AND DRAWINGS.

©2020 COPYRIGHT OF THIS DRAWING IS VESTED IN LUX89 CO., LTD.

THIS DRAWING IS AN UNCONTROLLED COPY, UNLESS NOTED OTHERWISE

[illegible]

T1	CP	FOR TENDER	10/04/2020
REV	BY	DESCRIPTION	DATE

CLIENT / PROJECT

**Tilleke & Gibbins
Myanmar Limited.**

PROJECT MANAGER & INTERIOR DESIGNER

LUX 89 CO., LTD.
7/89 Soi Rama 2 Soi 54/4, Samae Dam,
Bang Khun Thian, Bangkok, Thailand 10150
E LUX89.BKK@GMAIL.COM W LUX89.COM
T 66(2) 416 9189

68 Xn7

ARCHITECTURE

STRUCTURE ENGINEER

M&E ENGINEER

ACCO ENGINEERING CO., LTD.
1213/430 Soi Ladprao94 (Panjamit) Plubpla, Wang Thonglang,
Bangkok, Thailand. 10310
E APISAK@ACCO.CO.TH W ACCO@ACCO.CO.TH
T 66(2) 559 0177-9. F 66 (2) 559 0176

DRAWING


JOINERY DETAILS

JU-09, JU-10

STATUS
FOR TENDER

SCALE AT 1:1.35	DRAWN	CO-ORDINATED	CHECKED	PLOTTED DATE
1:10	AK	CP	CP	10/04/2020
JOB NO.	DRAWING NUMBER			REVISION
PTD 20.001	D-809.1			T1



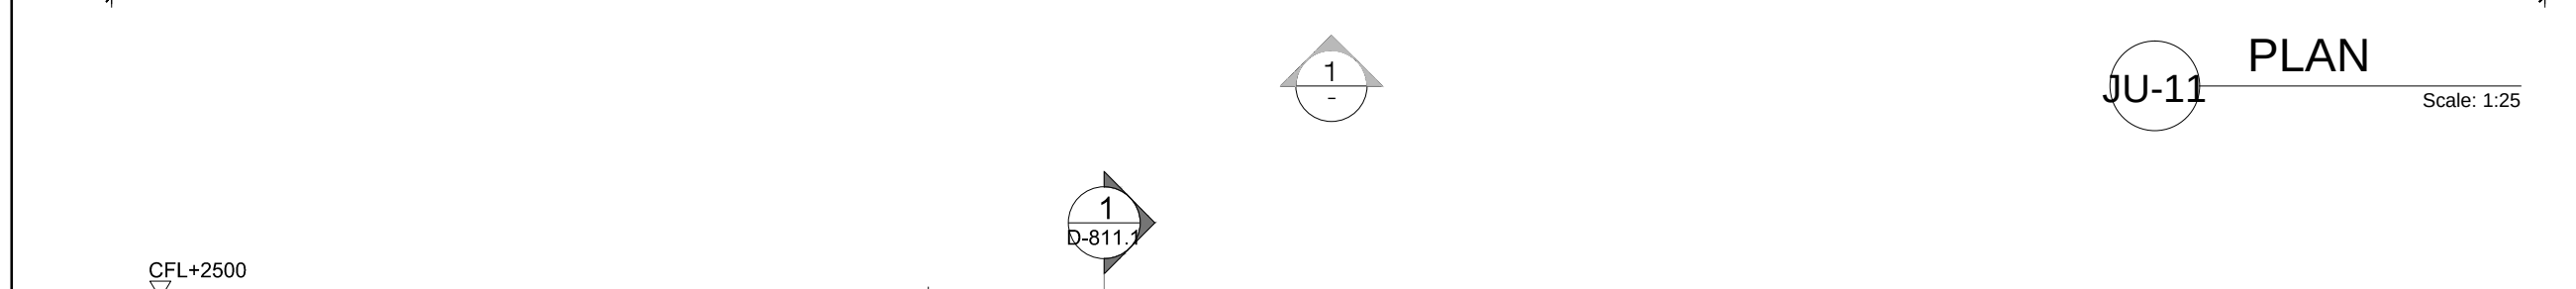



STATUS				
FOR TENDER				
SCALE AT #143	DRUM	CO-ORIENTED	CHECKED	POSTDATE
1:25	AK	CP	CP	10/04/2020
ASS. NO.		TRAINING NUMBER		REVISION
PTD 20.001		D-811		T1

© LUX89 CO., LTD. April 2020




REFERENCE MAP		NORTH	
NOTES 1. DO NOT SCALE DRAWINGS. WRITTEN DIMENSIONS GOVERN. 2. ALL DIMENSIONS ARE IN MILLIMETERS UNLESS NOTED OTHERWISE. 3. ALL DIMENSIONS SHALL BE VERIFIED ON SITE BEFORE PROCEEDING WITH THE WORK. LUX89 SHALL BE NOTIFIED IN WRITING OF ANY DISCREPANCIES. 4. THIS DRAWING MUST BE READ IN CONJUNCTION WITH ALL RELEVANT CONTRACTS, SPECIFICATIONS, REPORTS AND DRAWINGS. © 2020 COPYRIGHT OF THIS DRAWING IS VESTED IN LUX89 CO., LTD.			
THIS DRAWING IS AN UNCONTROLLED COPY, UNLESS NOTED OTHERWISE			
T1	CP	FOR TENDER	10/04/2020
REV	BY	DESCRIPTION	DATE
CLIENT / PROJECT			
Tilleke & Gibbins Myanmar Limited. PROJECT MANAGER & INTERIOR DESIGNER LUX 89 CO., LTD. 7/89 Soi Rama 2 Soi 54/4,Samae Dam, Bang Khun Thian, Bangkok , Thailand10150 E LUX89.BKK@GMAIL.COM W LUX89.COM T 66(2) 416 9189 ARCHITECTURE STRUCTURE ENGINEER M&E ENGINEER ACCO ENGINEERING CO., LTD. 1213/430 Soi Ladprao94 (Panjarnit) Plubpha, Wang Thonglang, Bangkok, Thailand. 10310 E APISAK@ACCO.CO.TH W ACCO@ACCO.CO.TH T 66(2) 559 0177-9, F 66 (2) 559 0176 DRAWING JOINERY DETAILS JU-11, JU-12			
STATUS			
FOR TENDER			
SCALE AT 1:10	DRAWN	CORROBORATED	CHECKED
1 : 10	AJK	CP	CP
JOB NO.	DRAWING NUMBER	REVISION	
PTD 20.001	D-811.1	T1	

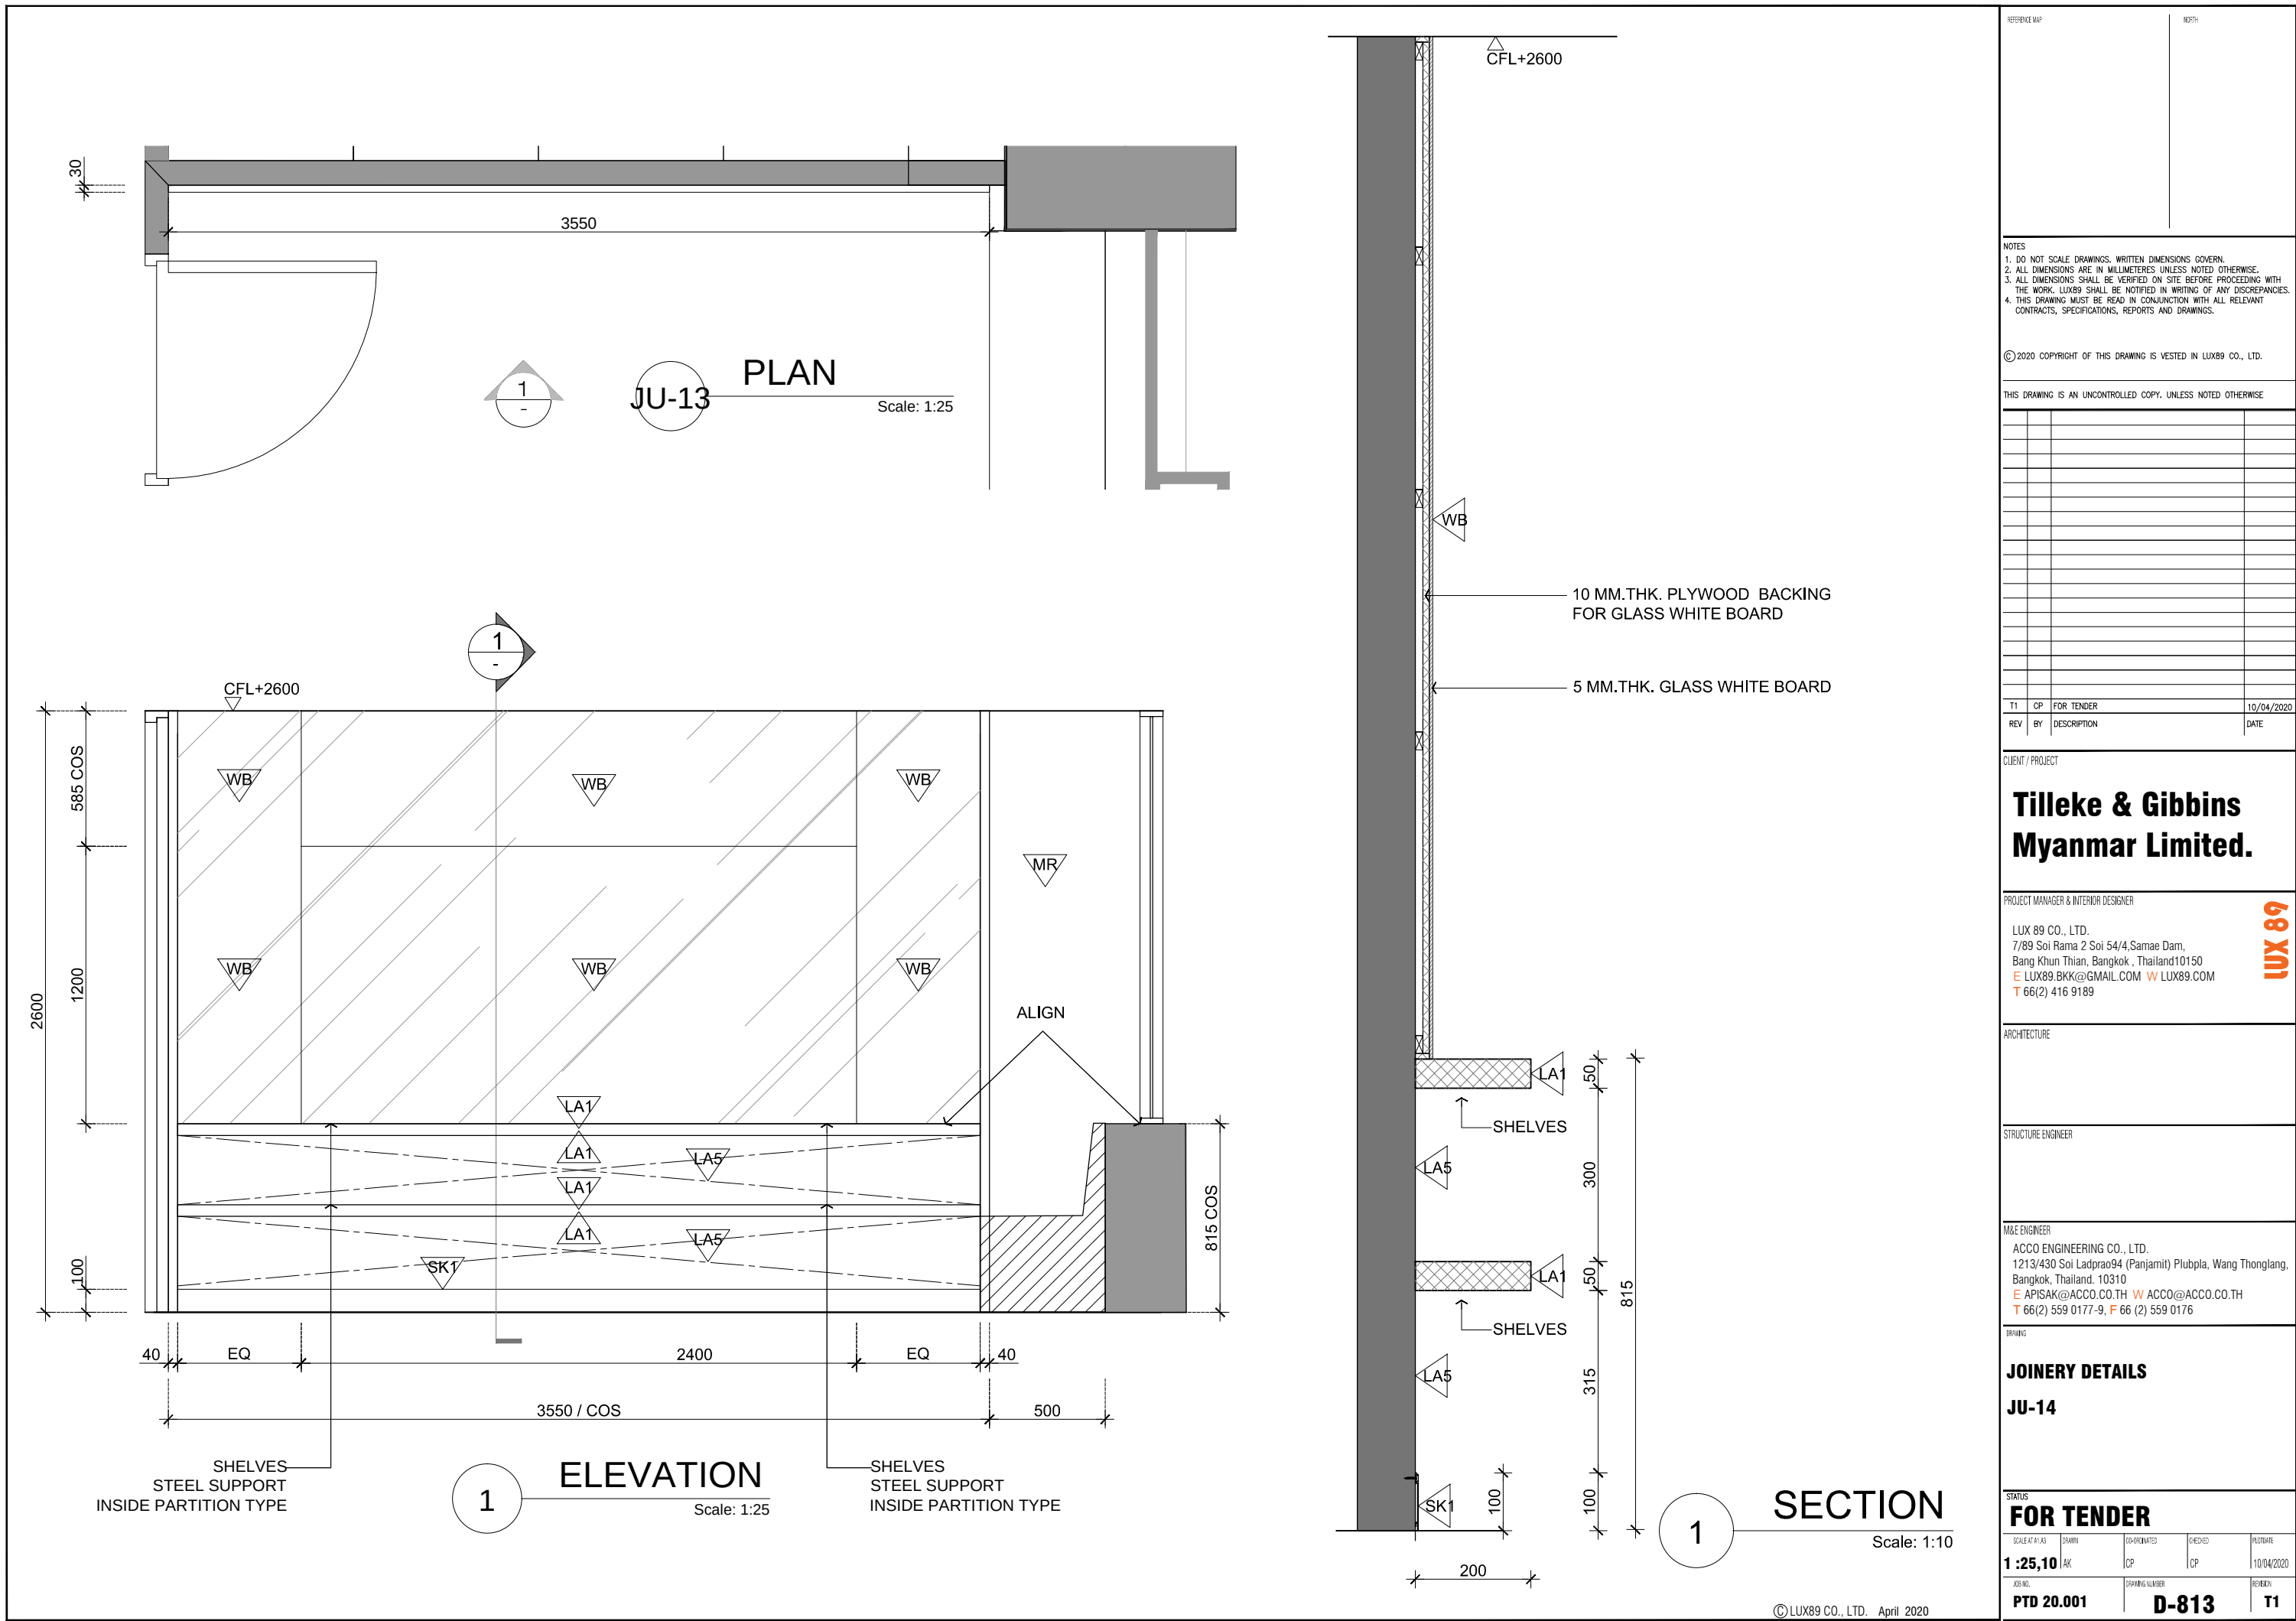


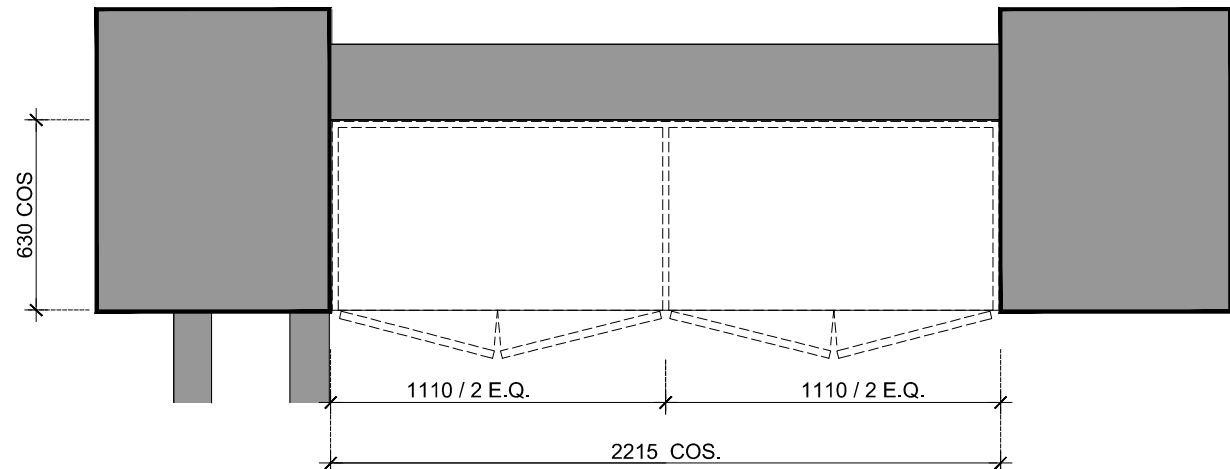

PLAN
JU-14 Scale: 1:25

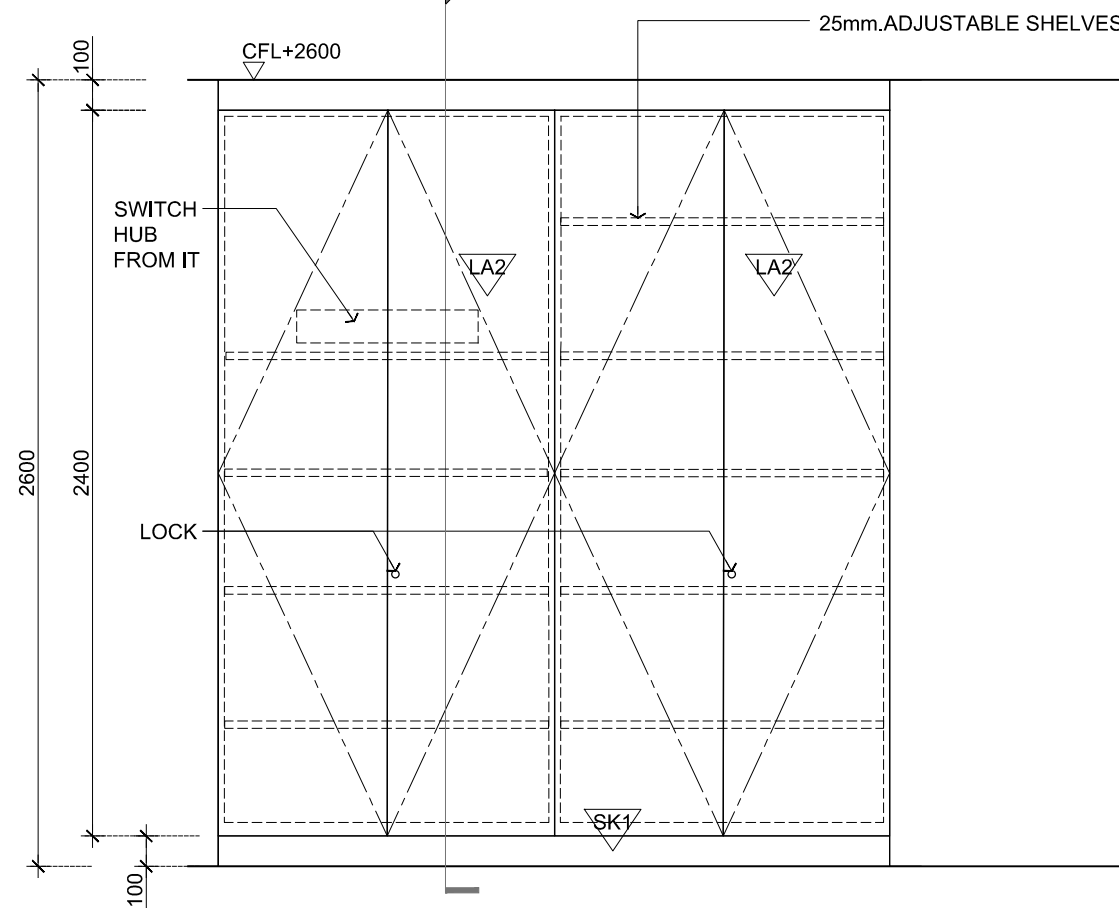

ELEVATION
1 Scale: 1:25

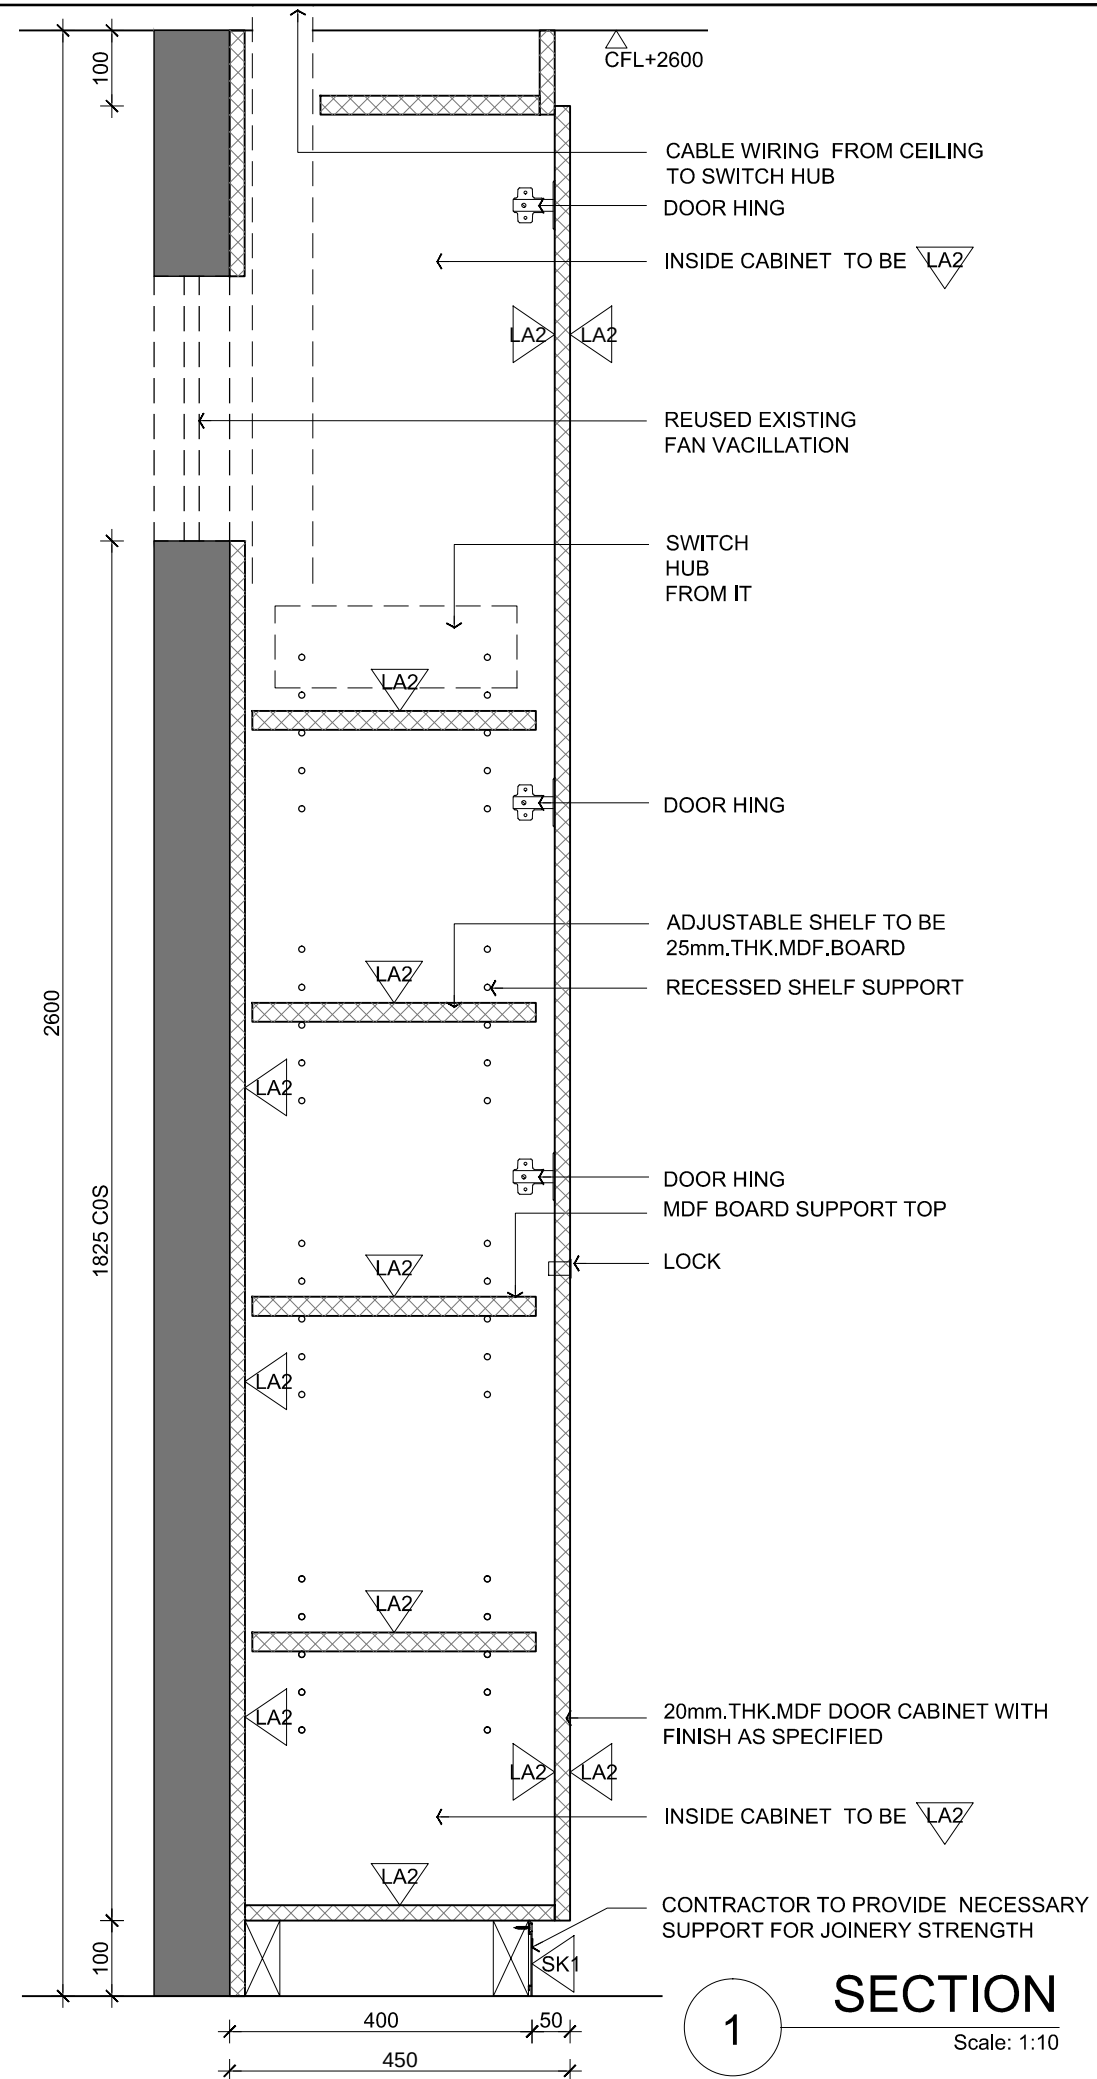

SECTION
1 Scale: 1:10

REFERENCE MAP

NORTH

NOTES

1. DO NOT SCALE. DRAWINGS. WRITTEN DIMENSIONS GOVERN.

2. ALL DIMENSIONS ARE IN MILLIMETERS UNLESS NOTED OTHERWISE.

3. ALL DIMENSIONS SHALL BE VERIFIED ON SITE BEFORE PROCEEDING WITH THE WORK. LUX89 SHALL BE NOTIFIED IN WRITING OF ANY DISCREPANCIES.

4. THIS DRAWING MUST BE READ IN CONJUNCTION WITH ALL RELEVANT CONTRACTS, SPECIFICATIONS, REPORTS AND DRAWINGS.

© 2020 COPYRIGHT OF THIS DRAWING IS VESTED IN LUX89 CO., LTD.

THIS DRAWING IS AN UNCONTROLLED COPY. UNLESS NOTED OTHERWISE
